



ДИЗАЙН ИНТЕРЬЕРА
ПРОСТРАНСТВО ДЛЯ ЖИЗНИ

БАЗОВЫЙ ПРОЕКТ



АЛЬБОМ ЧЕРТЕЖЕЙ



Планировочные решения



Планы электрики



Планы сантехники



Планы освещения



Подбор отделочных материалов

ДАТА: _____




ВАШ ИНТЕРЬЕР –
НАША ПРОФЕССИЯ

Ведомость рабочих чертежей

Имя листа	№ листа
Титульный лист	01
Ведомость рабочих чертежей	02
Обмерочный чертеж	03
План демонтажа	04
План монтажа	05
План расстановки мебели и оборудования	06
План формирования дверных проемов	07
Общий план расстановки сантехнического оборудования	08
План потолков	09
План расстановки осветительного оборудования	10
План расположения розеток и выключателей	11
План управления осветительного оборудования	12
План привязки теплого пола	13
План раскладки напольных покрытий	14
Развертка стен кухонной мебели	15

		Подпись	Дата		Стадия	Лист
Руководитель:					ДП	02
Дизайнер:						
Выполнил:				Ведомость рабочих чертежей		
Заказчик:						

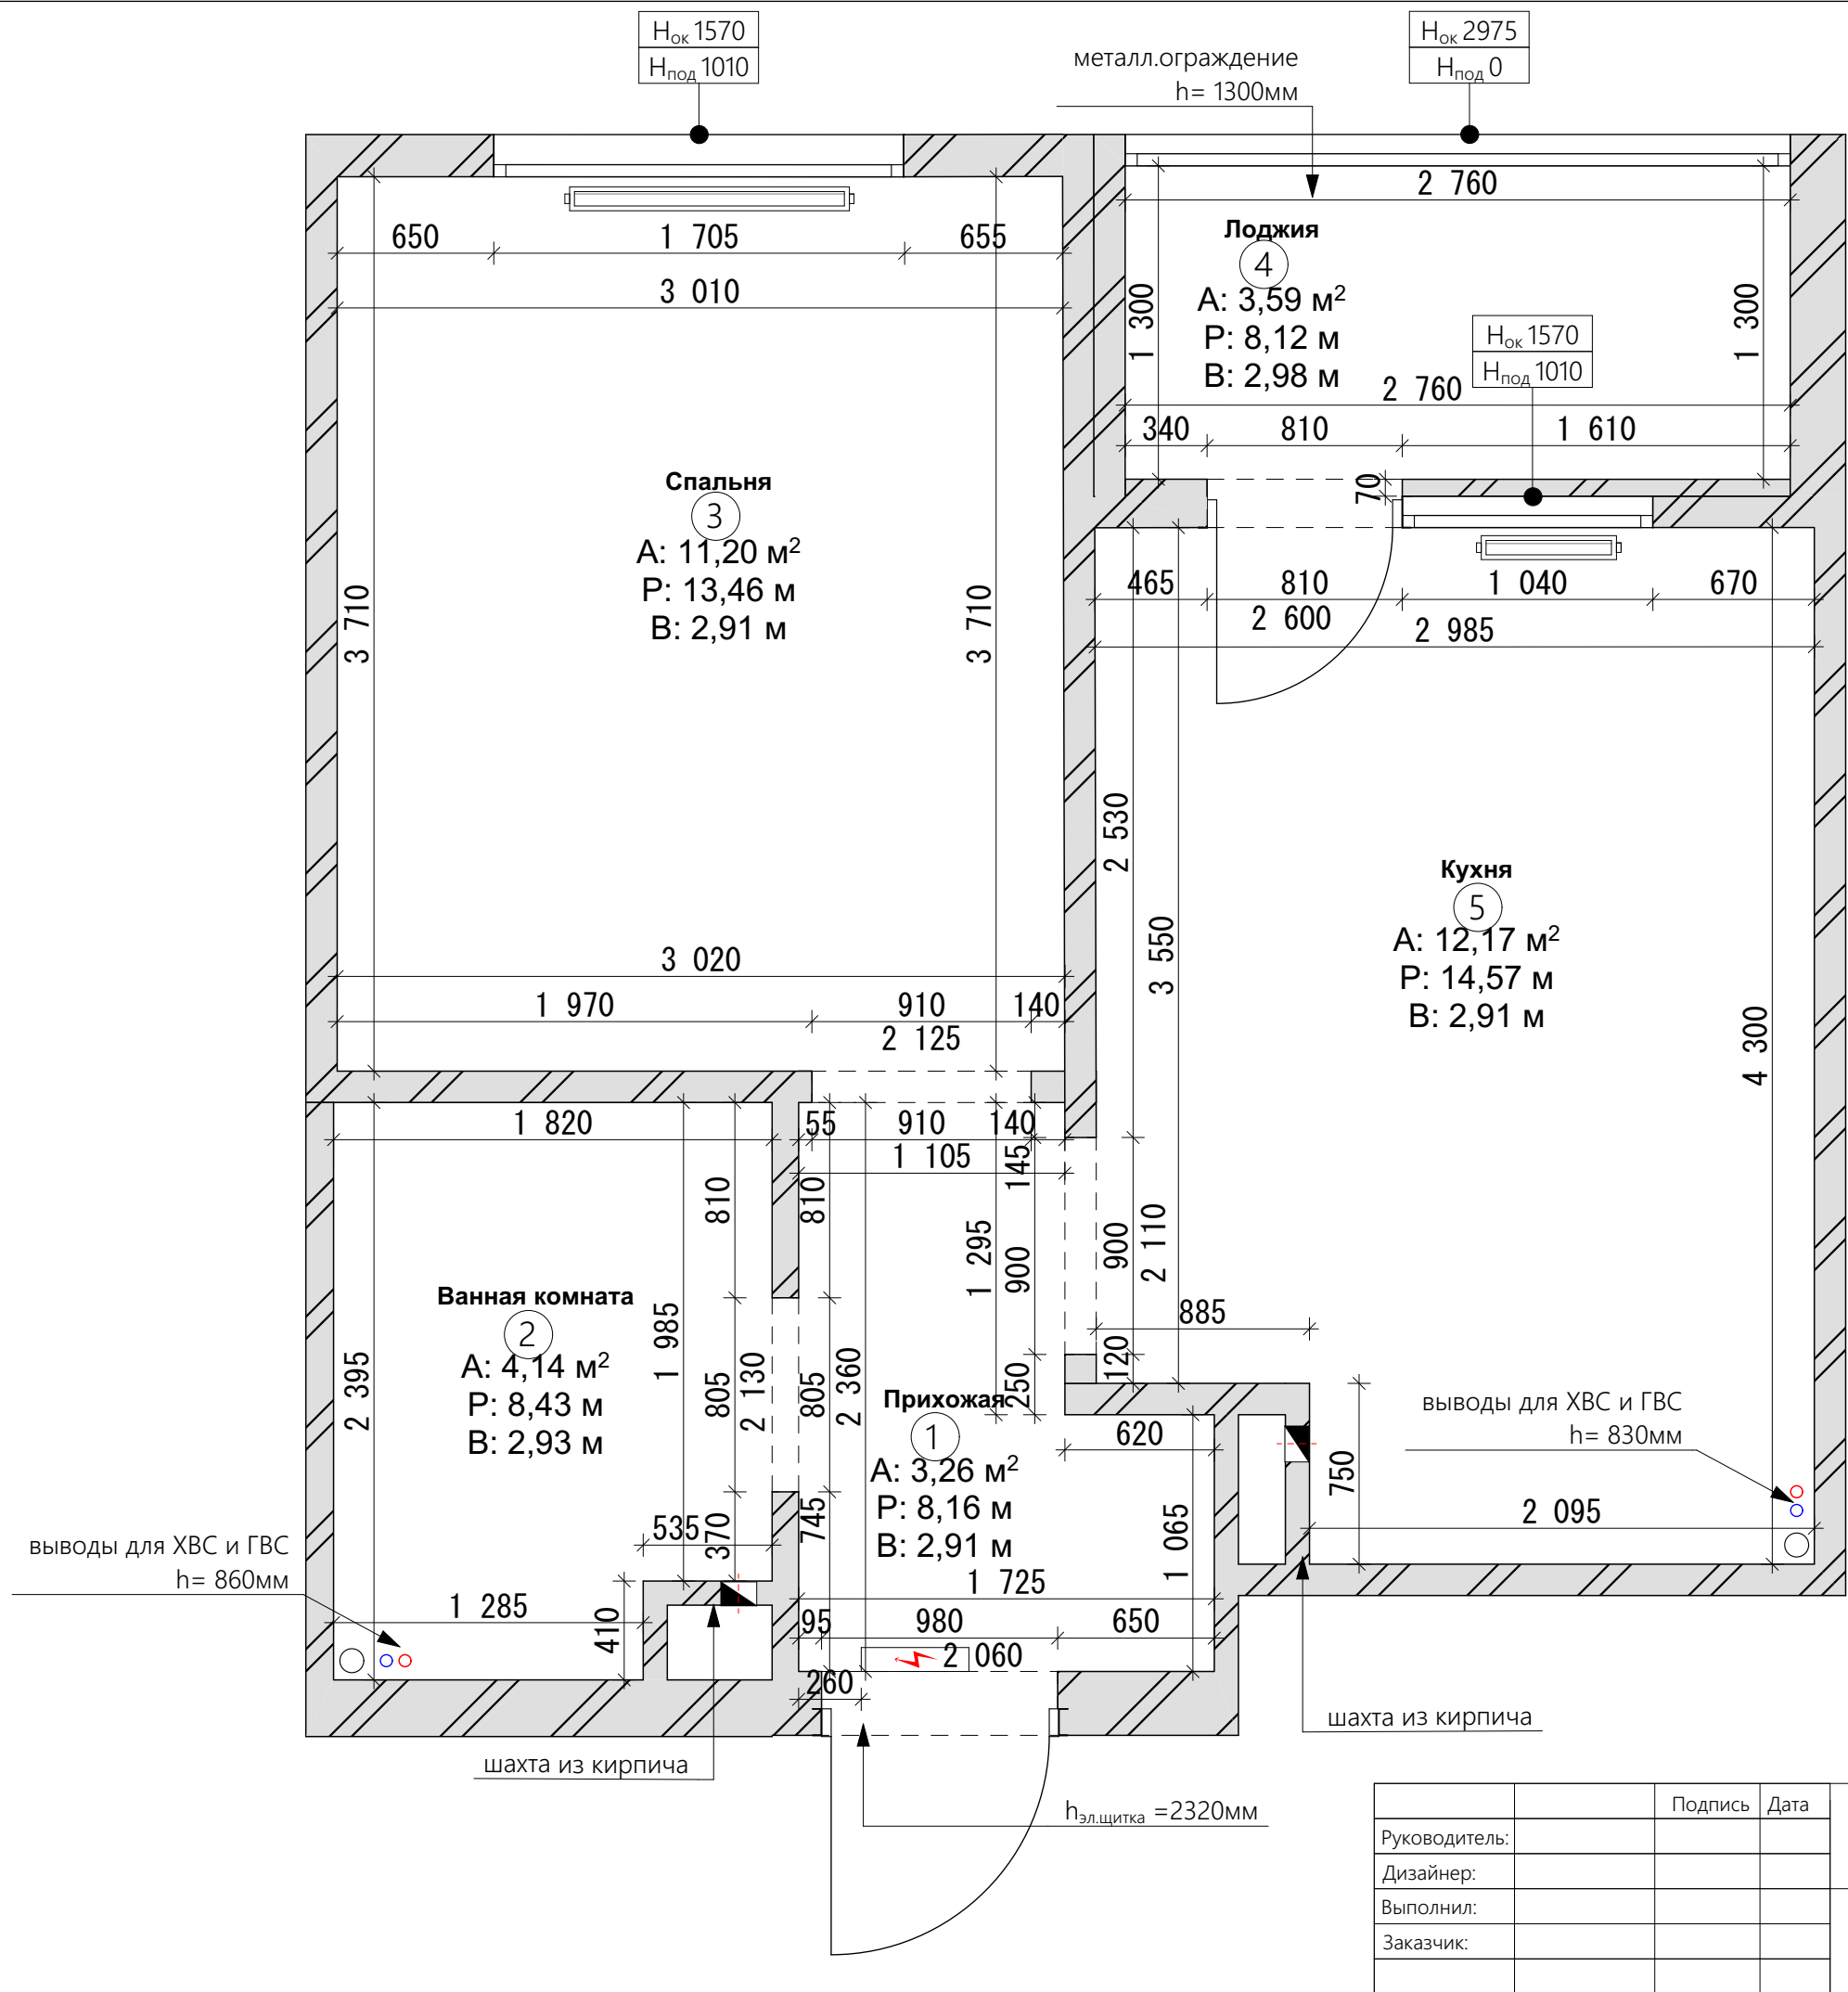

ЭКСПЛИКАЦИЯ ПОМЕЩЕНИЙ		
№	Наименование помещений	Площадь, м²
1	Прихожая	3,26
2	Ванная комната	4,14
3	Спальня	11,20
4	Лоджия	3,59
5	Кухня	12,17
Общая площадь = 34,36 м²		


УСЛОВНЫЕ ОБОЗНАЧЕНИЯ


	существующие стены
	электрощиток
	проем для вентиляции
	водопровод канализация
	радиатор
А - площадь; Р - периметр; В - высота	

ПРИМЕЧАНИЯ

- 1. Все размеры указаны в миллиметрах.
- 2. Все размеры проверить по месту, возможны погрешности.
- 3. Размеры даны без учета отделочных слоев.
- 4. В помещениях 1,3,4,5 присутствует штукатурка.

		Подпись	Дата	Стадия	Лист
Руководитель:					
Дизайнер:				ДП	03
Выполнил:					
Заказчик:				Обмерочный чертеж	

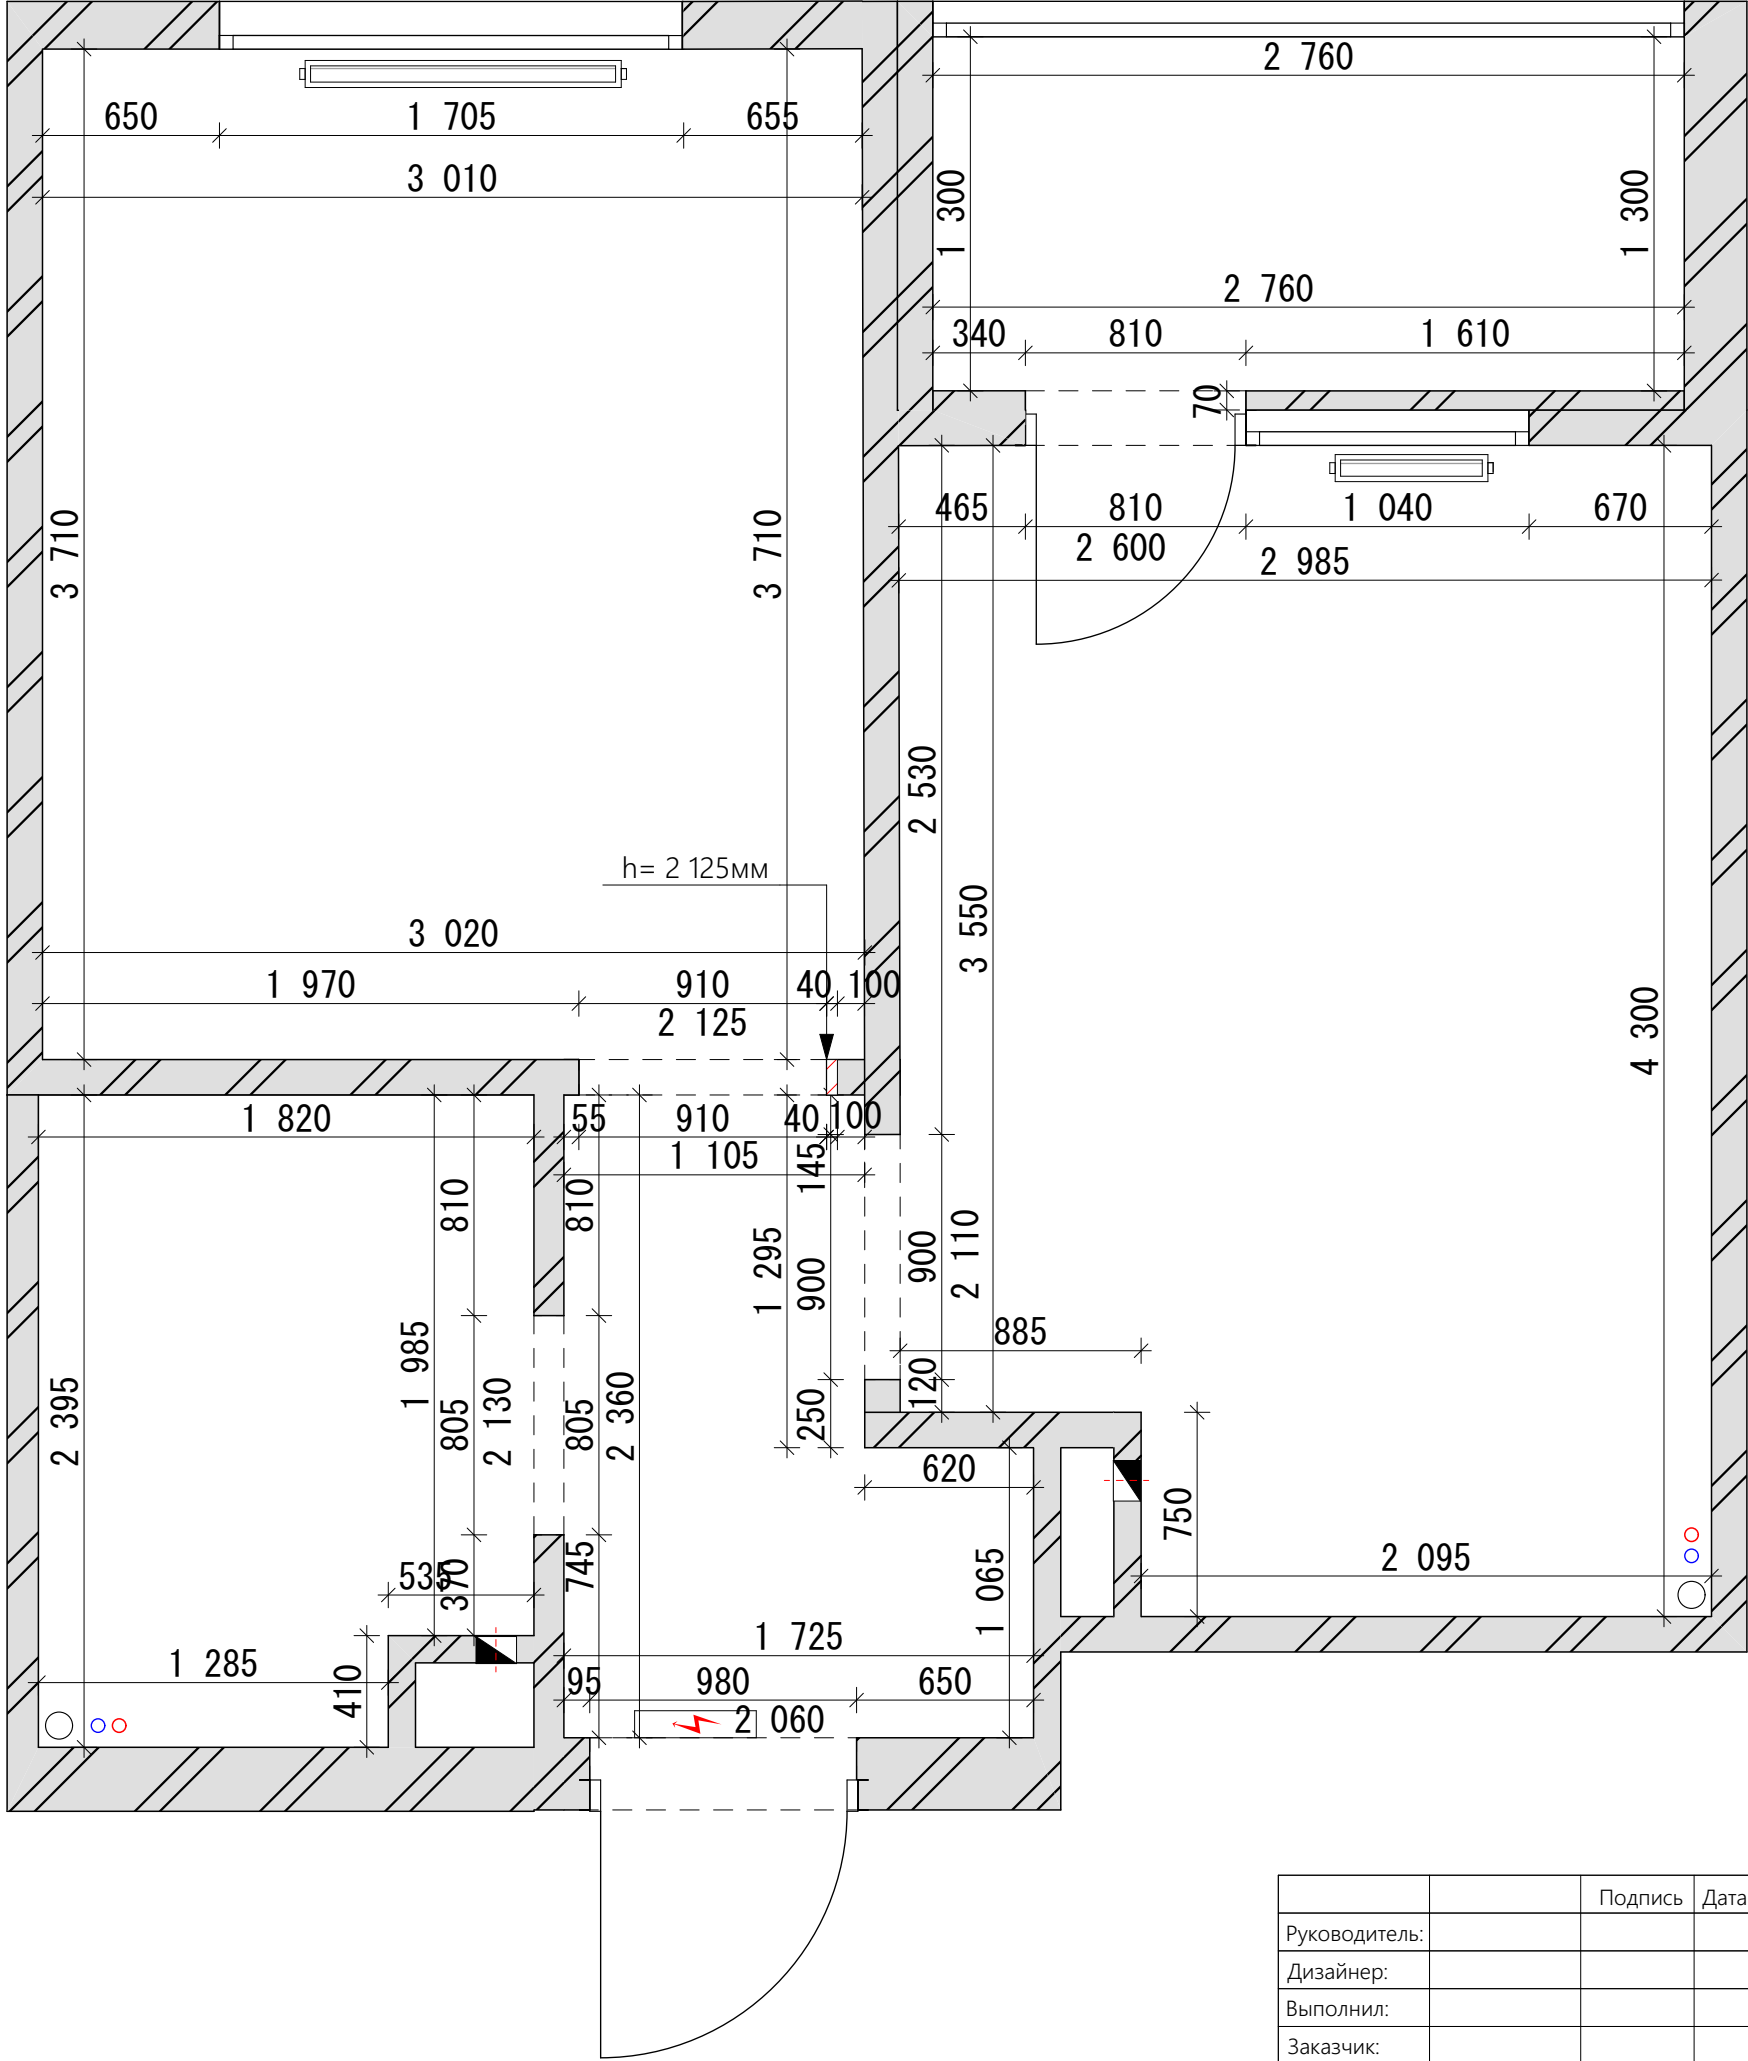

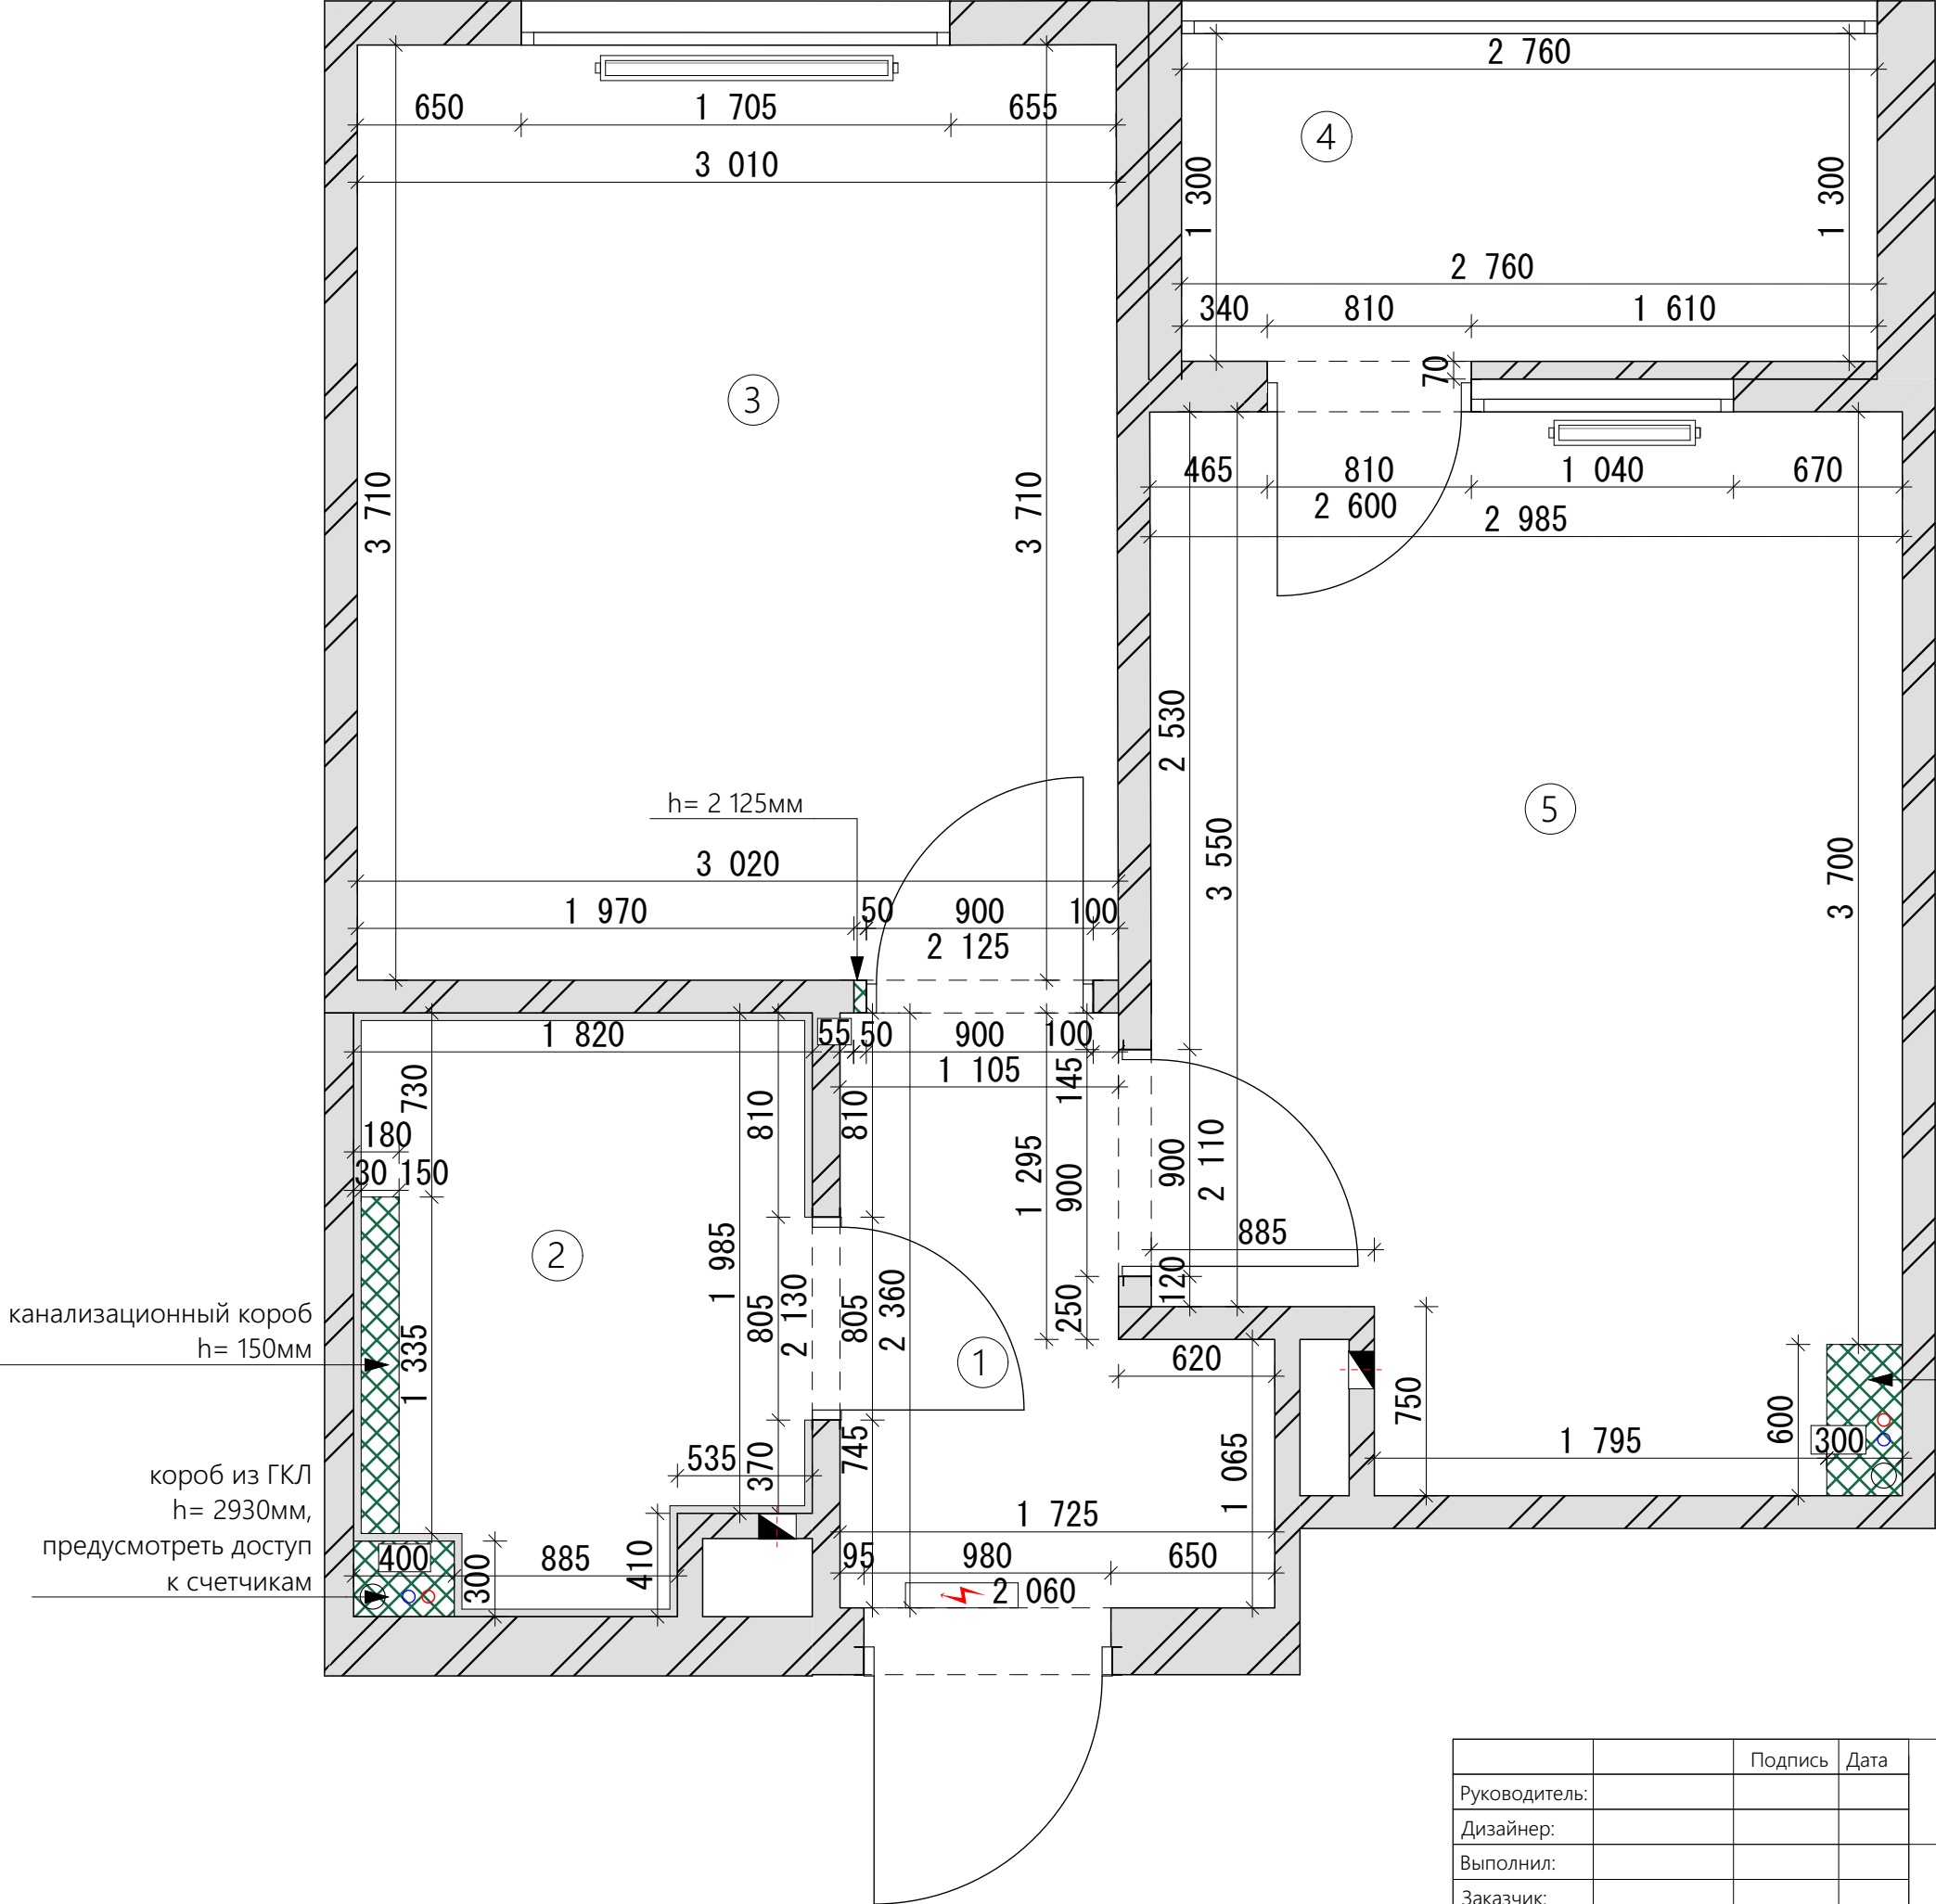

УСЛОВНЫЕ ОБОЗНАЧЕНИЯ

	стены из ГКЛ
	слой штукатурки

ЭКСПЛИКАЦИЯ ПОМЕЩЕНИЙ			
№	Наименование помещений	Площадь помещения, м²	Площадь стен, м²
1	Прихожая	3,26	16,21
2	Ванная комната	4,14	23,37
3	Спальня	11,20	34,53
4	Лоджия	3,59	12,23
5	Кухня	12,17	30,65
		S _{общ} = 34,36 м²	S _{общ} = 116,99 м²

ПРИМЕЧАНИЯ


- Все размеры указаны в миллиметрах.
- Размеры даны без учета отделочных слоев.
- В конструкциях, скрывающих коммуникации предусмотреть лючки.
- Вносимые изменения в существующую планировку квартиры (демонтаж, монтаж, перенос радиаторов, канализации и т.п.) требуют согласования в государственных и муниципальных учреждениях либо самостоятельно, либо через специализированные организации и являются ответственностью Заказчика.
- Высоту и ширину межкомнатных проемов уточнить после окончательного согласования моделей дверей.
- Площадь возводимых конструкций на чертеже и фактическая площадь могут отличаться по техническим моментам.
- Краны перекрытия воды предусмотреть по месту с согласованием прораба и заказчика.
- Вывести углы стен под 90 градусов в санузлах, в местах монтажа плитки на стенах (фартук, декоративные панели) а также на местах монтажа корпусной мебели, панельной отделки.


короб из ГКЛ
h= 2910мм

канализационный короб
h= 150мм

короб из ГКЛ
h= 2930мм,
предусмотреть доступ
к счетчикам

		Подпись	Дата	План монтажа	Стадия	Лист
Руководитель:					ДП	05
Дизайнер:						
Выполнил:						
Заказчик:						

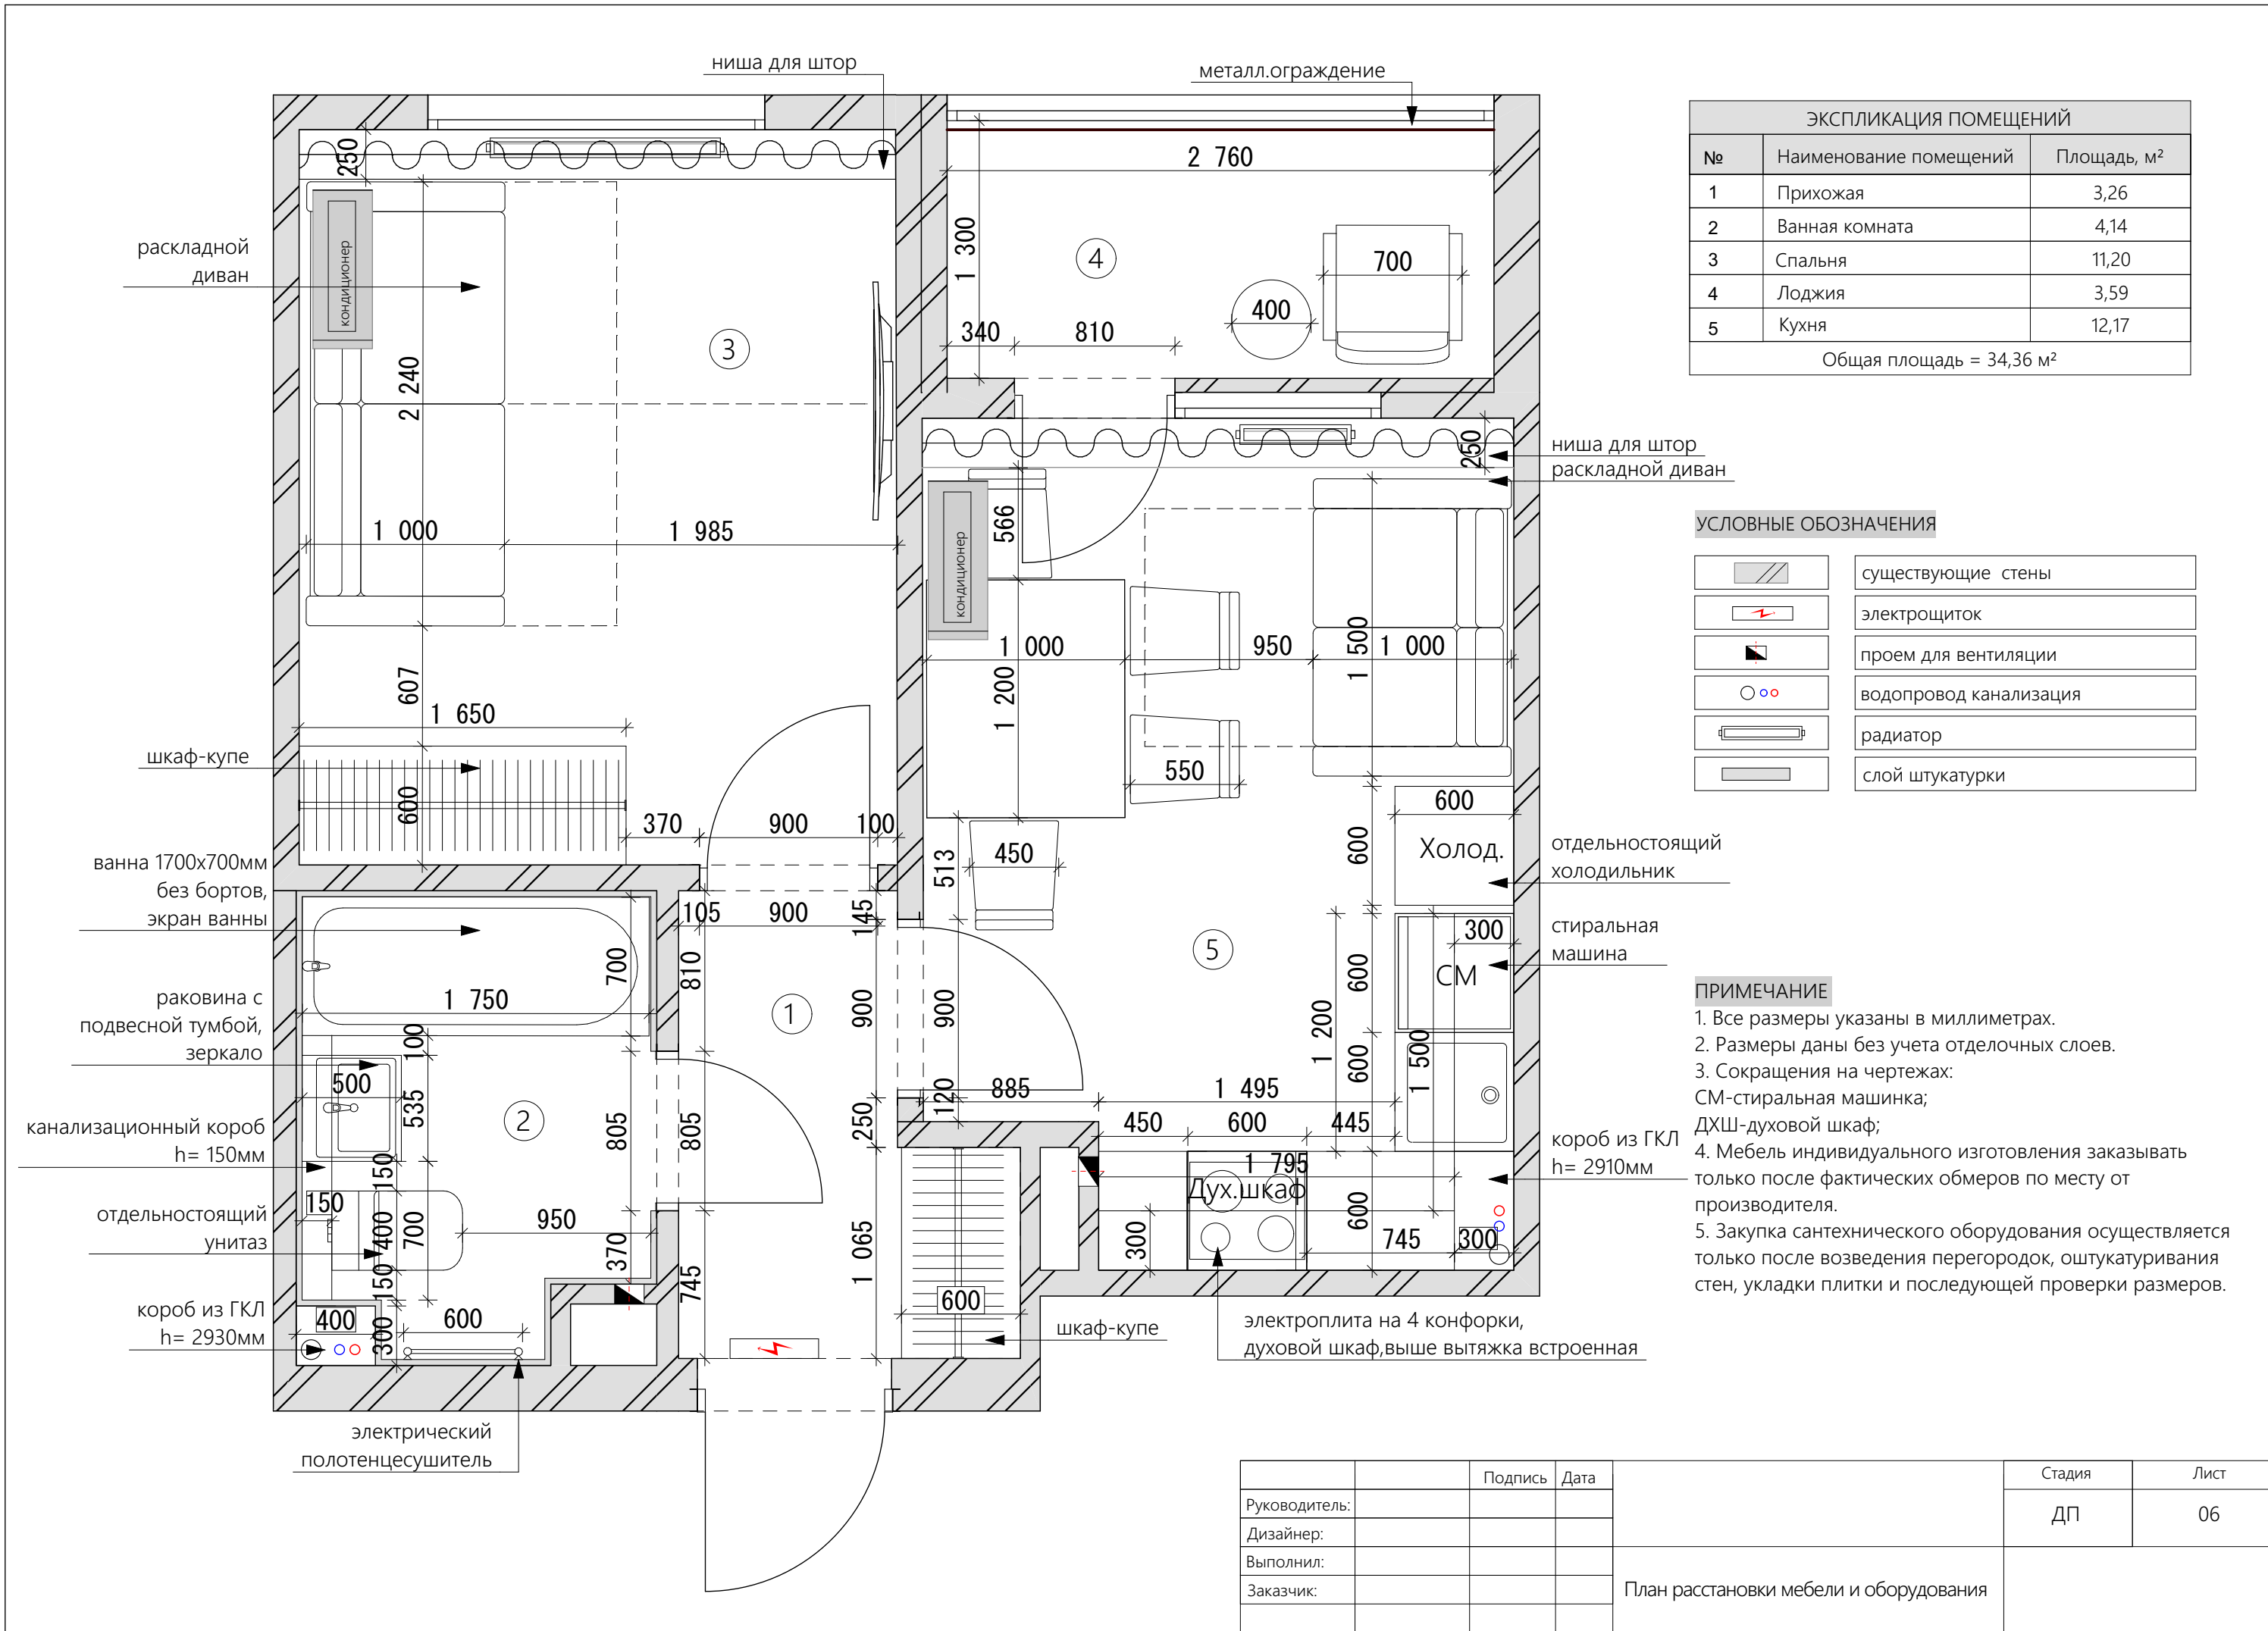

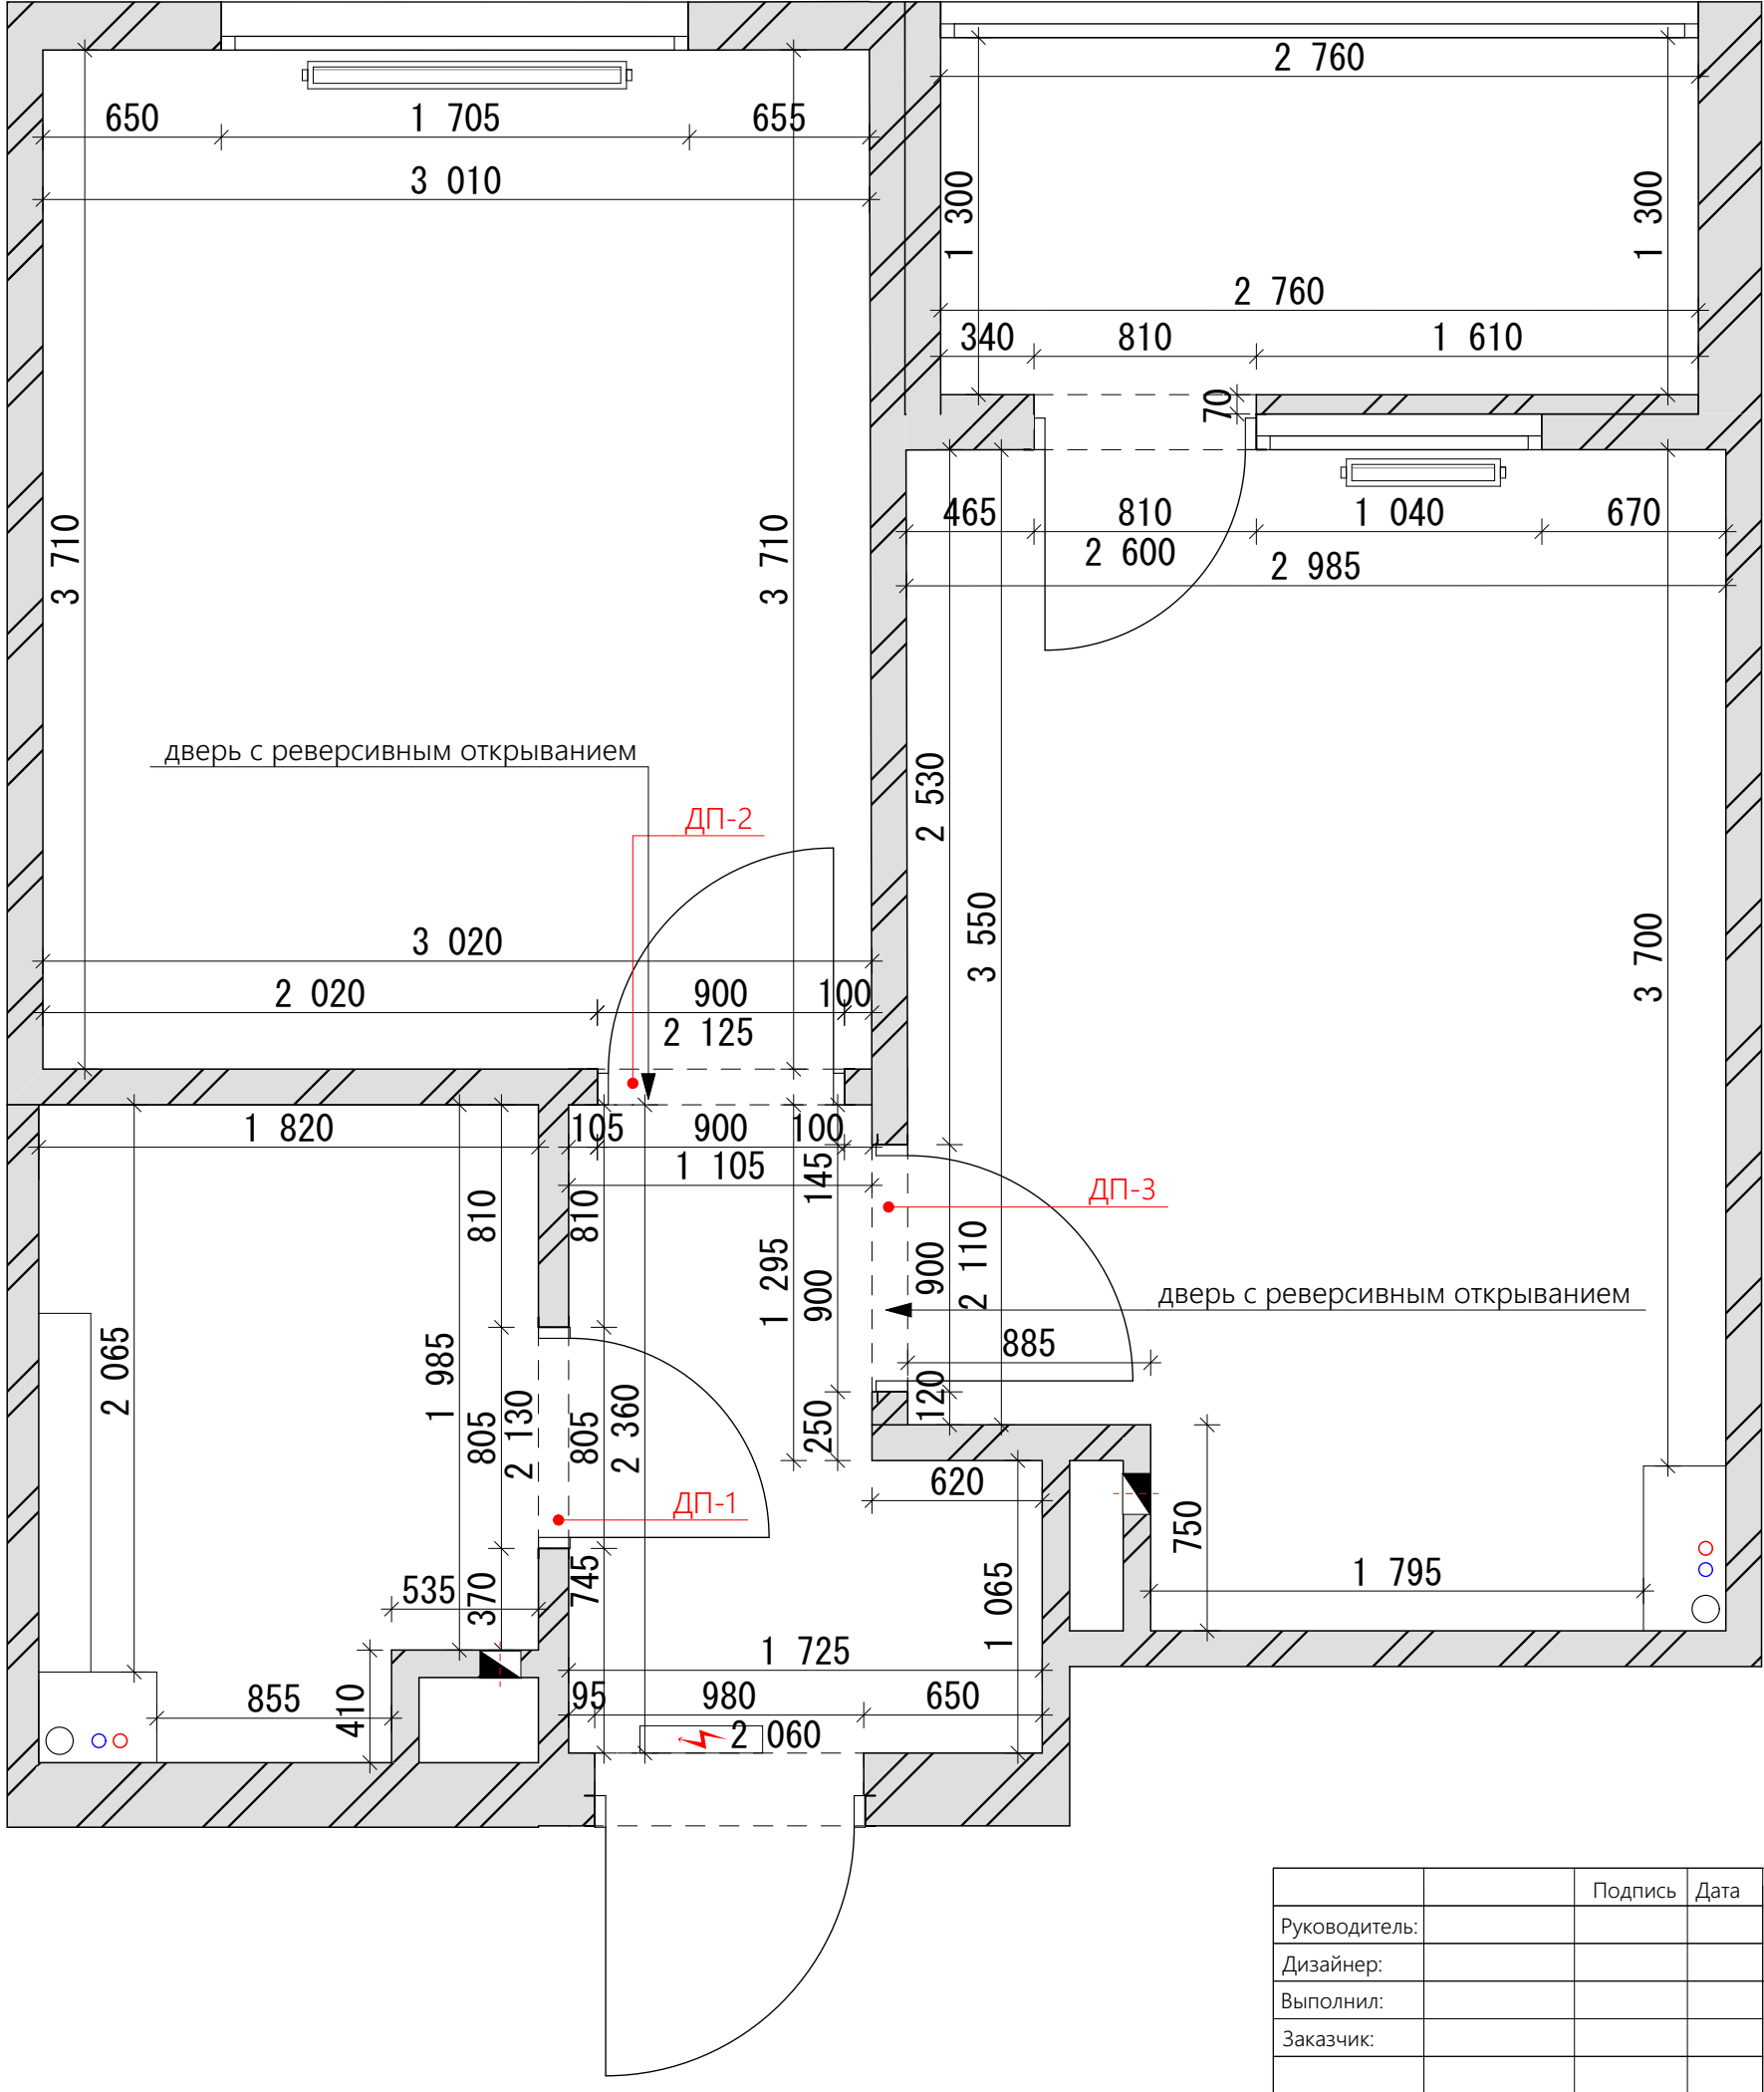



ВЕДОМОСТЬ ДВЕРНЫХ ПОЛОТЕН	
№	Размер дверного полотна
ДП-1	дверное полотно межкомнат.двери 700х2000мм
ДП-2	дверное полотно межкомнат.двери 800х2000мм
ДП-3	дверное полотно межкомнат.двери 800х2000мм


УСЛОВНЫЕ ОБОЗНАЧЕНИЯ	
	существующие стены

- ПРИМЕЧАНИЯ
1. Все размеры указаны в миллиметрах.
 2. Размеры даны без учета отделочных слоев.
 3. Ширину проёмов проверить, и выполнить в соответствии с требованиям по установке дверных коробок.
 4. Размеры межкомнатных проемов уточнить после окончательного согласования моделей дверей.

		Подпись	Дата	План формирования дверных проемов	Стадия	Лист
Руководитель:					ДП	07
Дизайнер:						
Выполнил:						
Заказчик:						

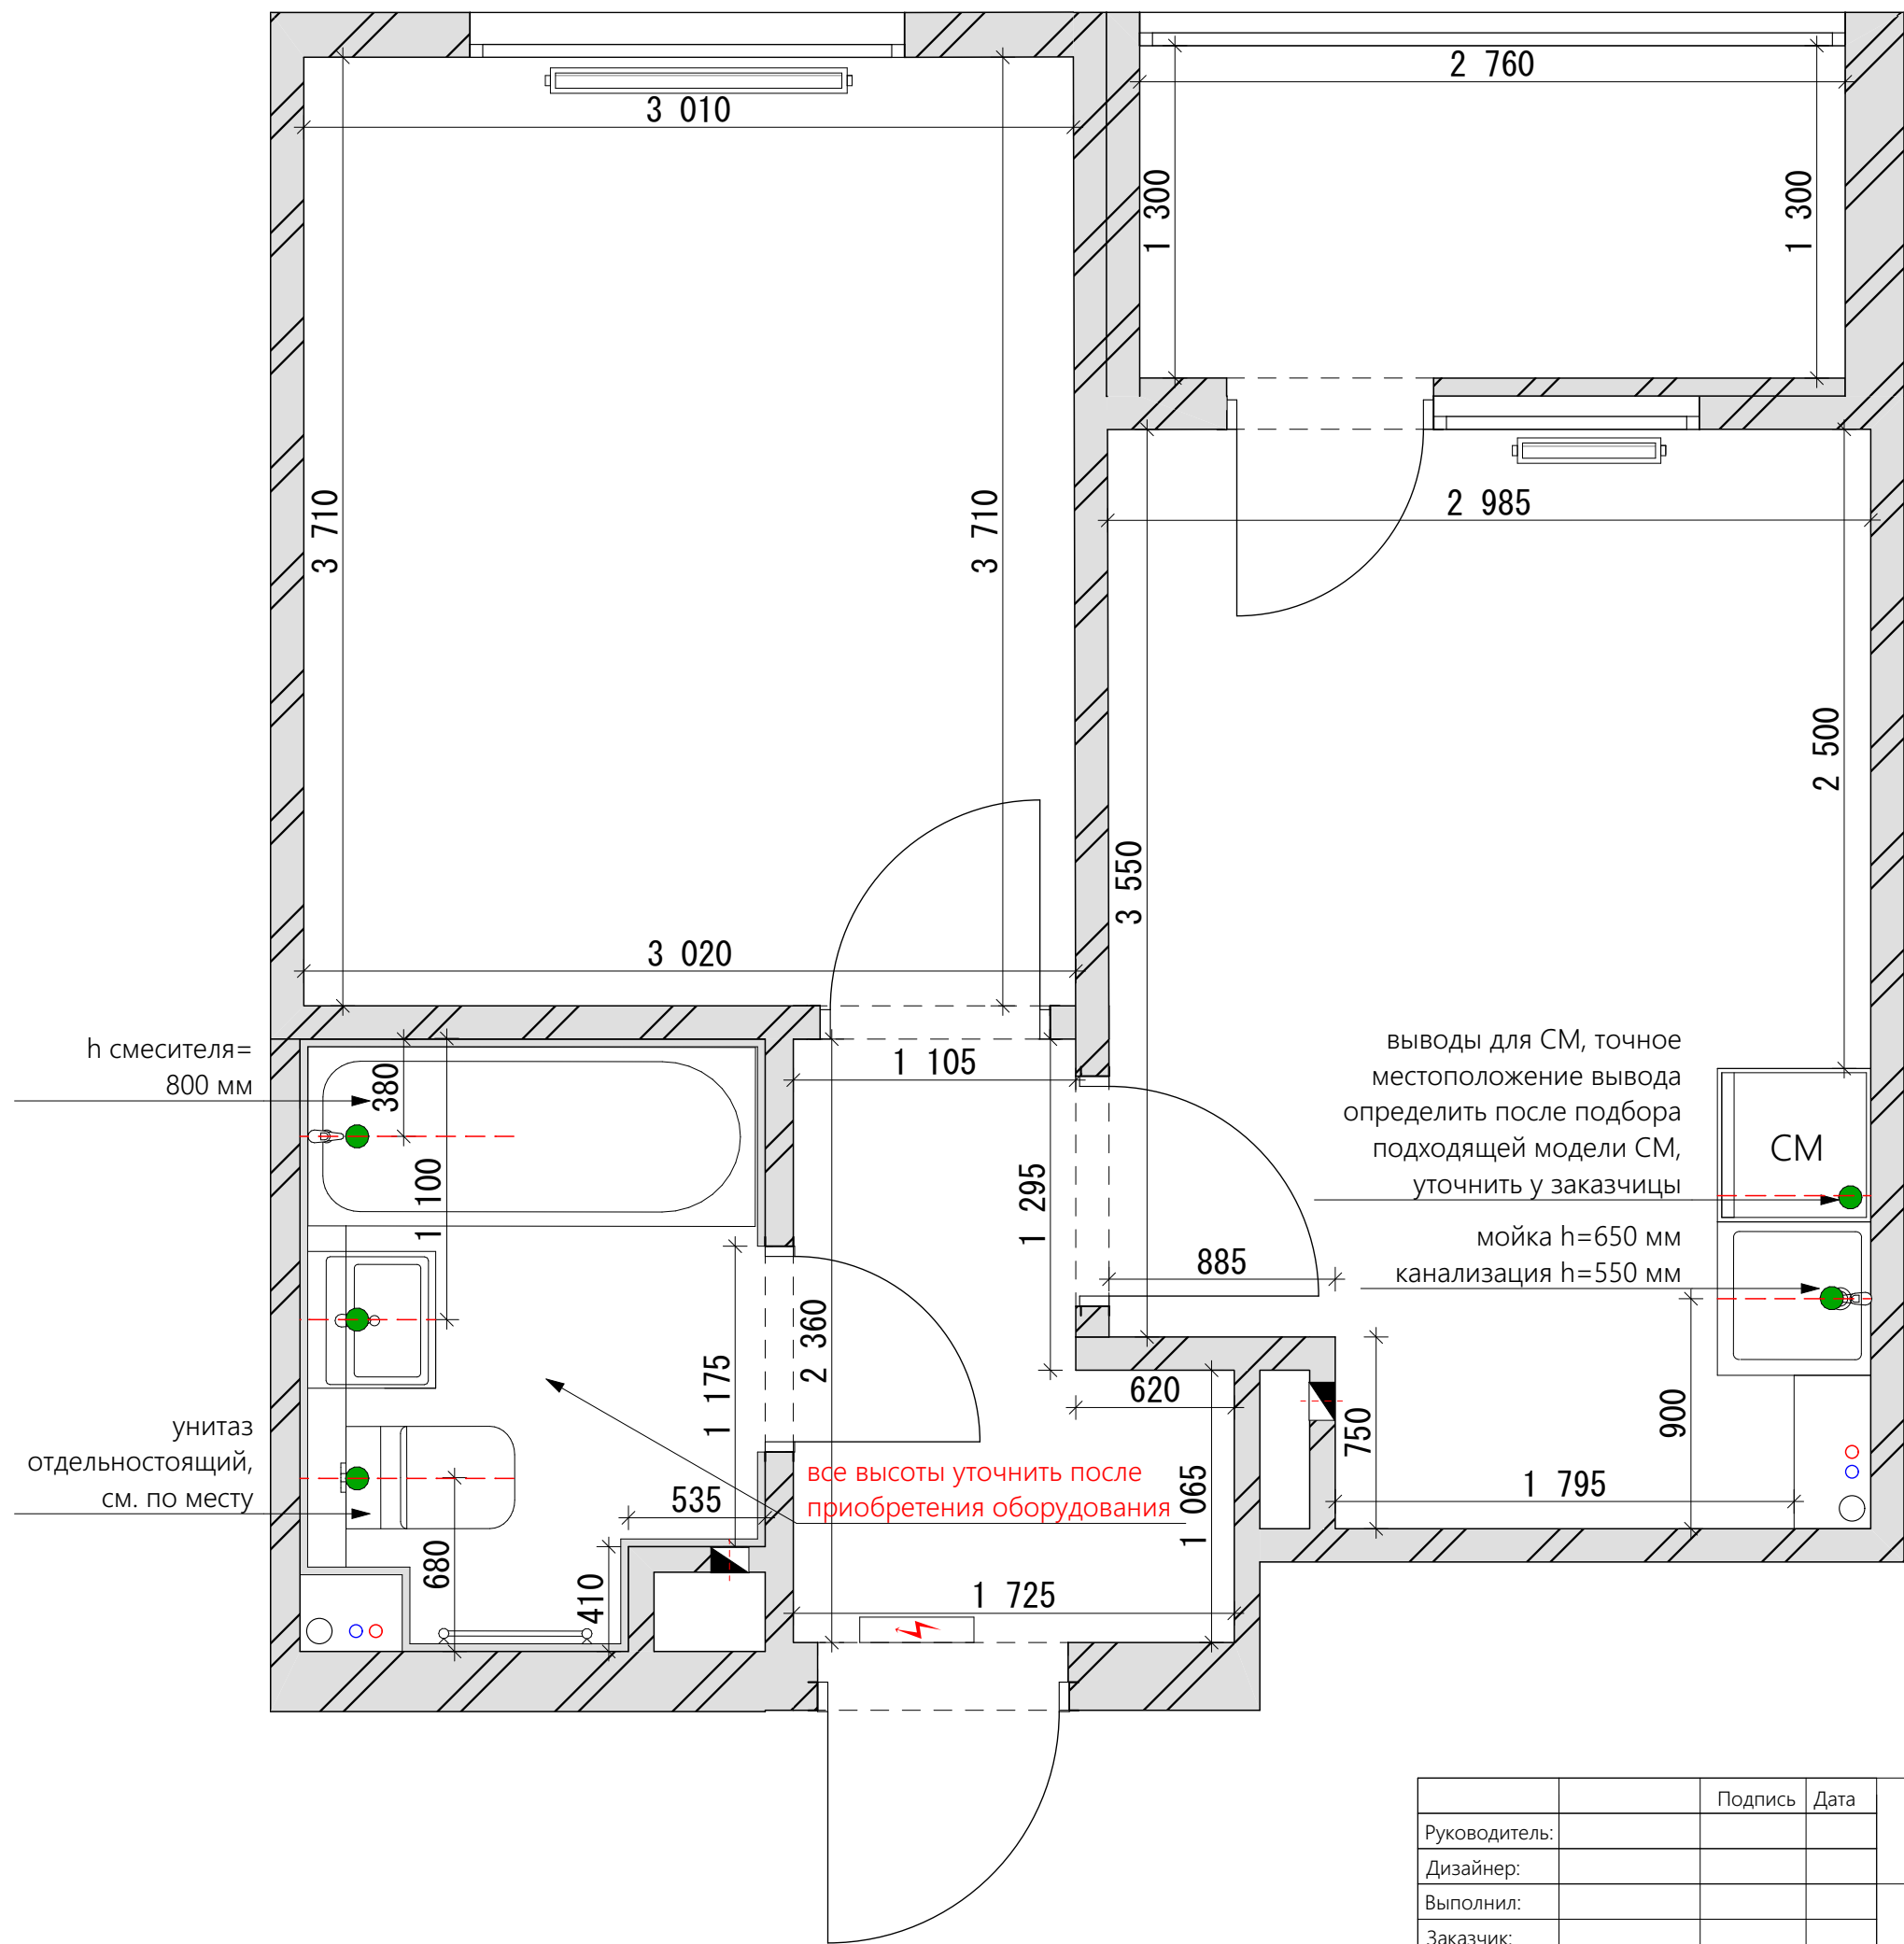

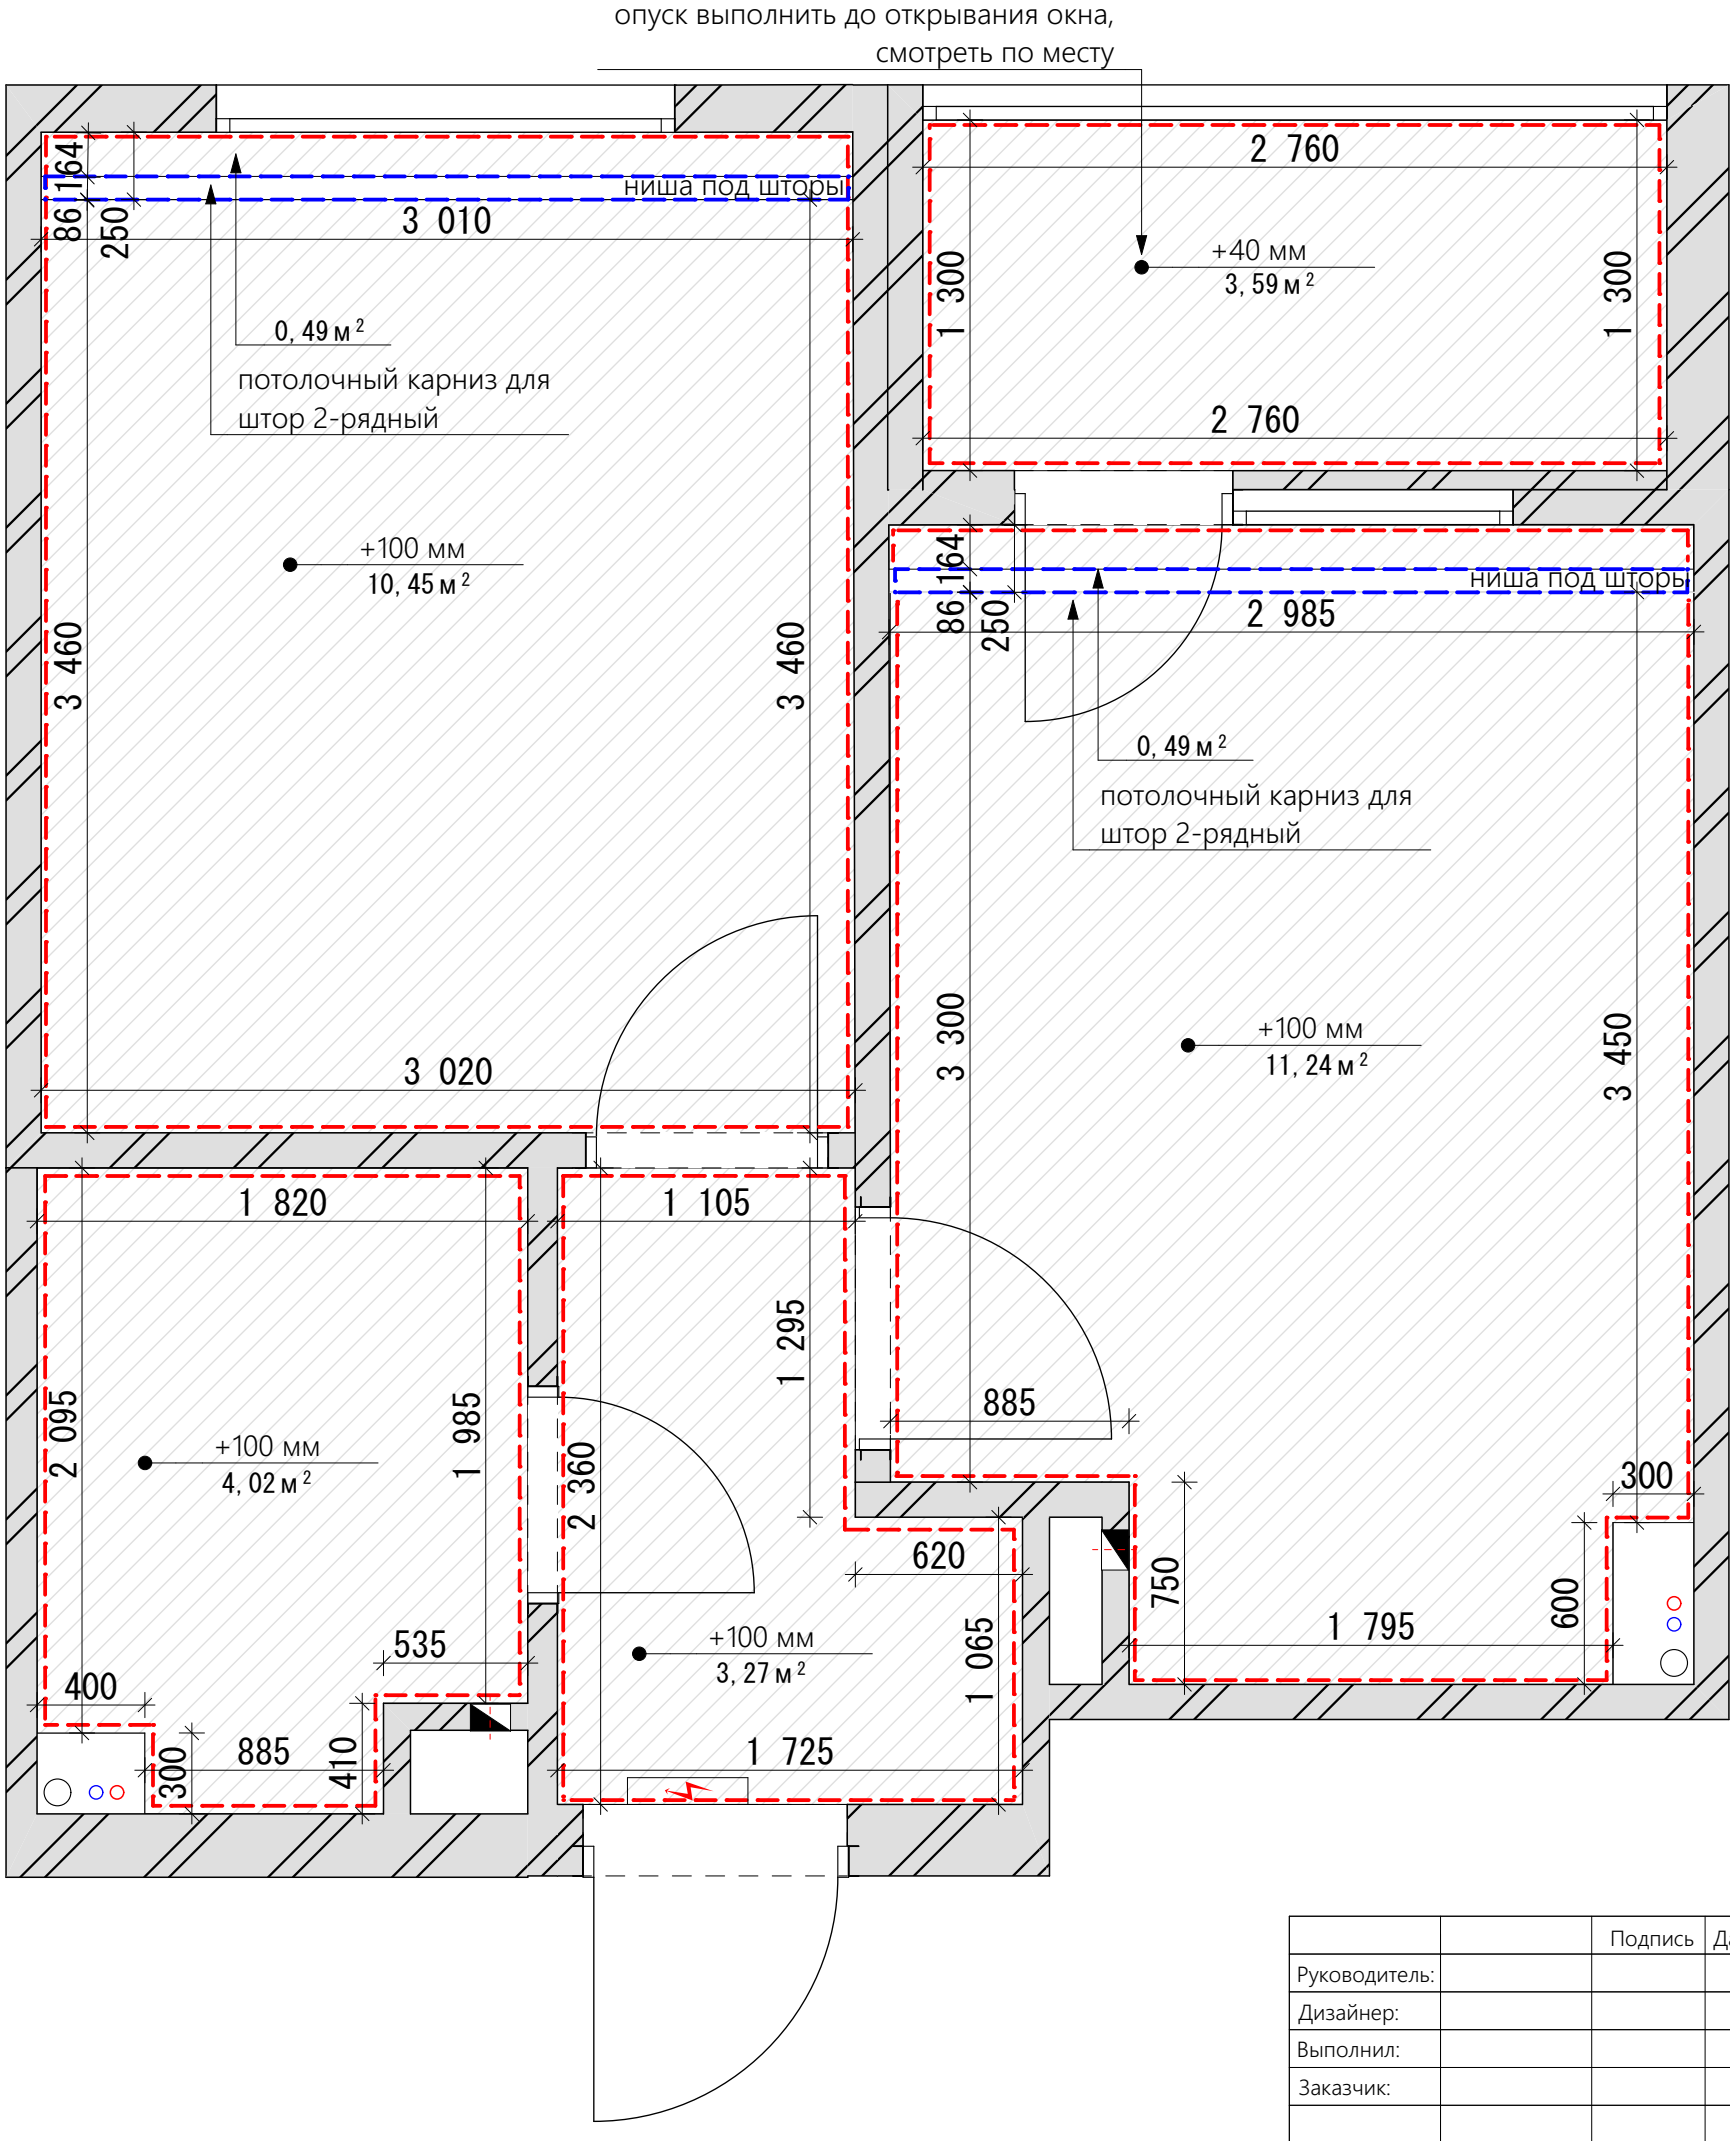

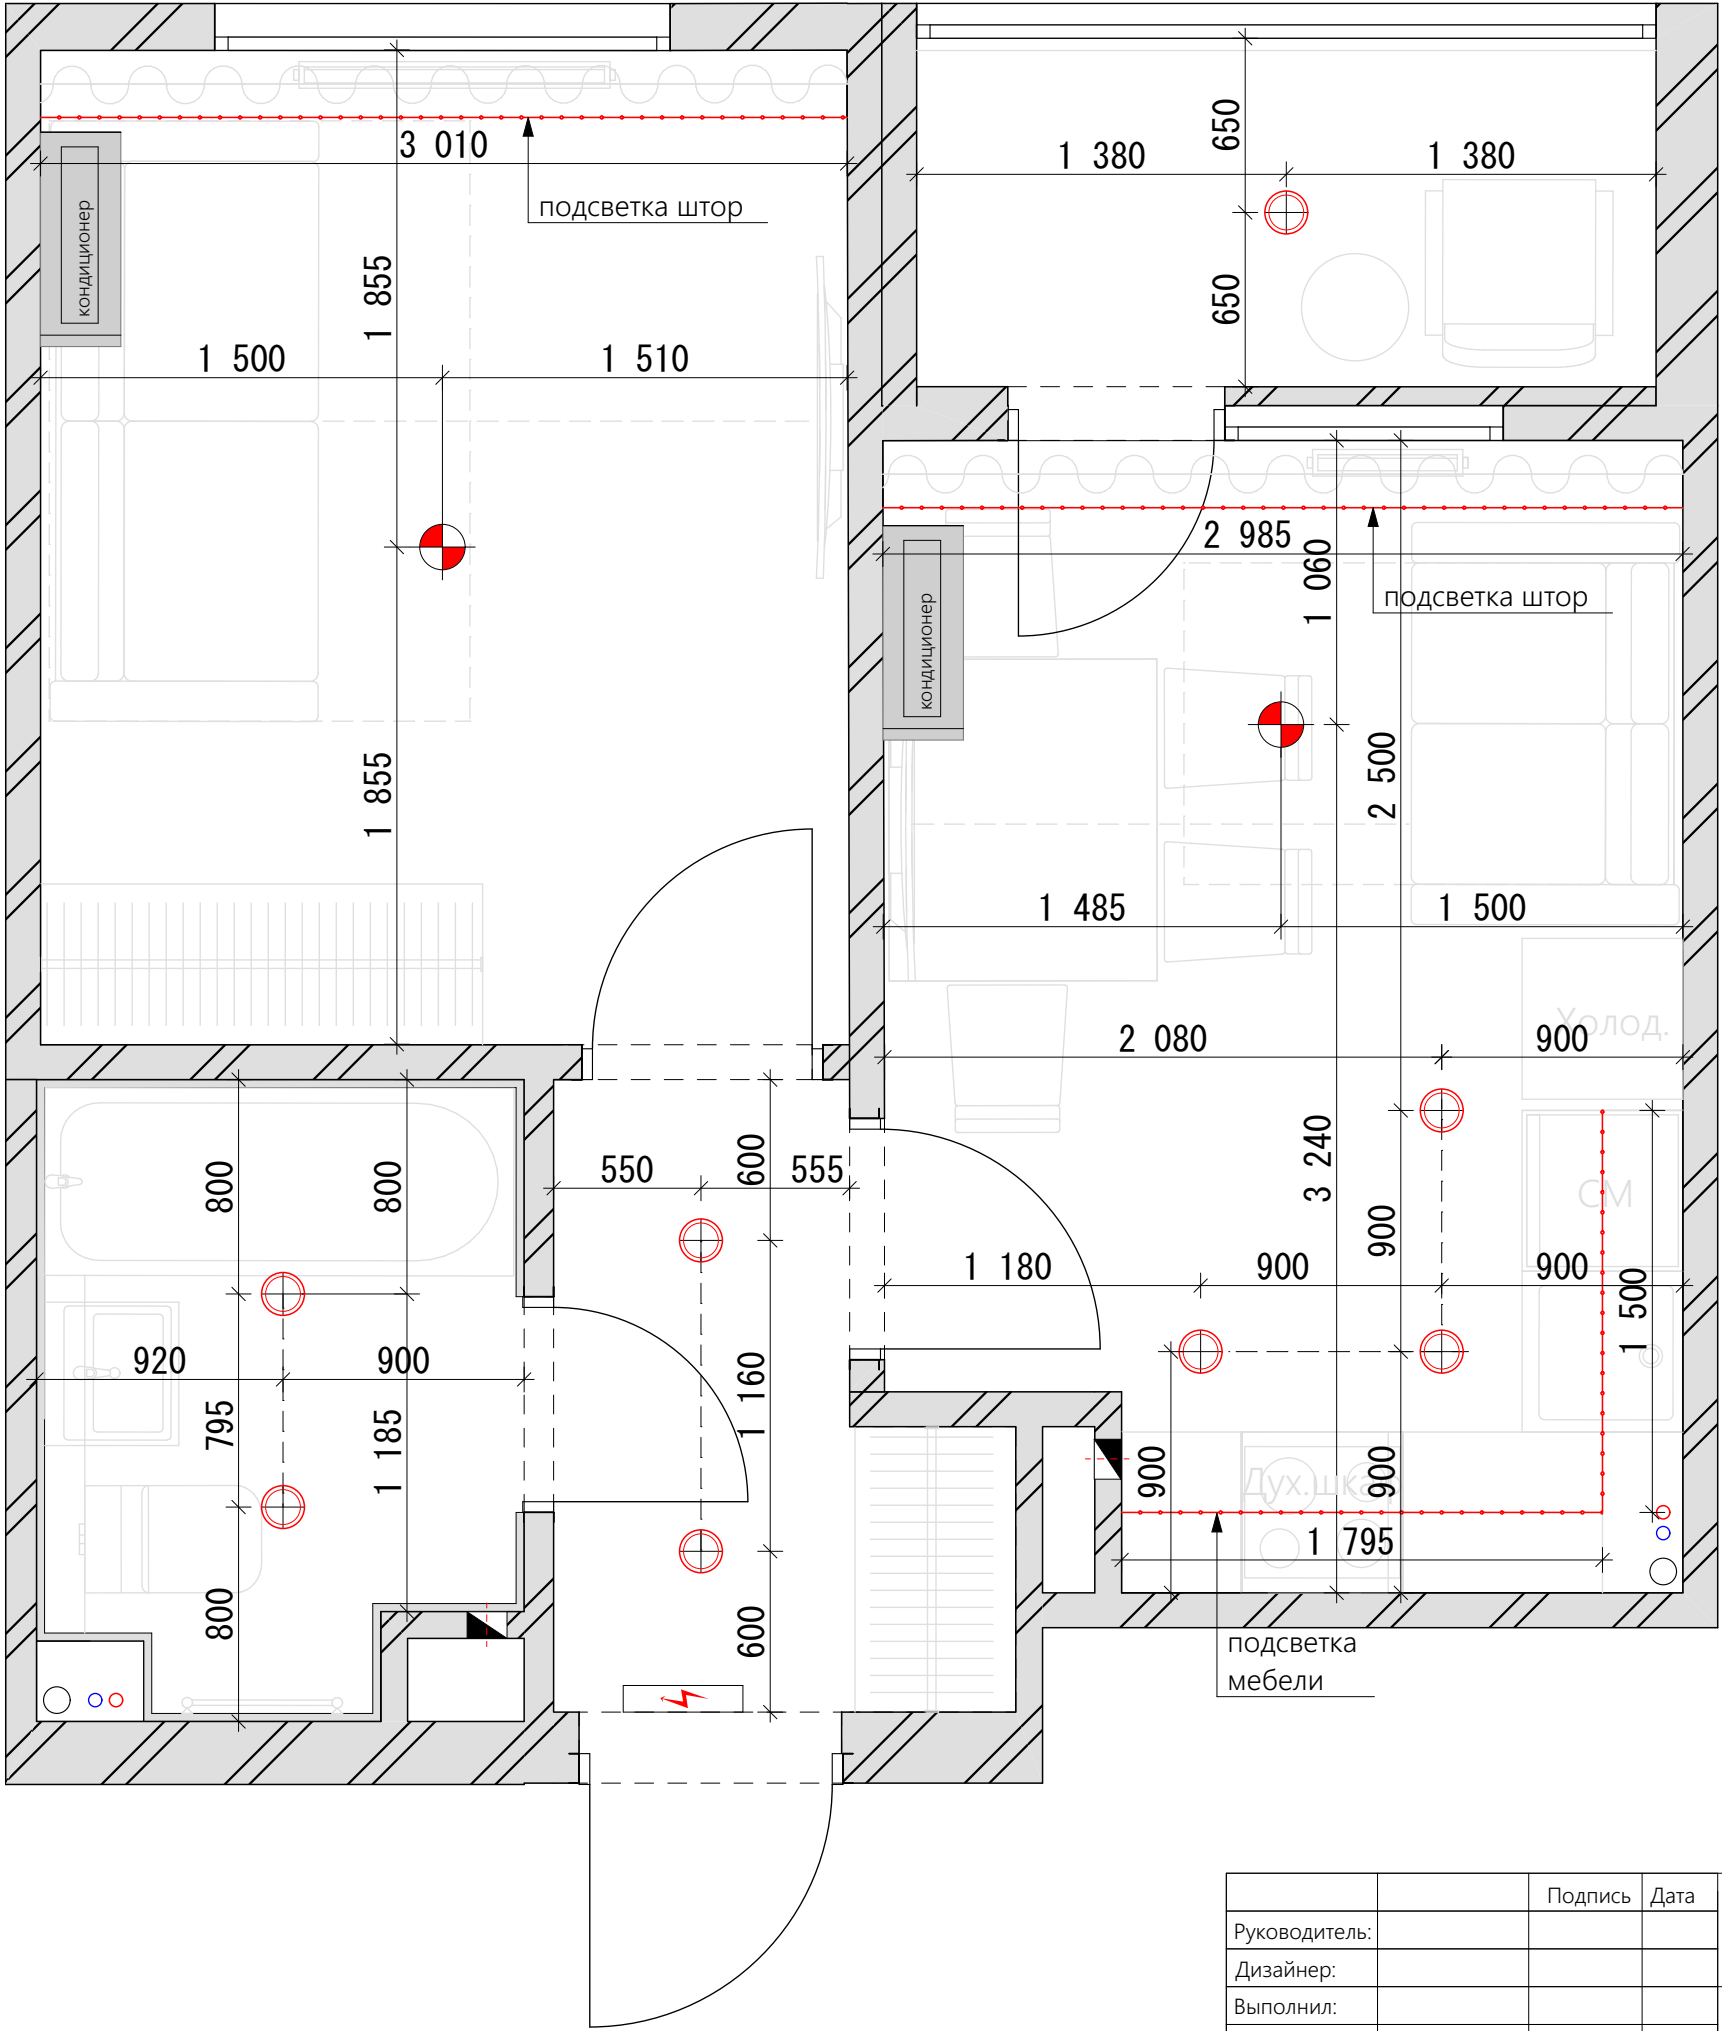


УСЛОВНЫЕ ОБОЗНАЧЕНИЯ

	люстра 2 шт
	встроенный точечный светильник 8 шт
	подсветка 5,99 пог.м

ПРИМЕЧАНИЯ

1. Все размеры указаны в миллиметрах.
2. Лист смотреть совместно с развертками стен.
3. Размеры даны без учета отделочных работ.
4. Расположение осветительного оборудования указано относительно центра светильника.
5. Для электровыводов дать запас.

		Подпись	Дата		Стадия	Лист
Руководитель:					ДП	10
Дизайнер:						
Выполнил:						
Заказчик:						
				План расстановки осветительного оборудования		

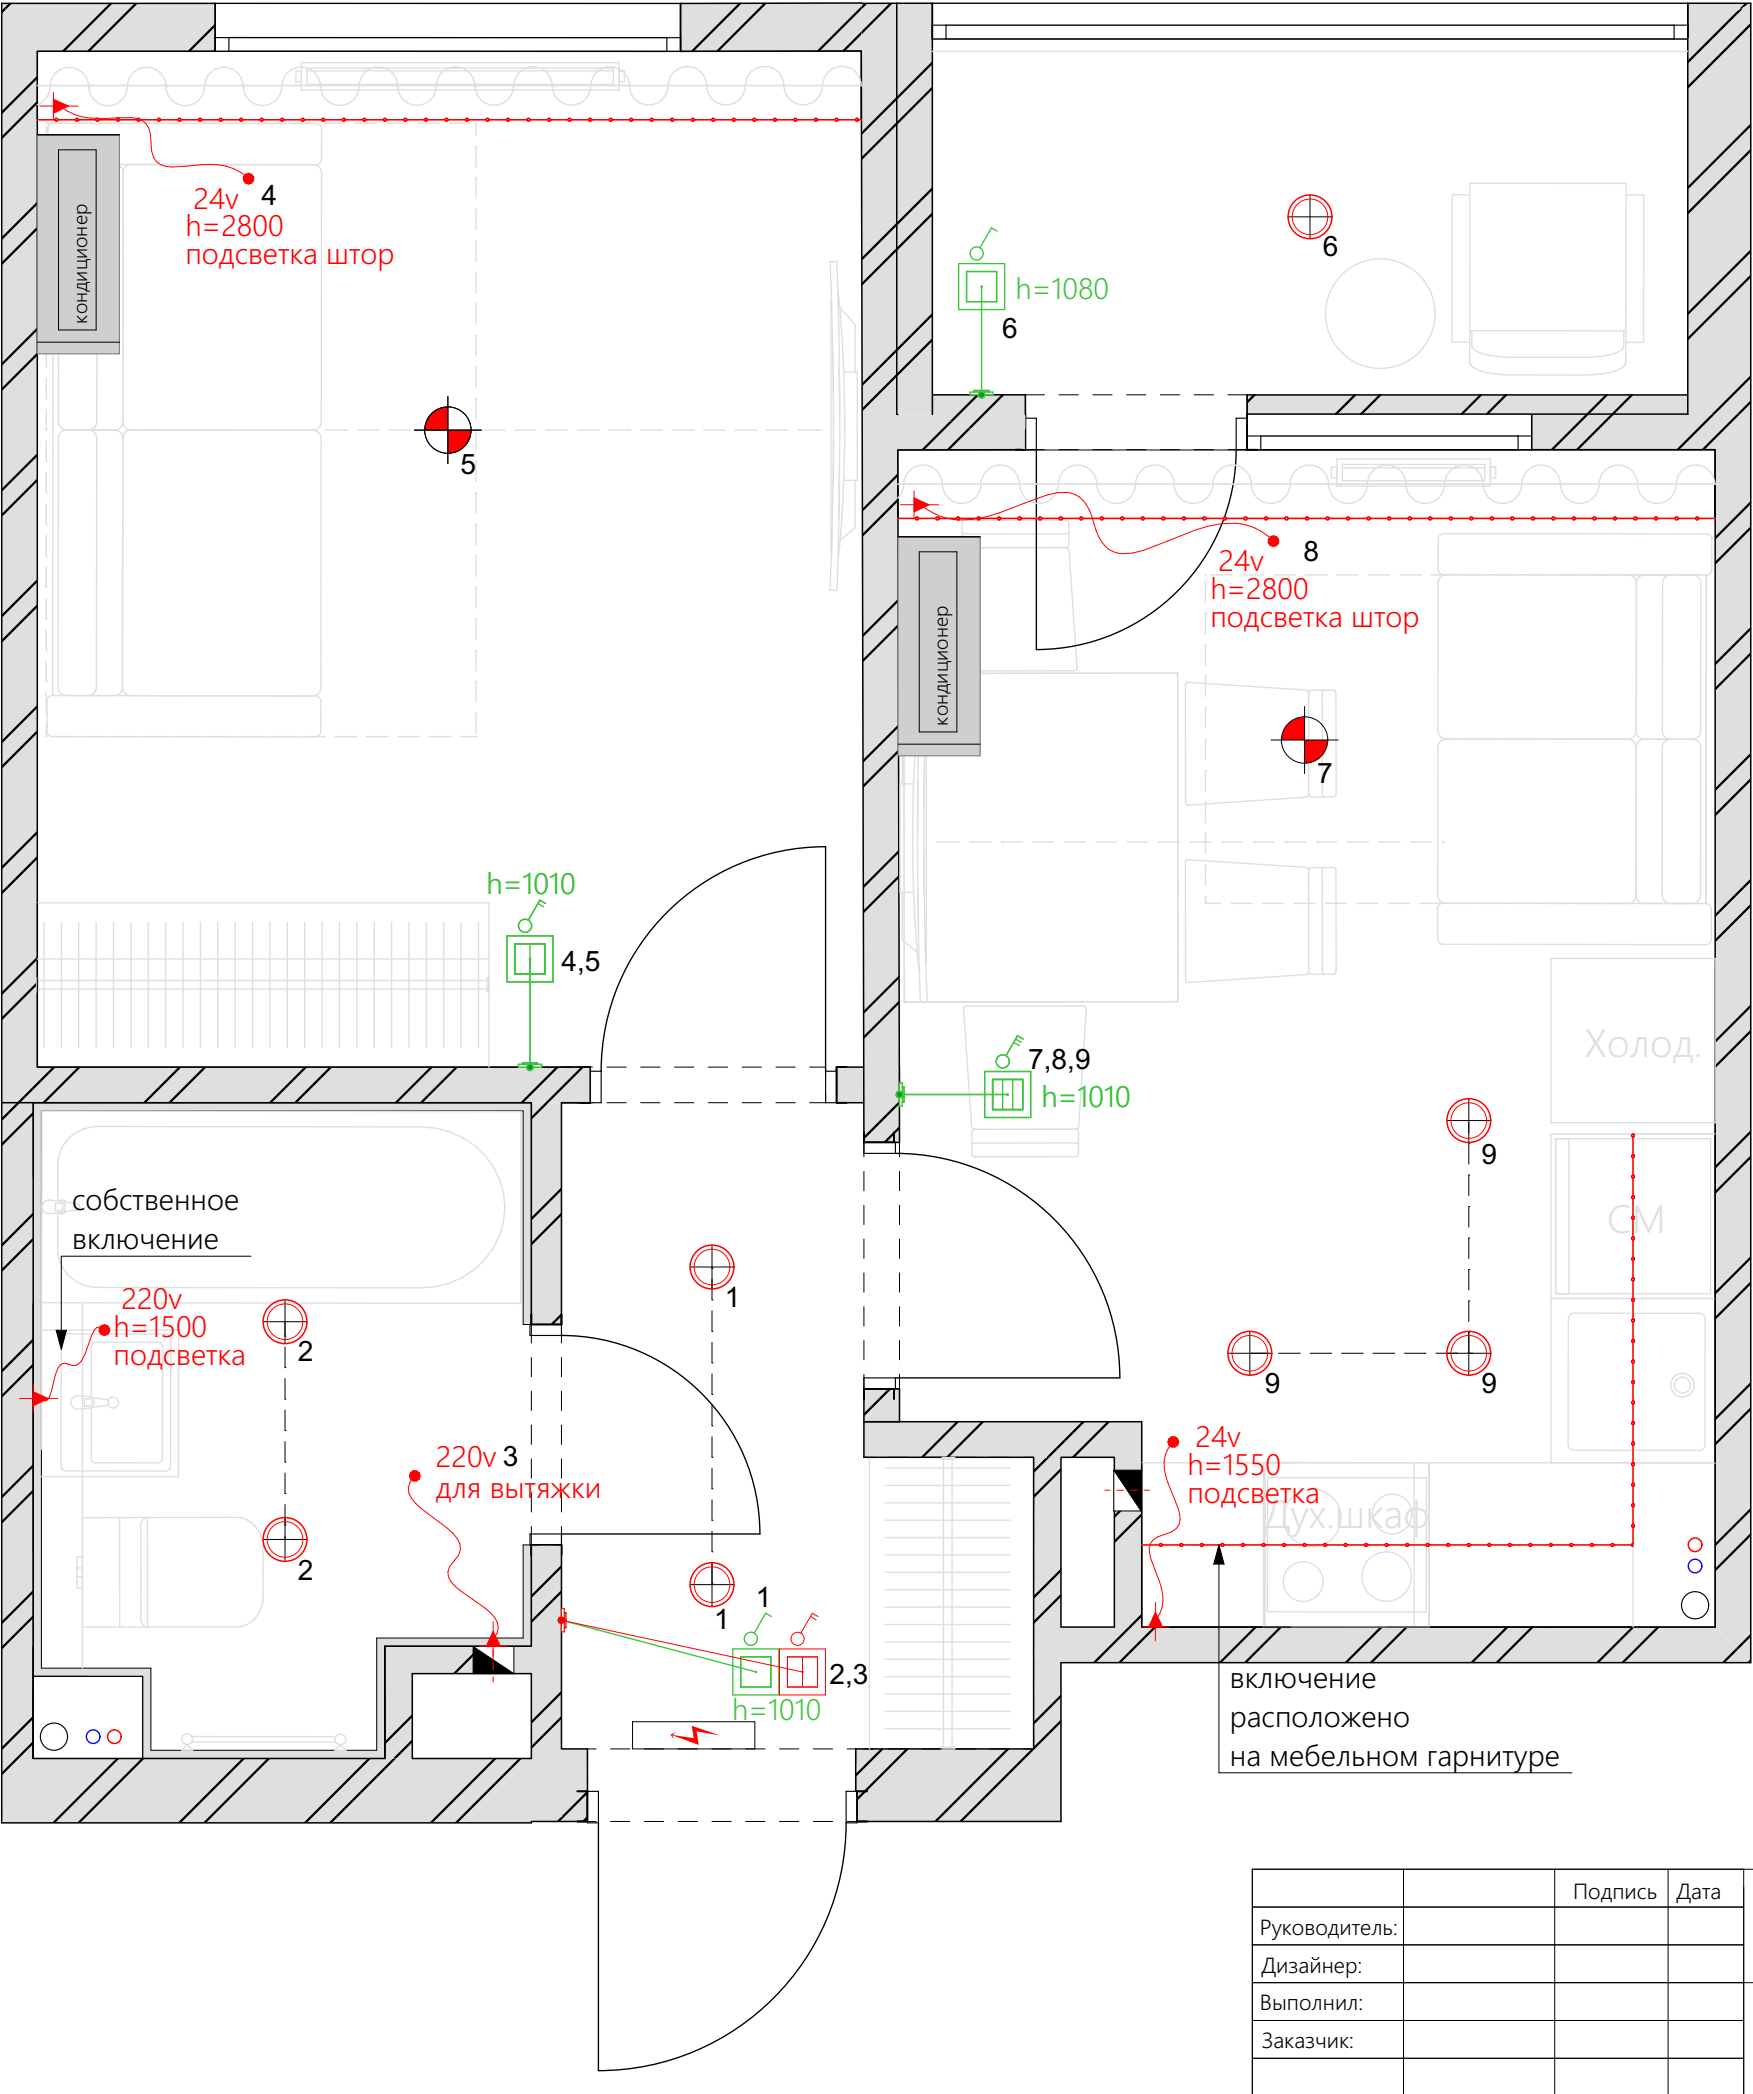


УСЛОВНЫЕ ОБОЗНАЧЕНИЯ	
	1 кл. выключатель 2 шт
	2 кл. выключатель 1 шт
	3 кл. выключатель 1 шт
	2 кл. выключатель 1 шт

ПРИМЕЧАНИЕ

1. Все размеры указаны в миллиметрах.
2. Лист смотреть совместно с развертками стен.
3. Размеры даны без учета отделочных слоев.
4. Расположение розеток и выводов указано относительно центра розетки или группы розеток.
5. Точное расположение розеток и выводов для кухонной техники уточнить при заказе кухни.
6. Распределение автоматов согласовать с заказчиком.

		Подпись	Дата	План управления осветительного оборудования	Стадия	Лист
Руководитель:					ДП	12
Дизайнер:						
Выполнил:						
Заказчик:						

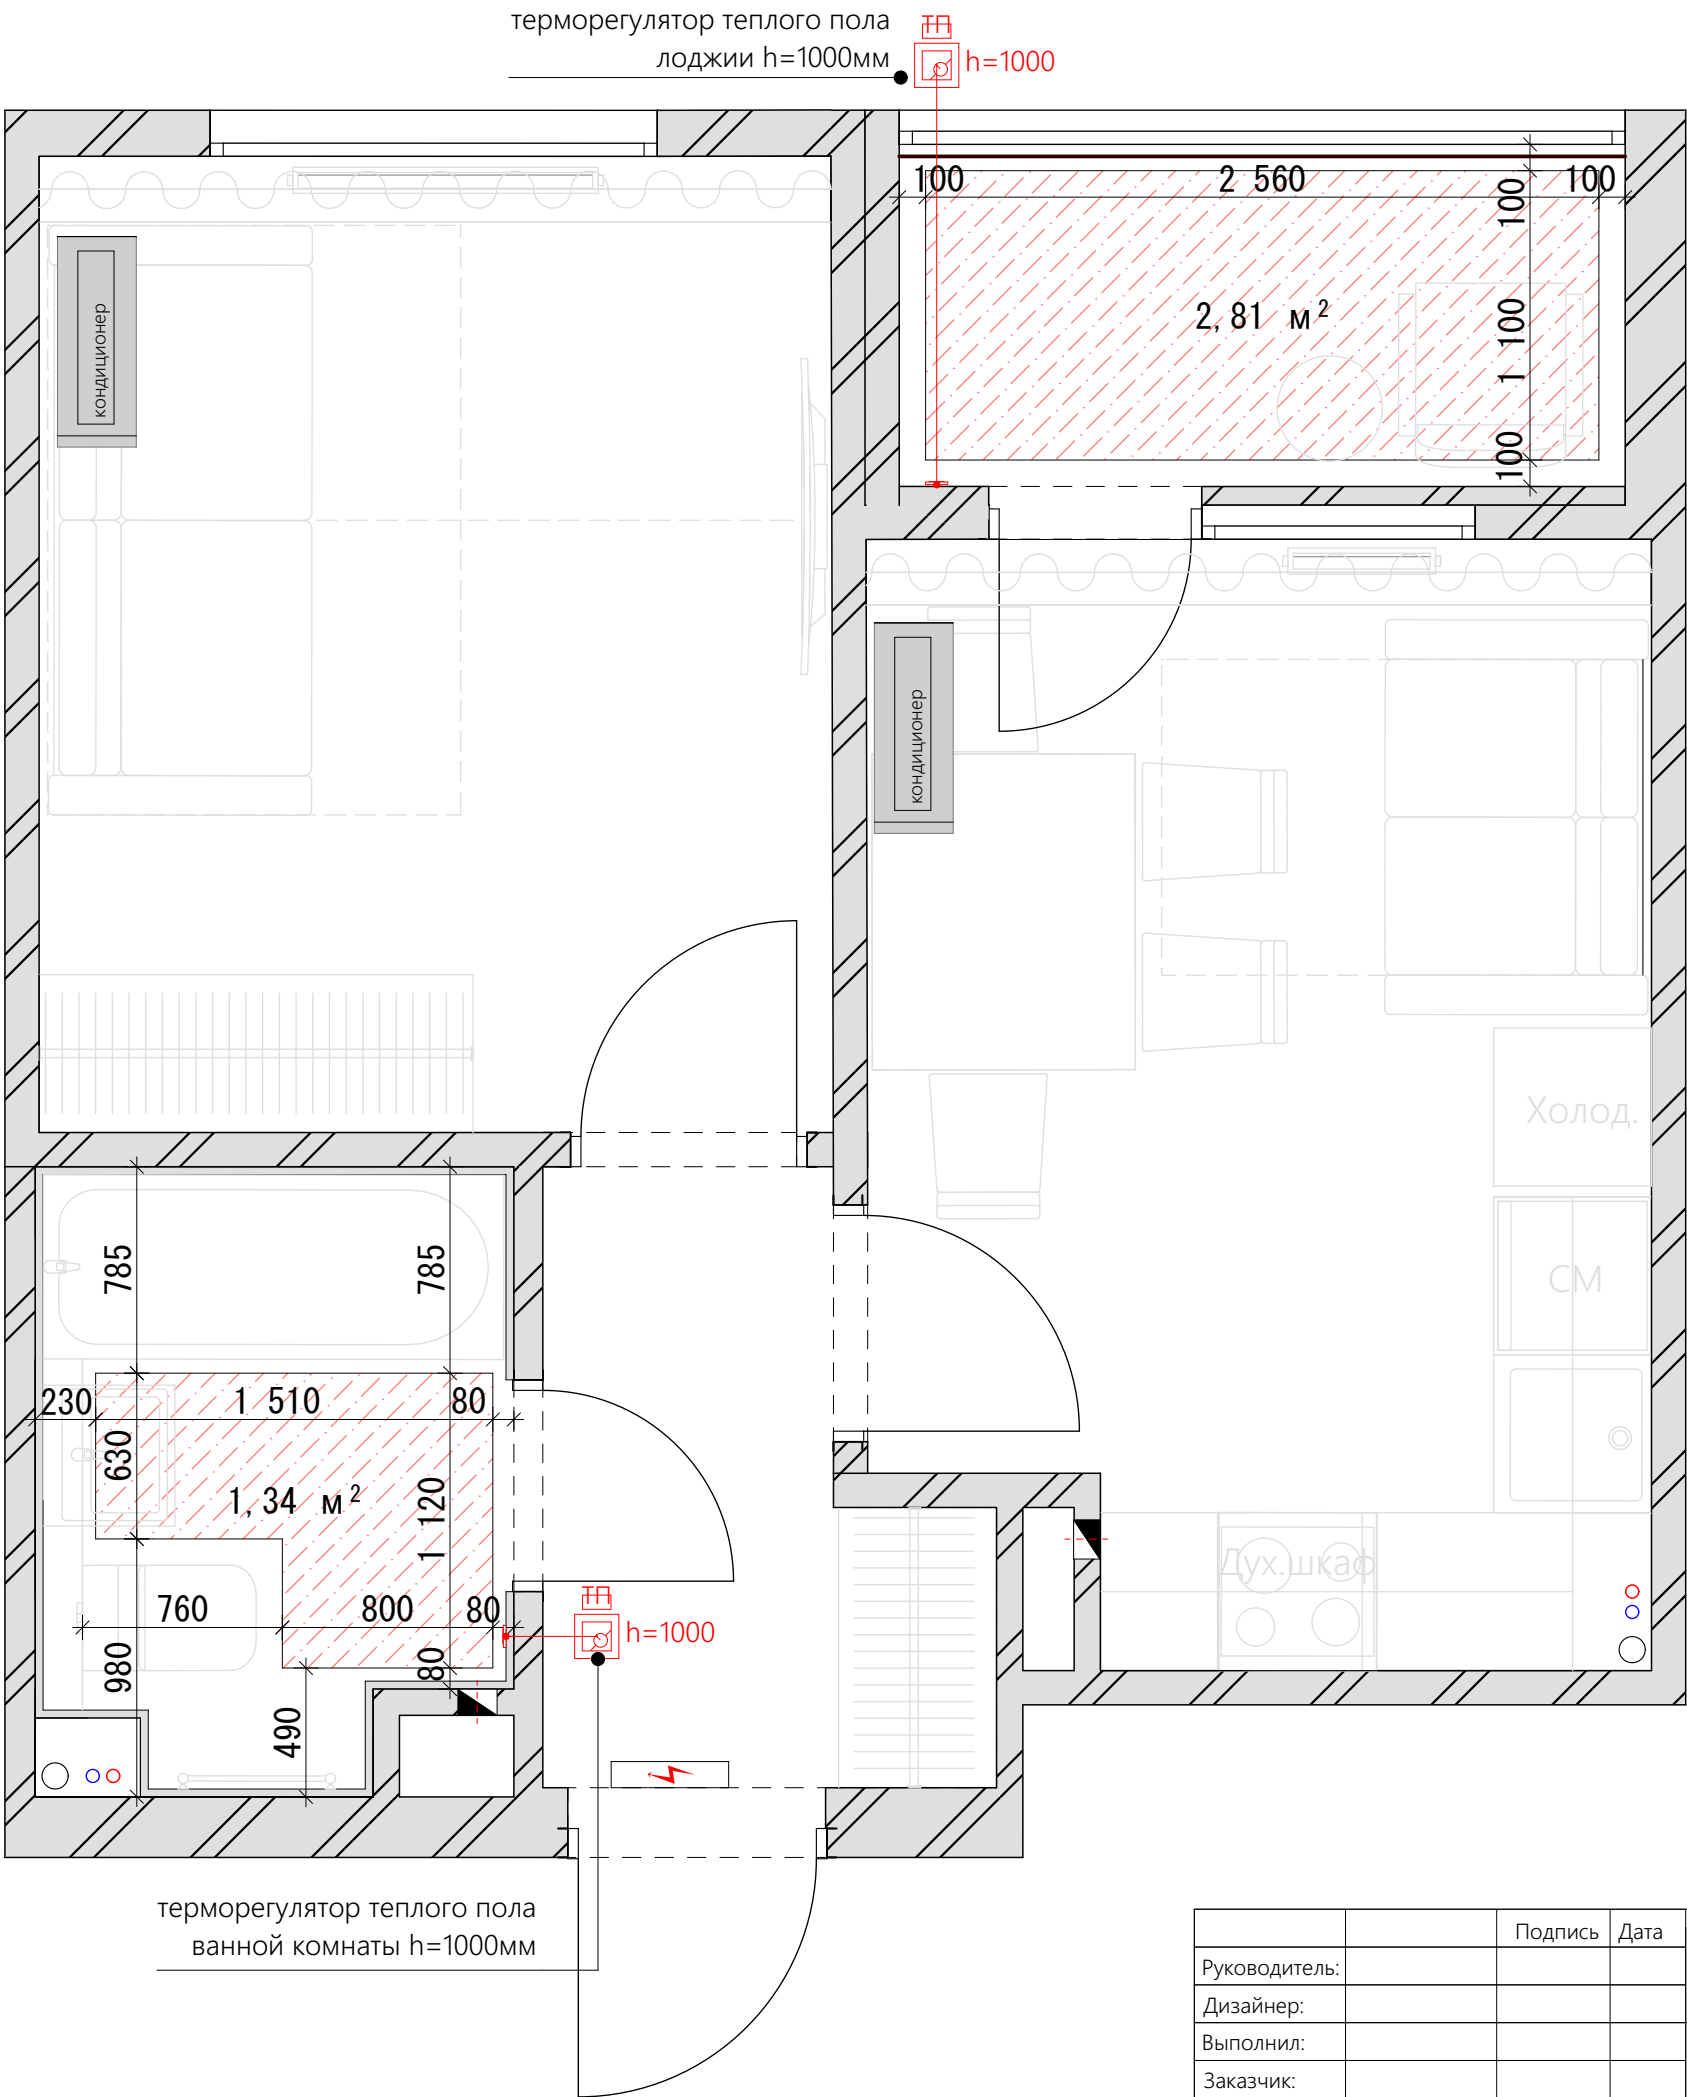


УСЛОВНЫЕ ОБОЗНАЧЕНИЯ

	датчик теплого пола = 2 шт
	теплый пол S=4,15 м²

ПРИМЕЧАНИЕ

1. Все размеры указаны в миллиметрах.
2. При приобретении напольных покрытий и систем теплого пола уточнить у поставщиков их совместимость.
3. Теплый пол монтируется с отступом от мебели 100 мм.

		Подпись	Дата		Стадия	Лист
Руководитель:					ДП	13
Дизайнер:						
Выполнил:						
Заказчик:						
				План привязки теплого пола		

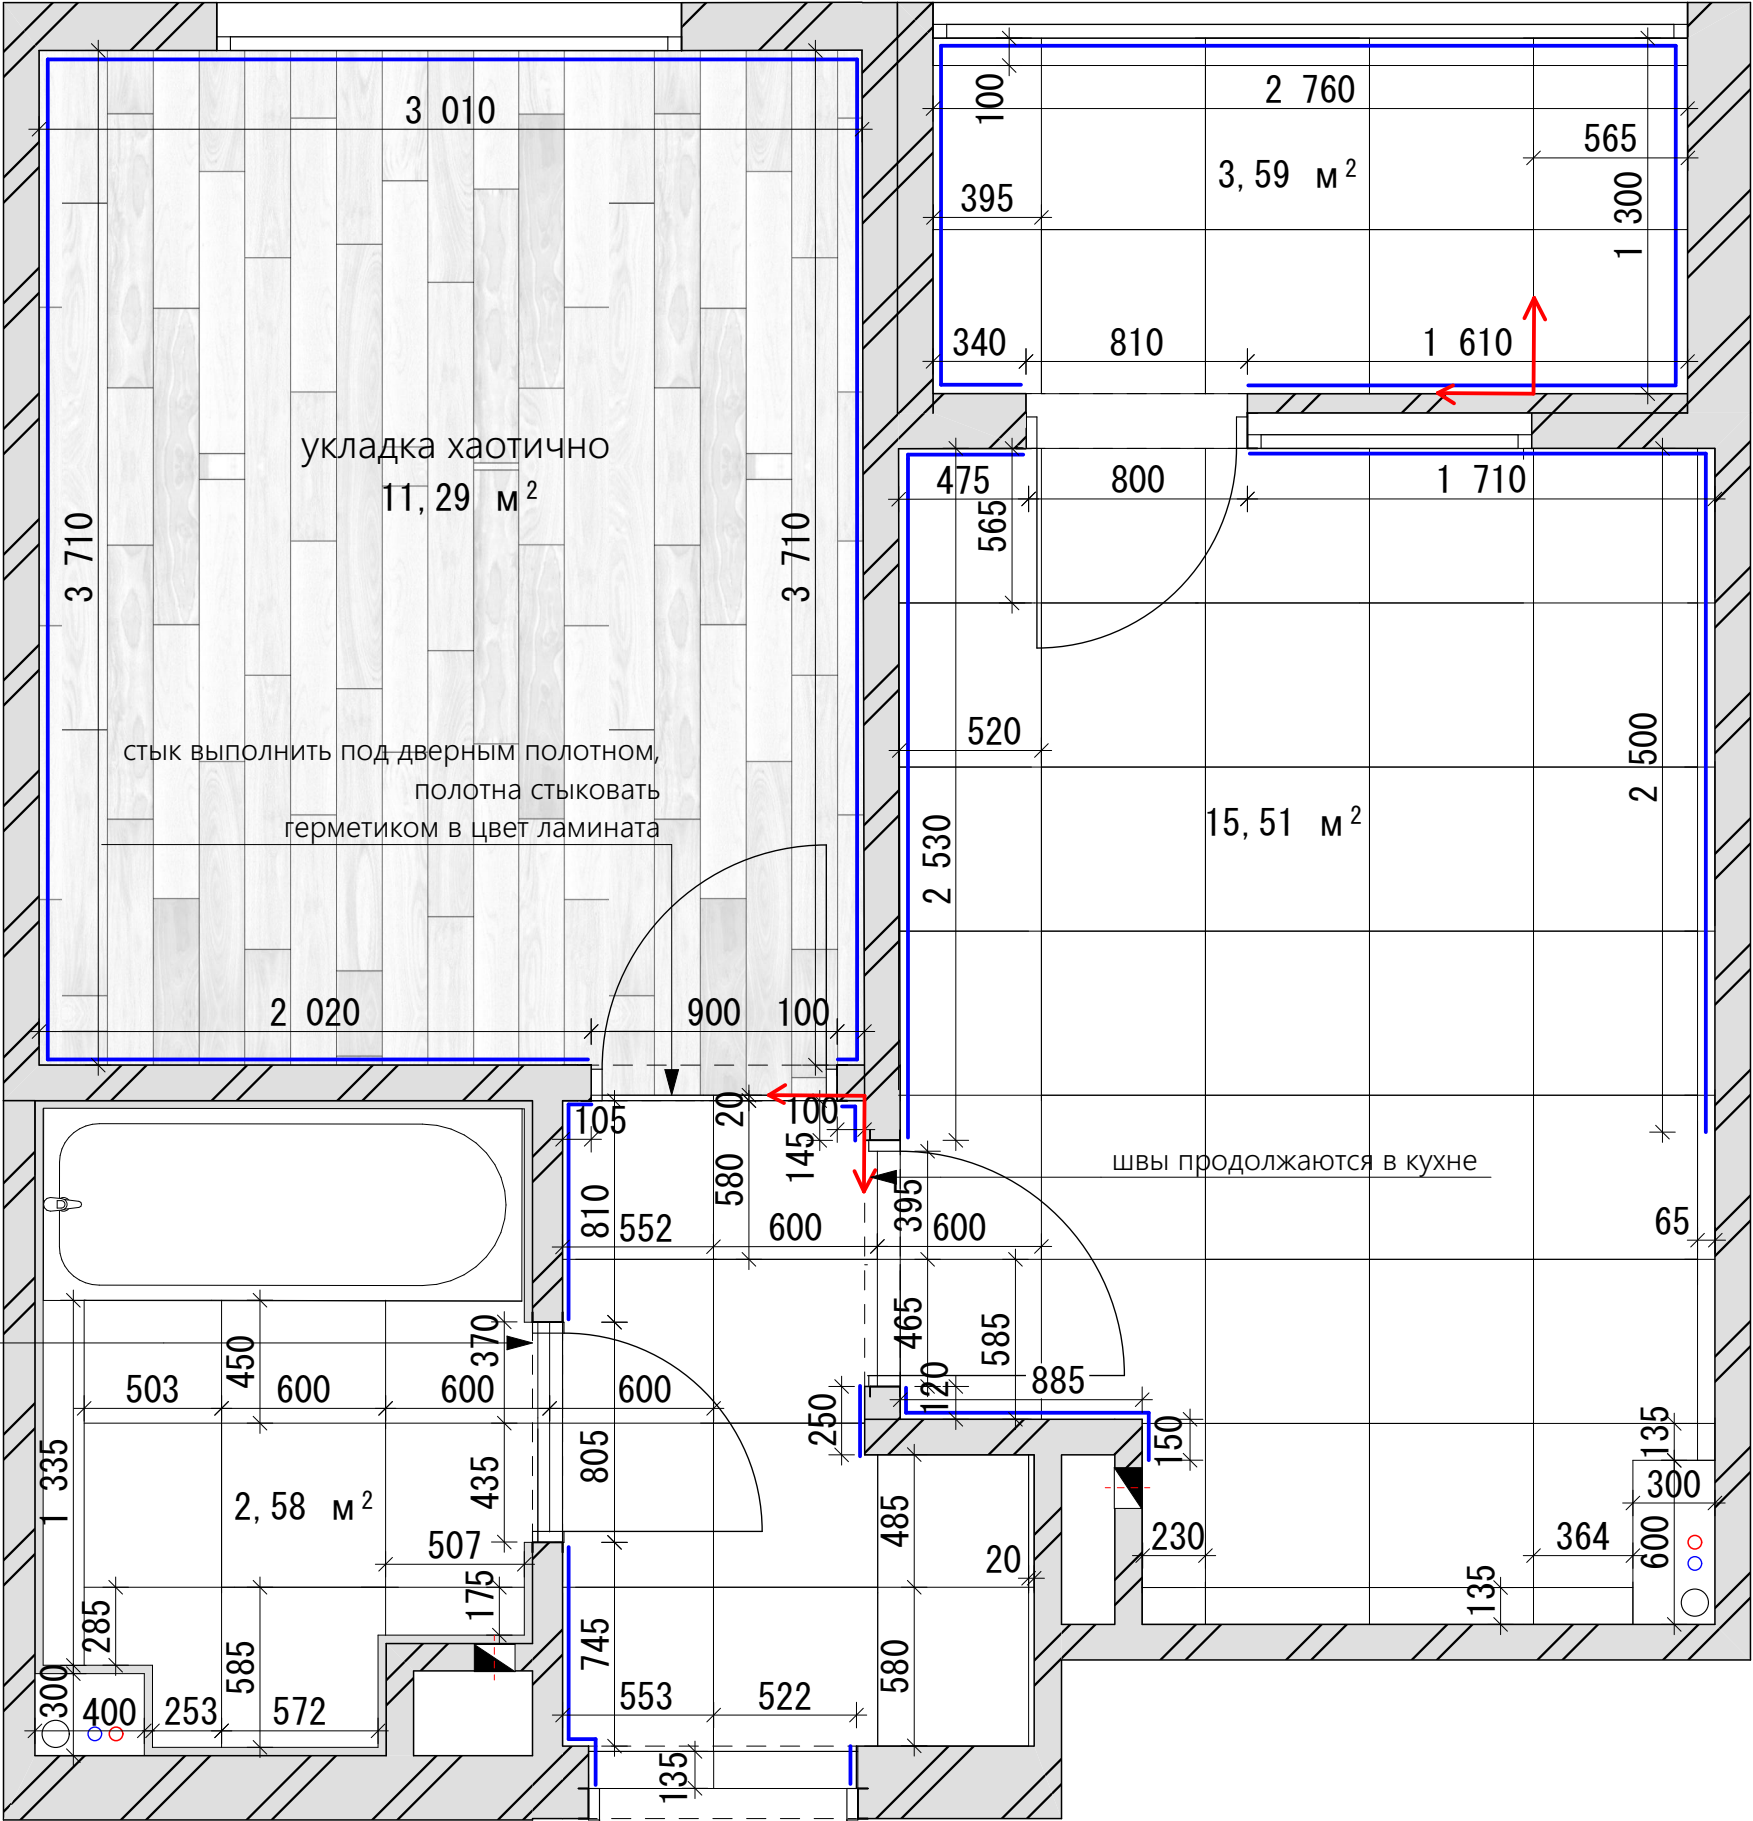

УСЛОВНЫЕ ОБОЗНАЧЕНИЯ		
Вид на плане	Наименование	Кол-во
	Ламинат - толщину уточнить при заказе материалов	11,29м² без запаса
	Керамогранит 600х600 - толщину уточнить при заказе материалов	21,68м² без запаса
	Плинтус, уточнить у заказчика	31,32 пог.м без запаса
	Начало раскладки	

ПРИМЕЧАНИЯ




1. Все размеры указаны в миллиметрах.
2. Лист смотреть совместно с развертками стен.
3. Размеры даны без учета отделочных слоев.
4. Все площади посчитаны без запаса.
5. Направление укладки пола и все размеры уточняются после окончания общестроительных работ.
6. Границы технологического разрыва уточнить, монтаж производить после согласования с заказчиком.
7. Уровень полов санузла довести до уровня чистового пола во всех помещениях.

швы продолжают
в ванной комнате

швы продолжают в кухне

		Подпись	Дата	План раскладки напольных покрытий	Стадия	Лист
Руководитель:					ДП	14
Дизайнер:						
Выполнил:						
Заказчик:						

Развертка кухонной мебели

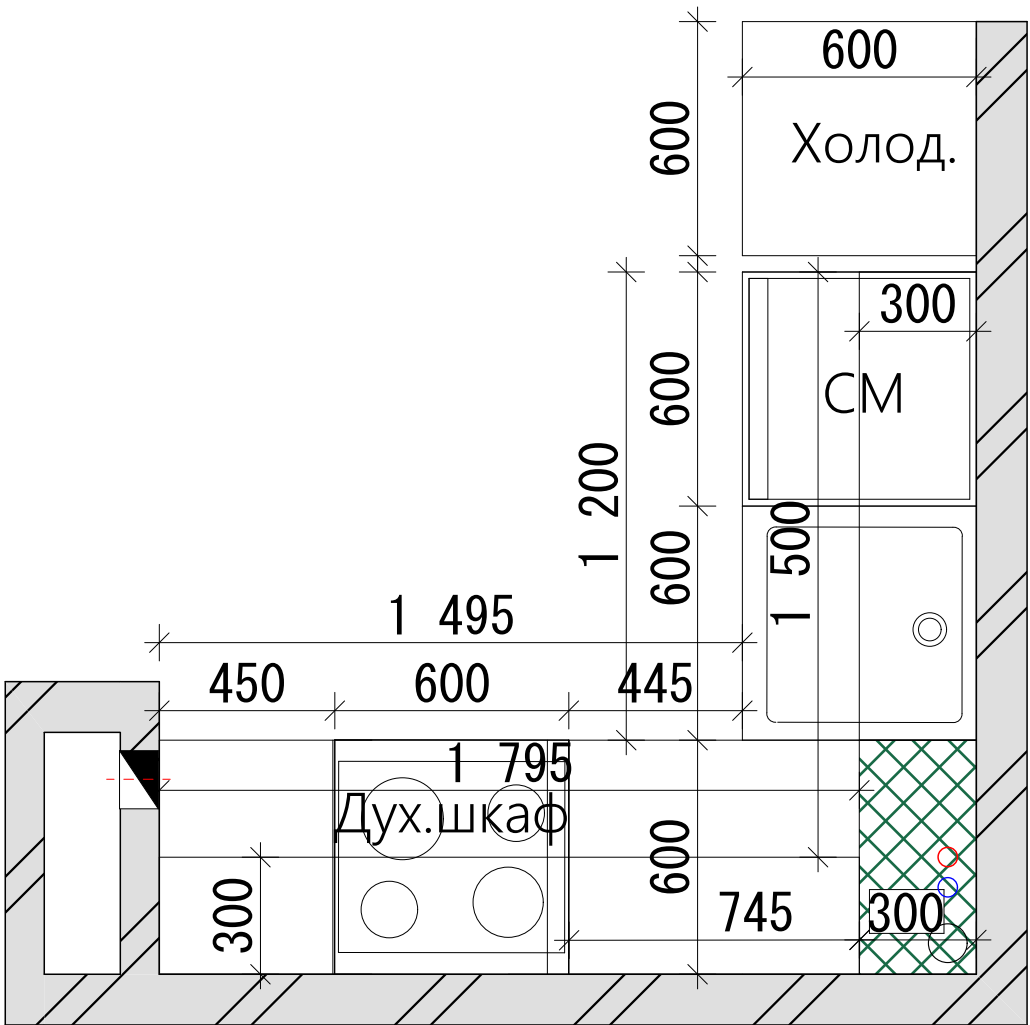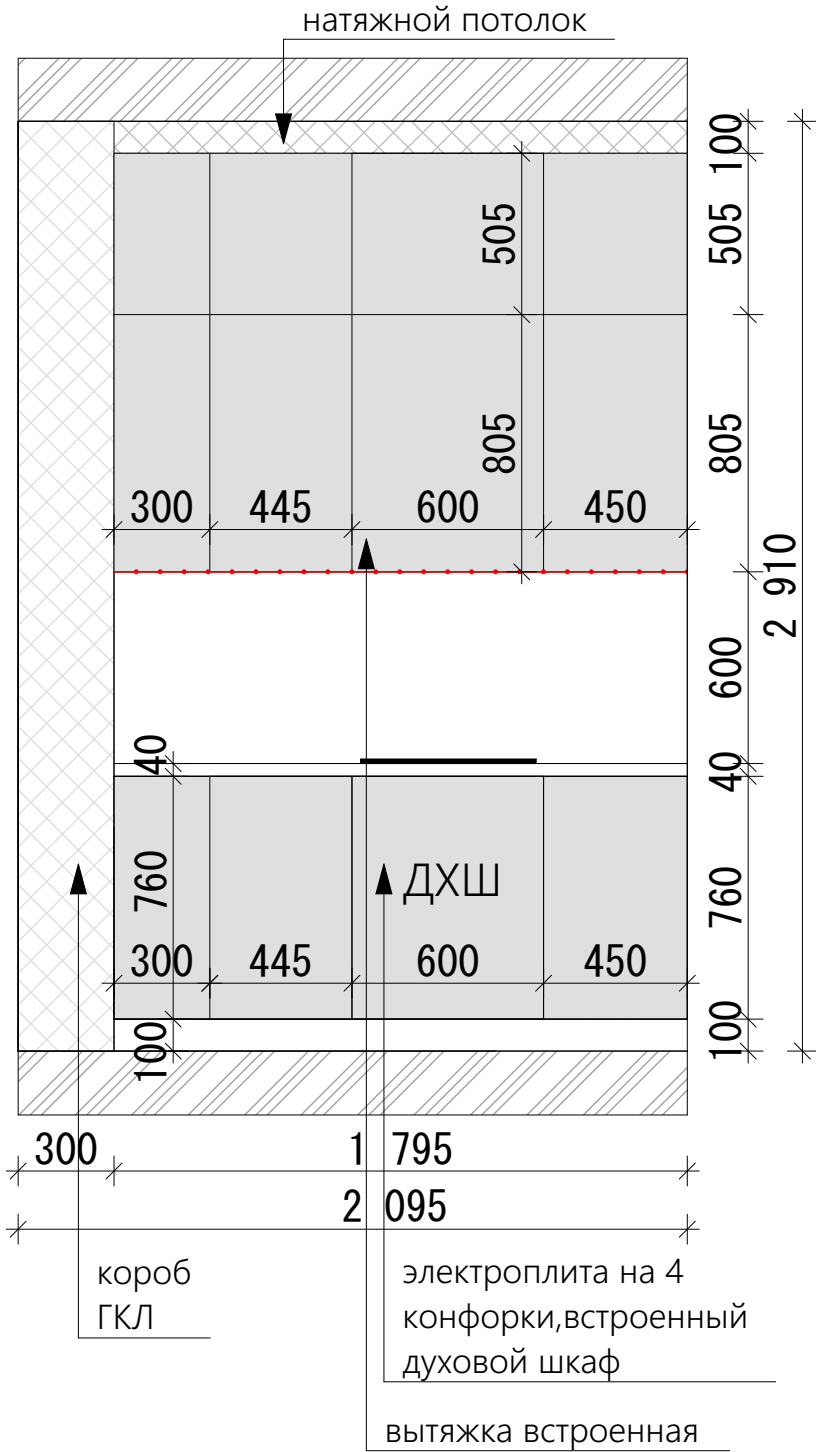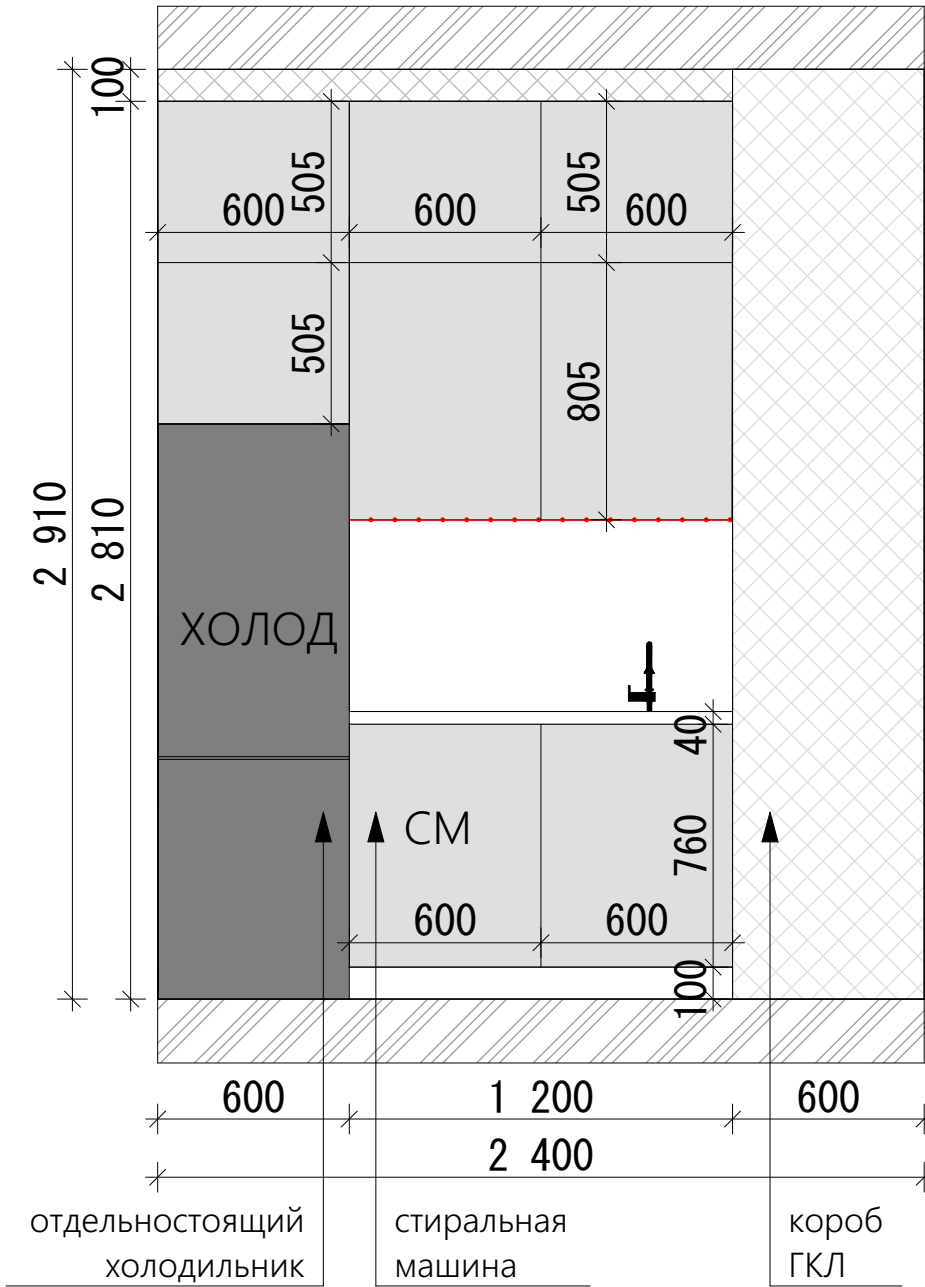

		Подпись	Дата		Стадия	Лист
Руководитель:					ДП	15
Дизайнер:						
Выполнил:						
Заказчик:						
				Развертка кухонной мебели		