



ДИЗАЙН ИНТЕРЬЕРА
ПРОСТРАНСТВО ДЛЯ ЖИЗНИ

МАКСИМАЛЬНЫЙ ПРОЕКТ

АЛЬБОМ ЧЕРТЕЖЕЙ,
ВИЗУАЛИЗАЦИЙ
И СПЕЦИФИКАЦИЙ



Технические чертежи и планы



Фотореалистичные визуализации



Подбор отделочных материалов



Подбор мебели и декора



Подбор освещения



Подбор сантехники



Рекомендации и спецификации

ДАТА: _____




ПРОДУМАННЫЙ ДИЗАЙН
ДЛЯ КОМФОРТНОЙ ЖИЗНИ
ОТ ИДЕИ ДО РЕАЛИЗАЦИИ

Ведомость рабочих чертежей

Имя листа	№ листа	Имя листа	№ листа
Титульный лист	01	План расположения розеток и выключателей	15
Ведомость рабочих чертежей	02	План управления осветительным оборудованием	16
Обмерочный чертёж	03	План раскладки напольных покрытий	17
План демонтажа	04	Развёртки стен Прихожая	18
План монтажа	05	Развёртки стен Гостиная	19
Схемы монтажа	06	Развёртки стен Кухня	20
План перепланировки	07	Развёртки стен Спальня	21
План расстановки мебели и оборудования	08	Развёртки стен Постирочная	22
План формирования дверных проёмов	09	Визуализации Прихожая	23-24
Общий план расстановки сантехнических приборов	10	Визуализации Гостиная	25-26
План технических карт сантехнических приборов	11	Визуализации Кухня	27-28
Развёртки стен Санузел	12	Визуализации Спальня	29-31
План потолка	13	Визуализации Постирочная	32
План расстановки осветительного оборудования	14	Визуализации Санузел	33-34

		Подпись	Дата		Стадия	Лист	Масштаб
Руководитель					ДП	02	
Дизайнер							
Выполнил							
Заказчик				Ведомость рабочих чертежей			

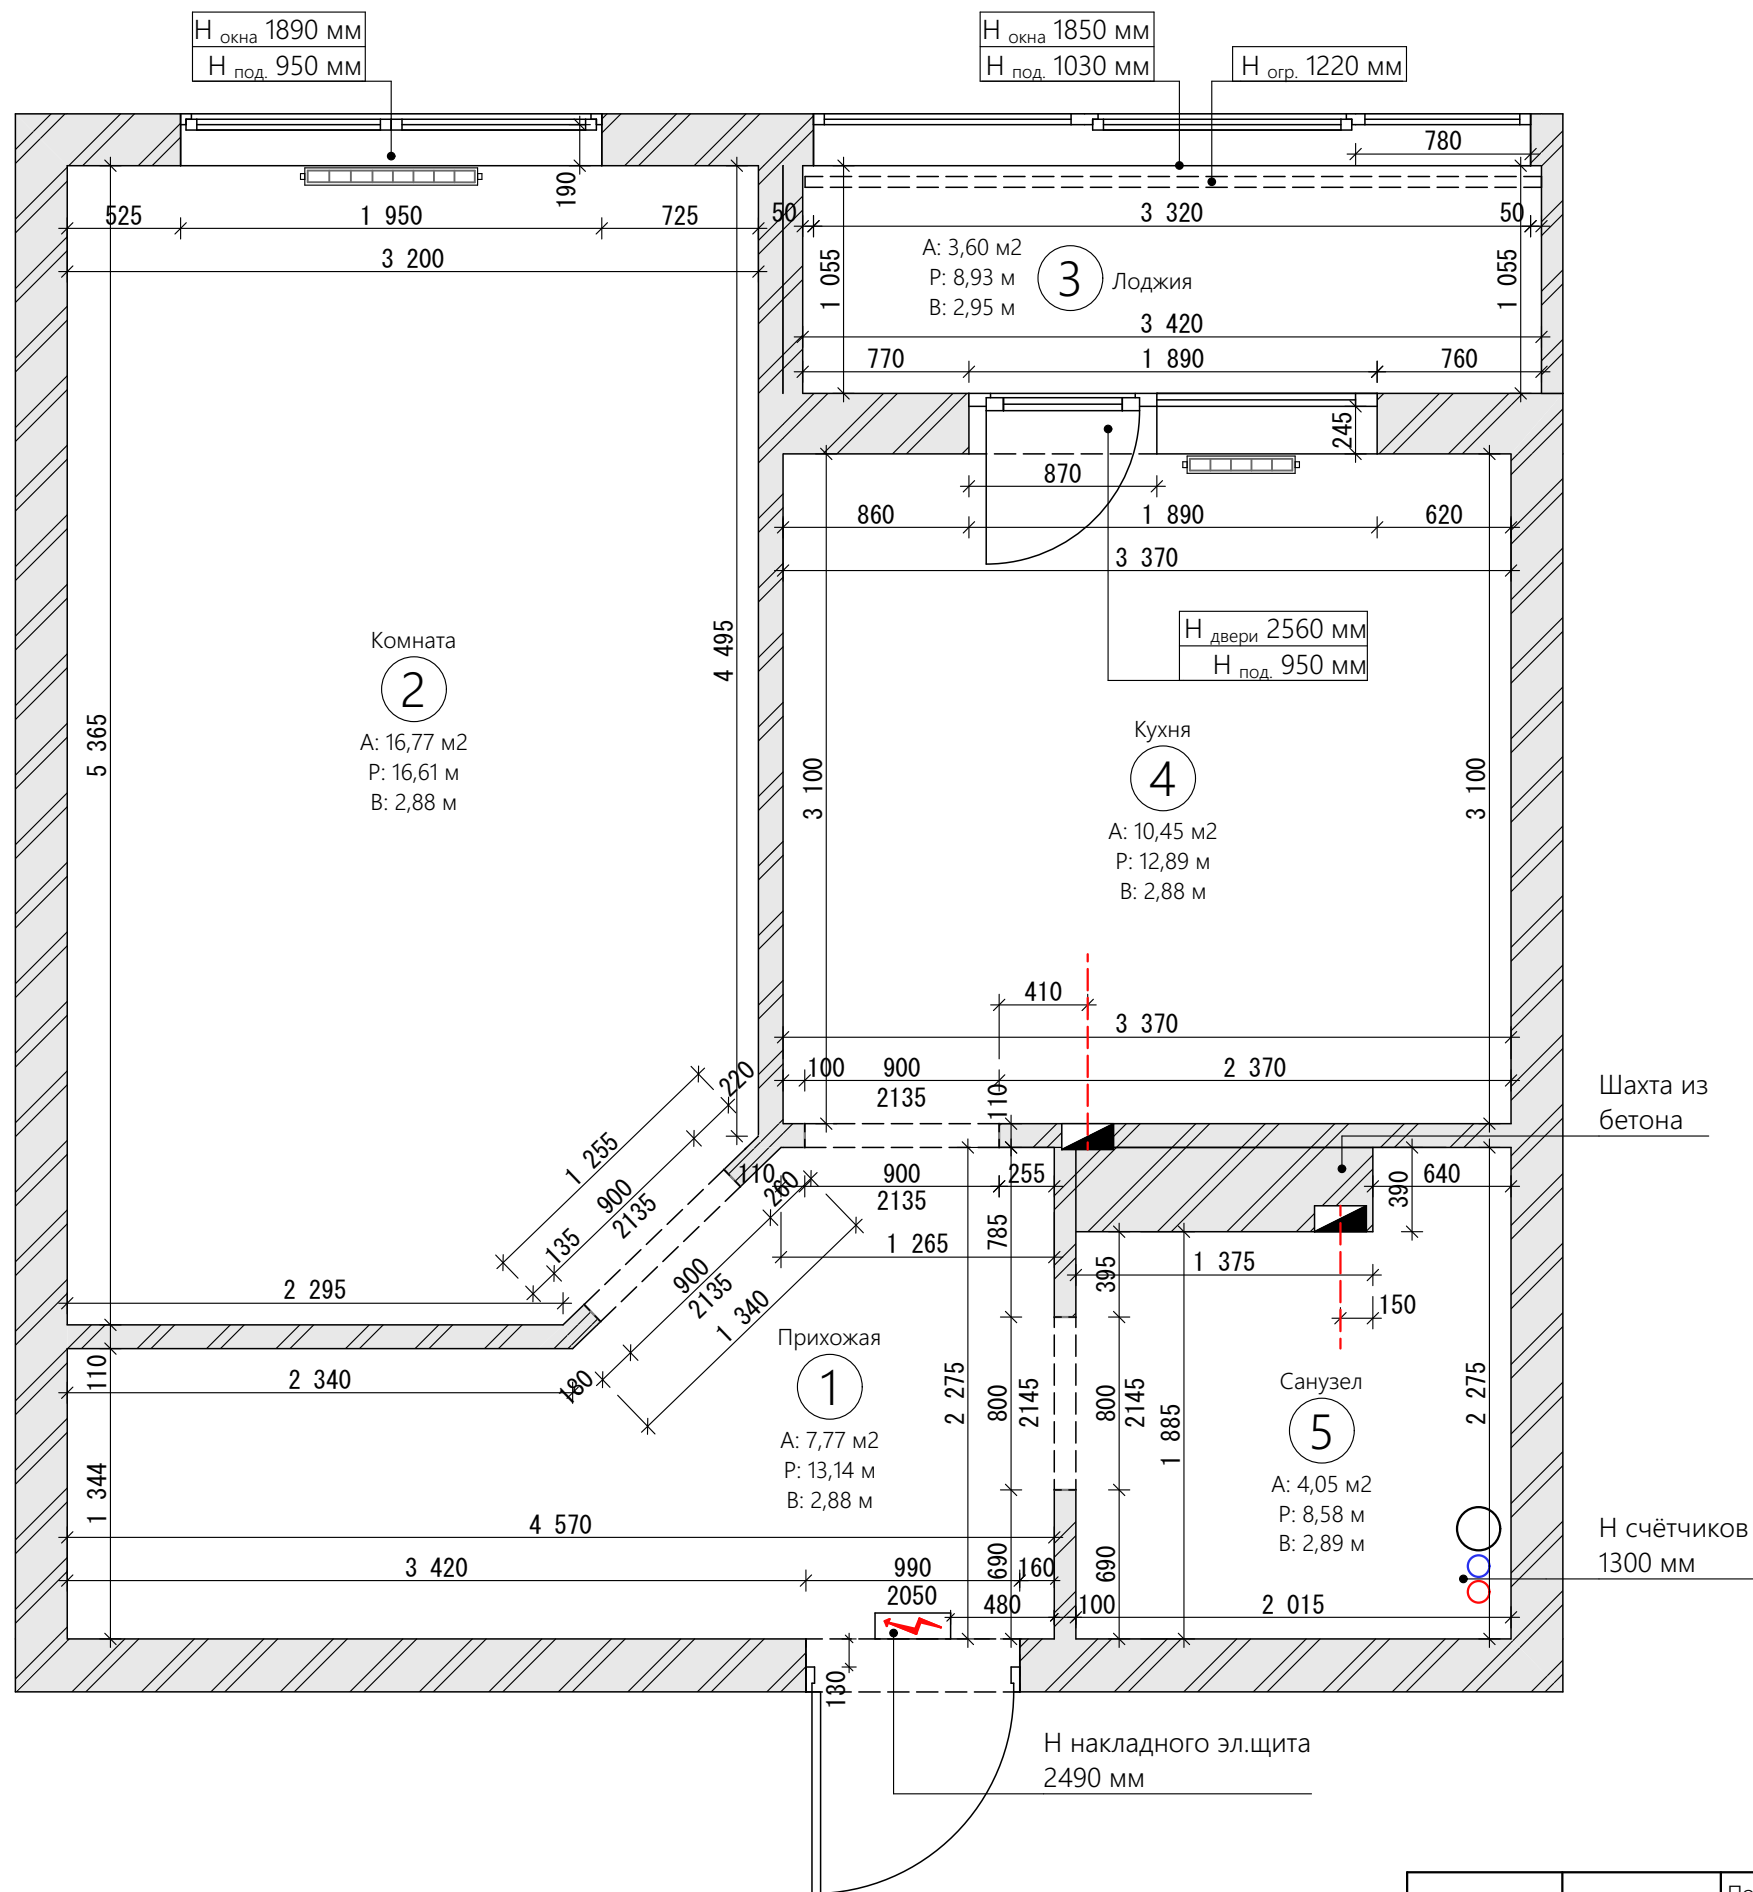

УСЛОВНЫЕ ОБОЗНАЧЕНИЯ:


	стены существующие
	электрощит
	водопровод канализация
	проём для вентиляции
	радиатор
А - площадь; Р - периметр; В - высота	

ЭКСПЛИКАЦИЯ ПОМЕЩЕНИЙ		
№	Наименование помещения	Площадь м²
1	Прихожая	7,77
2	Комната	16,77
3	Лоджия	3,60
4	Кухня	10,45
5	Санузел	4,05
Общая площадь = 42,64 м²		

ПРИМЕЧАНИЯ:

1. Все размеры указаны в миллиметрах.
2. Все размеры проверить по месту, возможны погрешности.
3. Размеры даны без учёта отделочных слоёв.
4. Стены в прихожей, кухне, комнате и лоджии оштукатурены от застройщика.

		Подпись	Дата		Стадия	Лист	Масштаб
Руководитель					ДП	03	1:35
Дизайнер					Обмерочный чертёж		
Выполнил							
Заказчик							

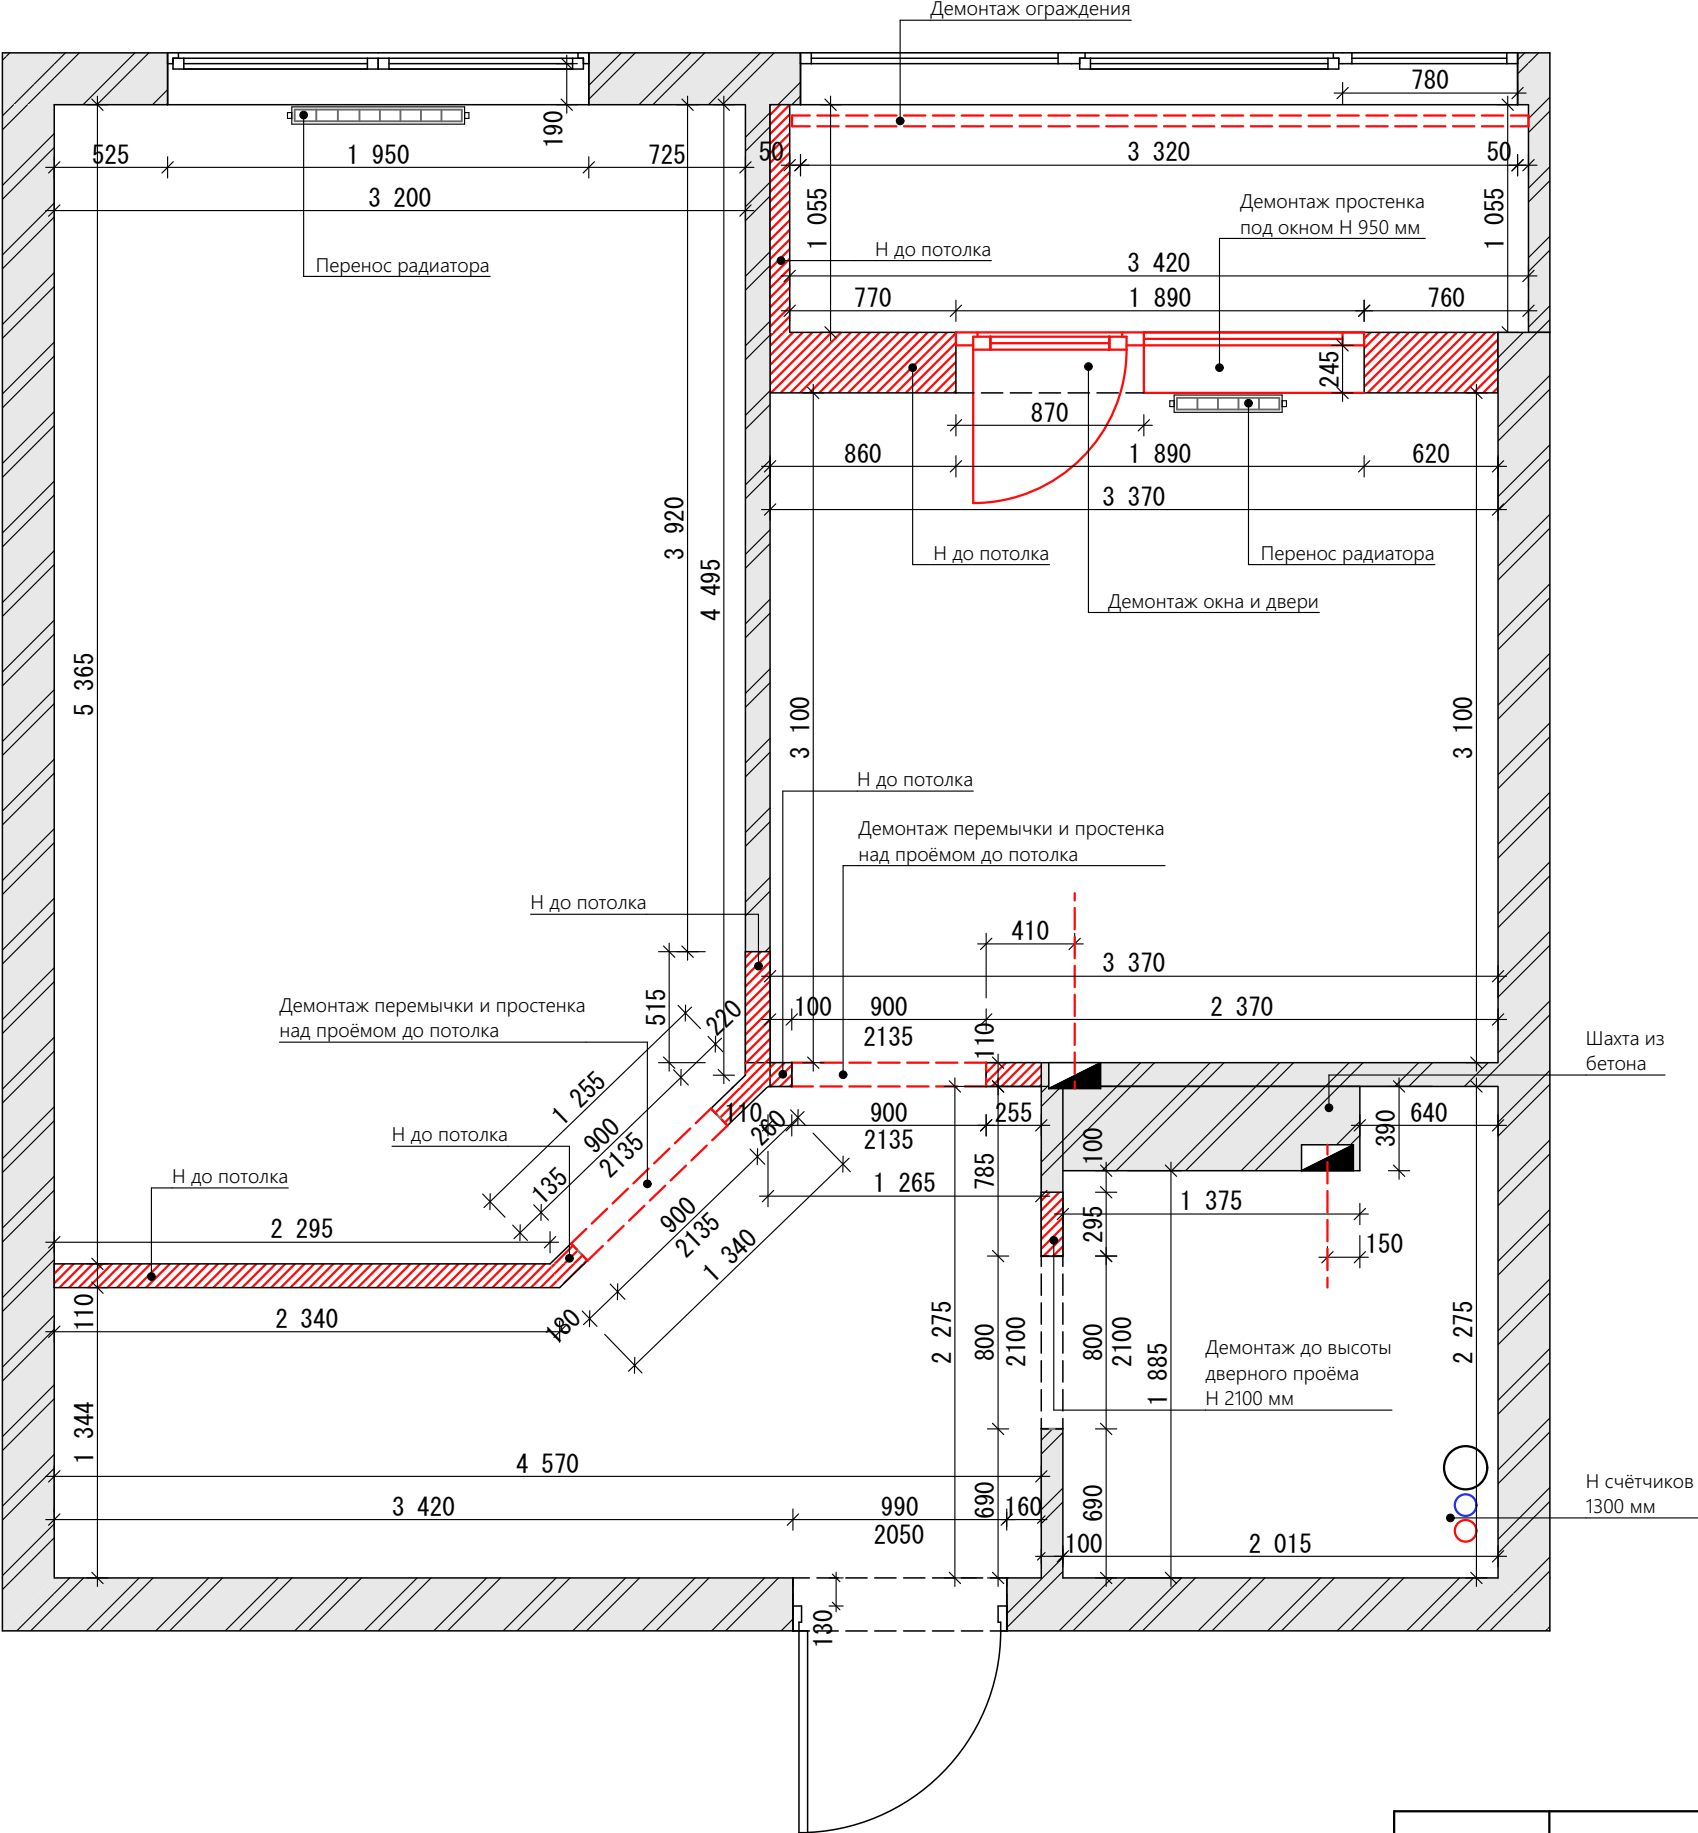

УСЛОВНЫЕ ОБОЗНАЧЕНИЯ:

	стены существующие
	водопровод канализация
	проём для вентиляции
	радиатор
	стены демонтируемые


ПРИМЕЧАНИЯ:

1. Все размеры указаны в миллиметрах.
2. Все размеры проверить по месту, возможны погрешности.
3. Размеры даны без учёта отделочных слоёв.
4. Вносимые изменения в существующую планировку квартиры (демонтаж, монтаж, перенос радиаторов, канализации и т.п.) требуют согласования в государственных и муниципальных учреждениях либо самостоятельно, либо через специализированные организации и являются ответственностью Заказчика.


		Подпись	Дата		Стадия	Лист	Масштаб
Руководитель					ДП	04	1:35
Дизайнер							
Выполнил							
Заказчик				План демонтажа			



1. Схема ниши с полками из керамогранита в санузле

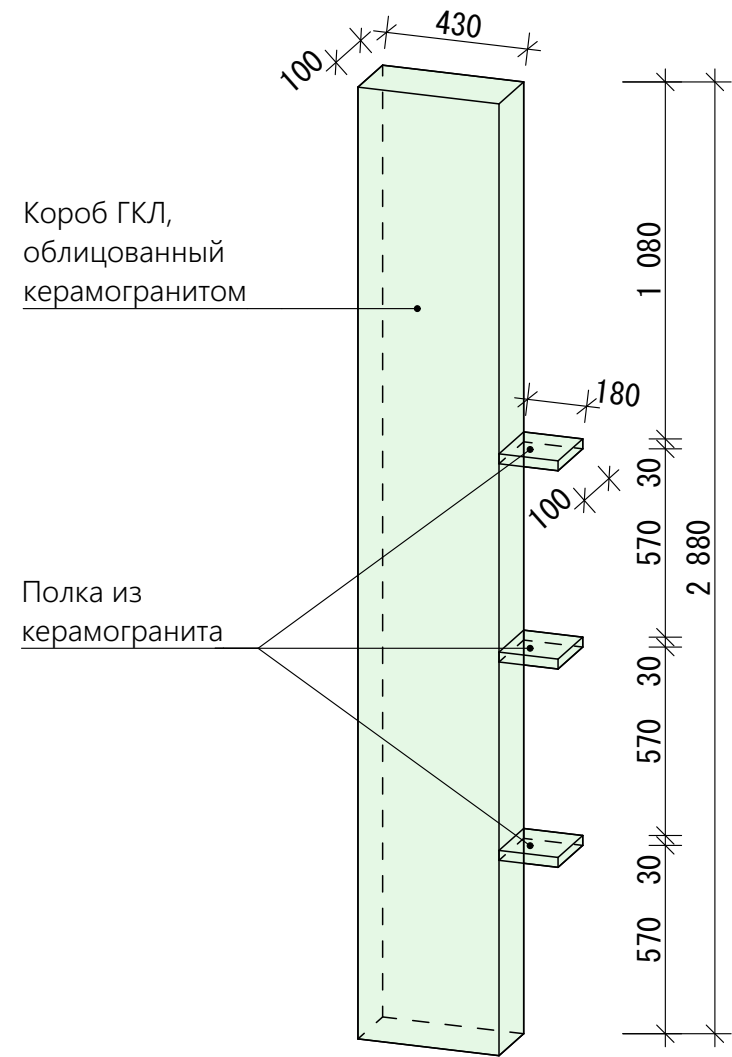

		Подпись	Дата		Стадия	Лист	Масштаб
Руководитель					ДП	06	
Дизайнер				Схемы монтажа			
Выполнил							
Заказчик							

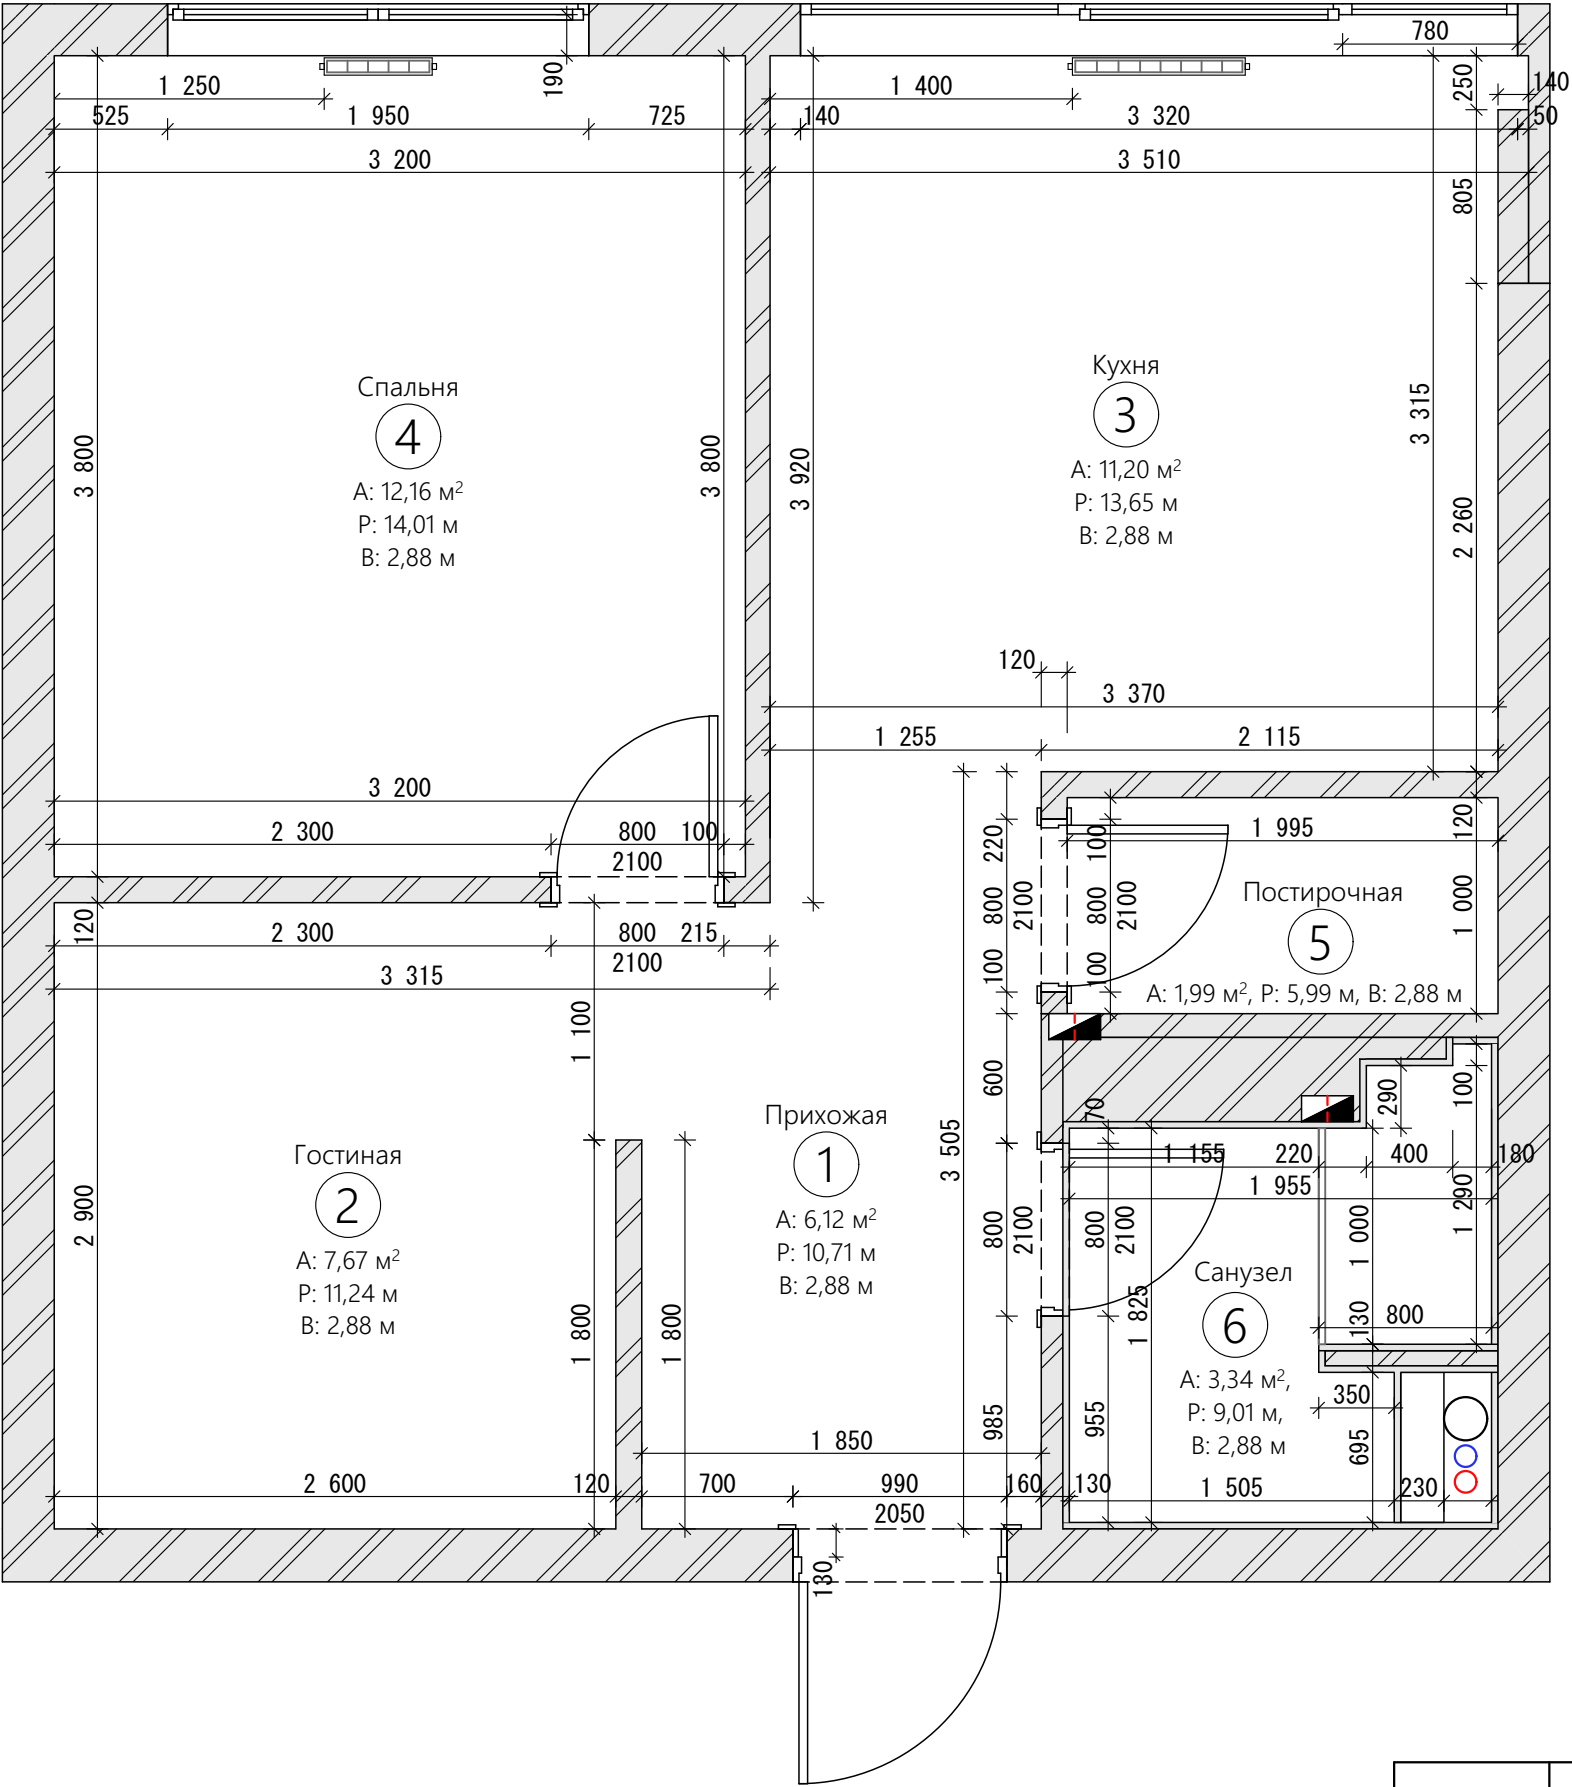

УСЛОВНЫЕ ОБОЗНАЧЕНИЯ:


	стены существующие
	водопровод канализация
	проём для вентиляции
	радиатор
А - площадь; Р - периметр; В - высота	

ЭКСПЛИКАЦИЯ ПОМЕЩЕНИЙ		
№	Наименование помещения	Площадь м²
1	Прихожая	6,12
2	Гостиная	7,67
3	Кухня	11,20
4	Спальня	12,16
5	Постирочная	1,99
6	Санузел	3,34
Общая площадь = 42,48 м²		

ПРИМЕЧАНИЯ:

- Все размеры указаны в миллиметрах.
- Все размеры проверить по месту, возможны погрешности.
- Размеры даны без учёта отделочных слоёв.

		Подпись	Дата	План перепланировки	Стадия	Лист	Масштаб
Руководитель					ДП	07	1:35
Дизайнер							
Выполнил							
Заказчик							

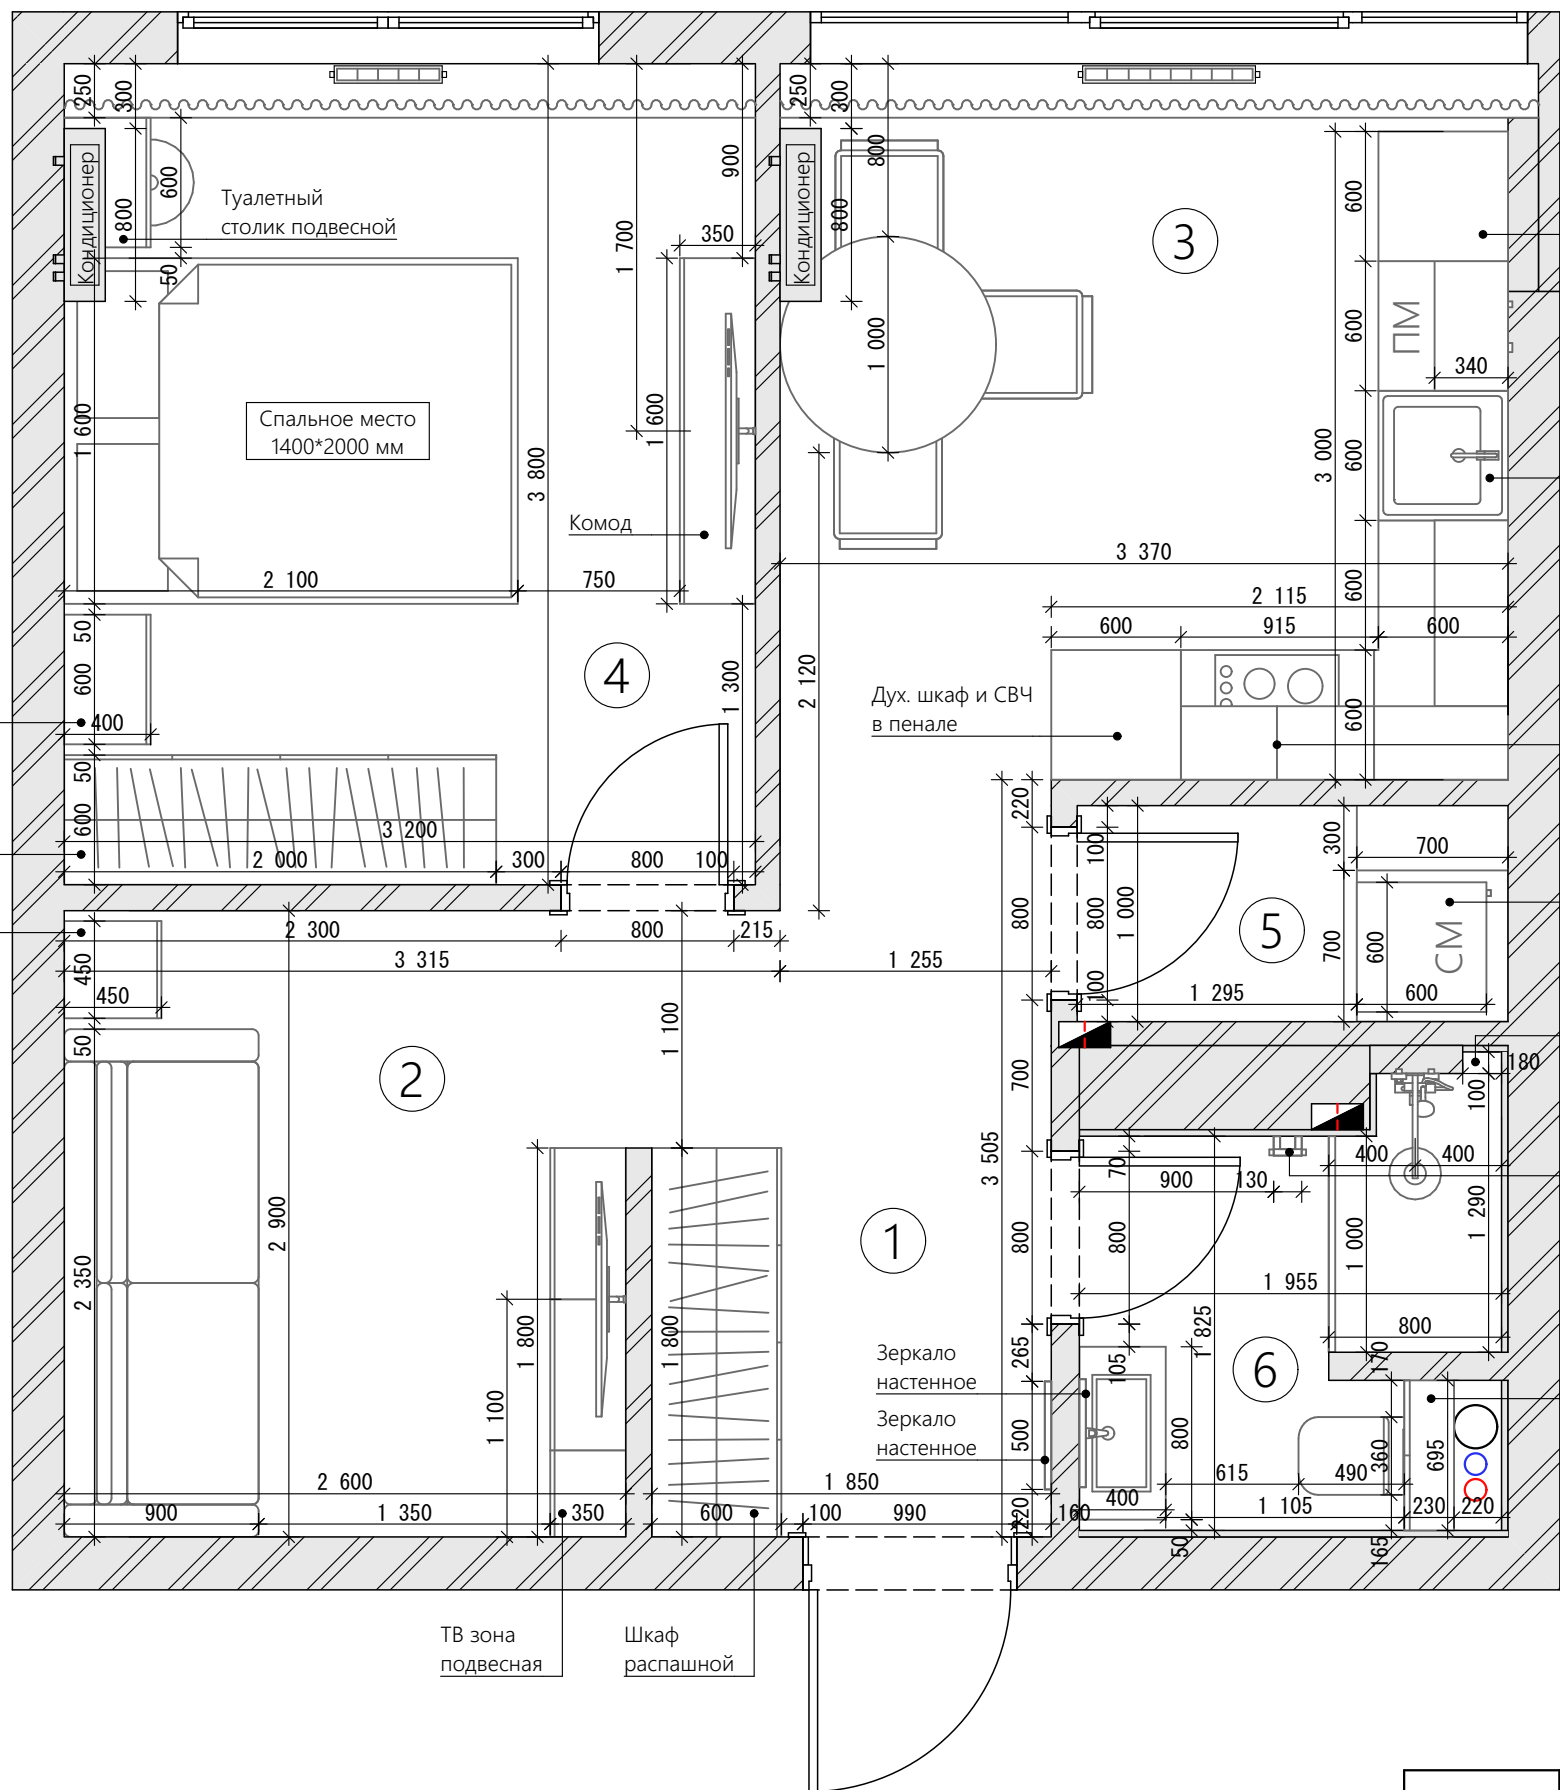

УСЛОВНЫЕ ОБОЗНАЧЕНИЯ:

	стены существующие
	электроцит
	водопровод канализация
	проём для вентиляции
	радиатор
	внутренний блок кондиционера


ЭКСПЛИКАЦИЯ ПОМЕЩЕНИЙ

№	Наименование помещения	Площадь м²
1	Прихожая	6,12
2	Гостиная	7,67
3	Кухня	11,20
4	Спальня	12,16
5	Постирочная	1,99
6	Санузел	3,34
Общая площадь = 42,48 м²		

ПРИМЕЧАНИЯ:

1. Все размеры указаны в миллиметрах.
2. Размеры даны без учёта отделочных слоёв.
3. Сокращения: ПМ - посудомоечная машина, СМ - стиральная машина, СШМ - сушильная машина.
4. Мебель индивидуального изготовления заказывать только после фактических обмеров по месту от производителя.
5. Закупка сантехнического оборудования осуществляется только после возведения перегородок, оштукатуривания стен, укладке плитки и последующей проверки размеров.

		Подпись	Дата		Стадия	Лист	Масштаб
Руководитель					ДП	08	1:35
Дизайнер							
Выполнил							
Заказчик							

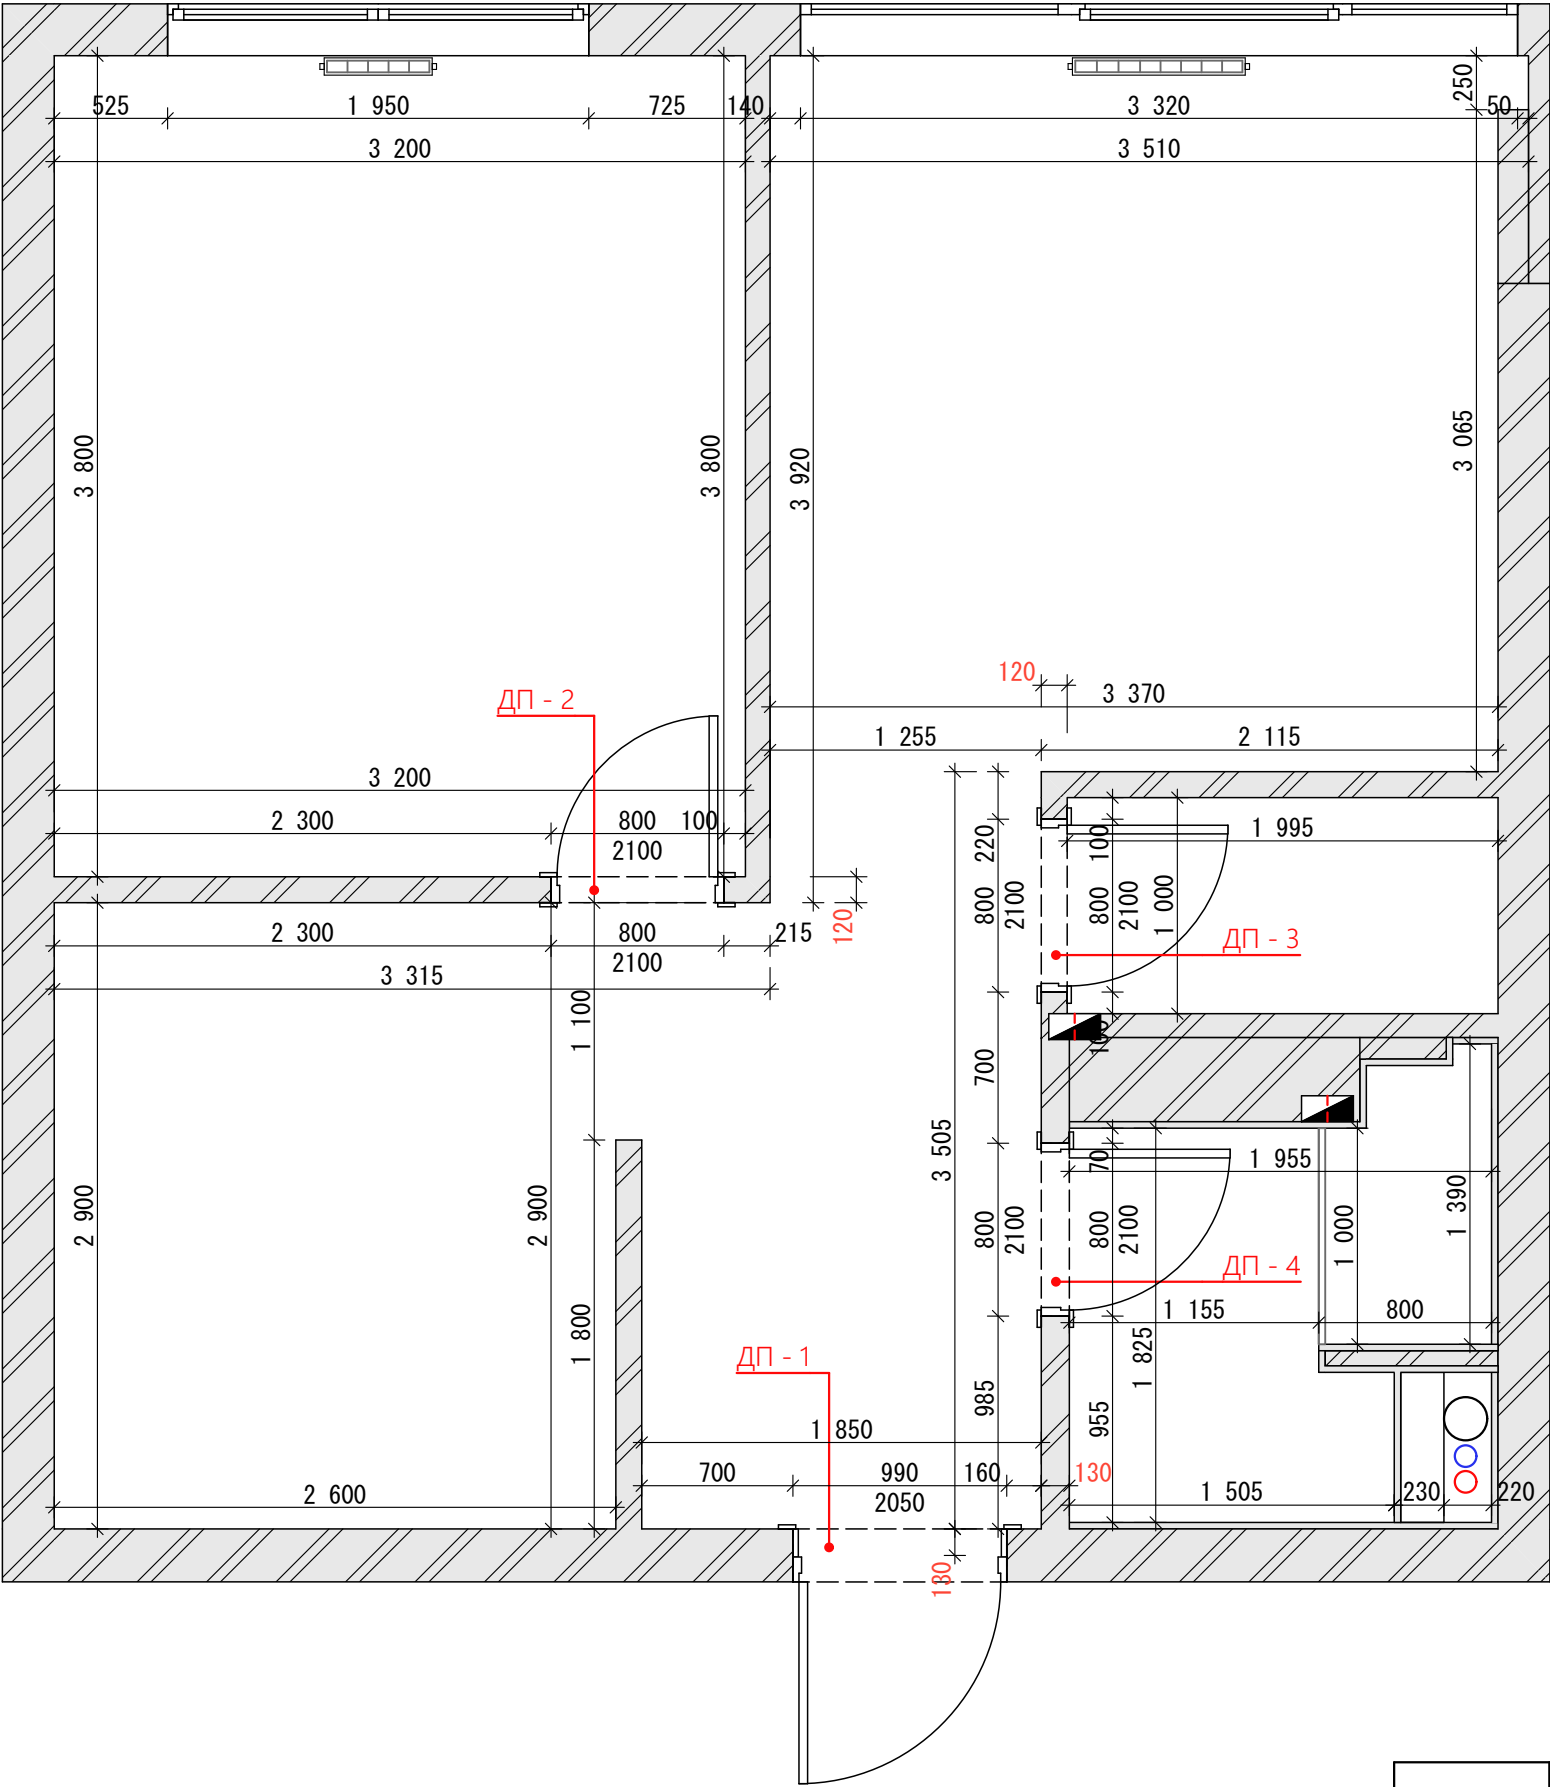

УСЛОВНЫЕ ОБОЗНАЧЕНИЯ:

	стены существующие
--	--------------------


ВЕДОМОСТЬ ДВЕРНЫХ ПОЛОТЕН:

ДП - 1	накладка на входную дверь - 890(900)*2000 мм
ДП - 2	дверное полотно межкомнат. двери - 700*2000 мм
ДП - 3	дверное полотно межкомнат. двери - 700*2000 мм
ДП - 4	дверное полотно межкомнат. двери - 700*2000 мм

ПРИМЕЧАНИЯ:

1. Все размеры указаны в миллиметрах.
2. Размеры даны без учёта отделочных слоёв.
3. Ширину проёмов проверить, и выполнить в соответствии с требованиям по установке дверных коробок.
4. Размеры межкомнатных проёмов уточнить после окончательного согласования моделей дверей.
5. Все привязки даны относительно дверного проёма, а не полотна!

		Подпись	Дата		Стадия	Лист	Масштаб
Руководитель					ДП	09	1:35
Дизайнер				План формирования дверных проёмов			
Выполнил							
Заказчик							

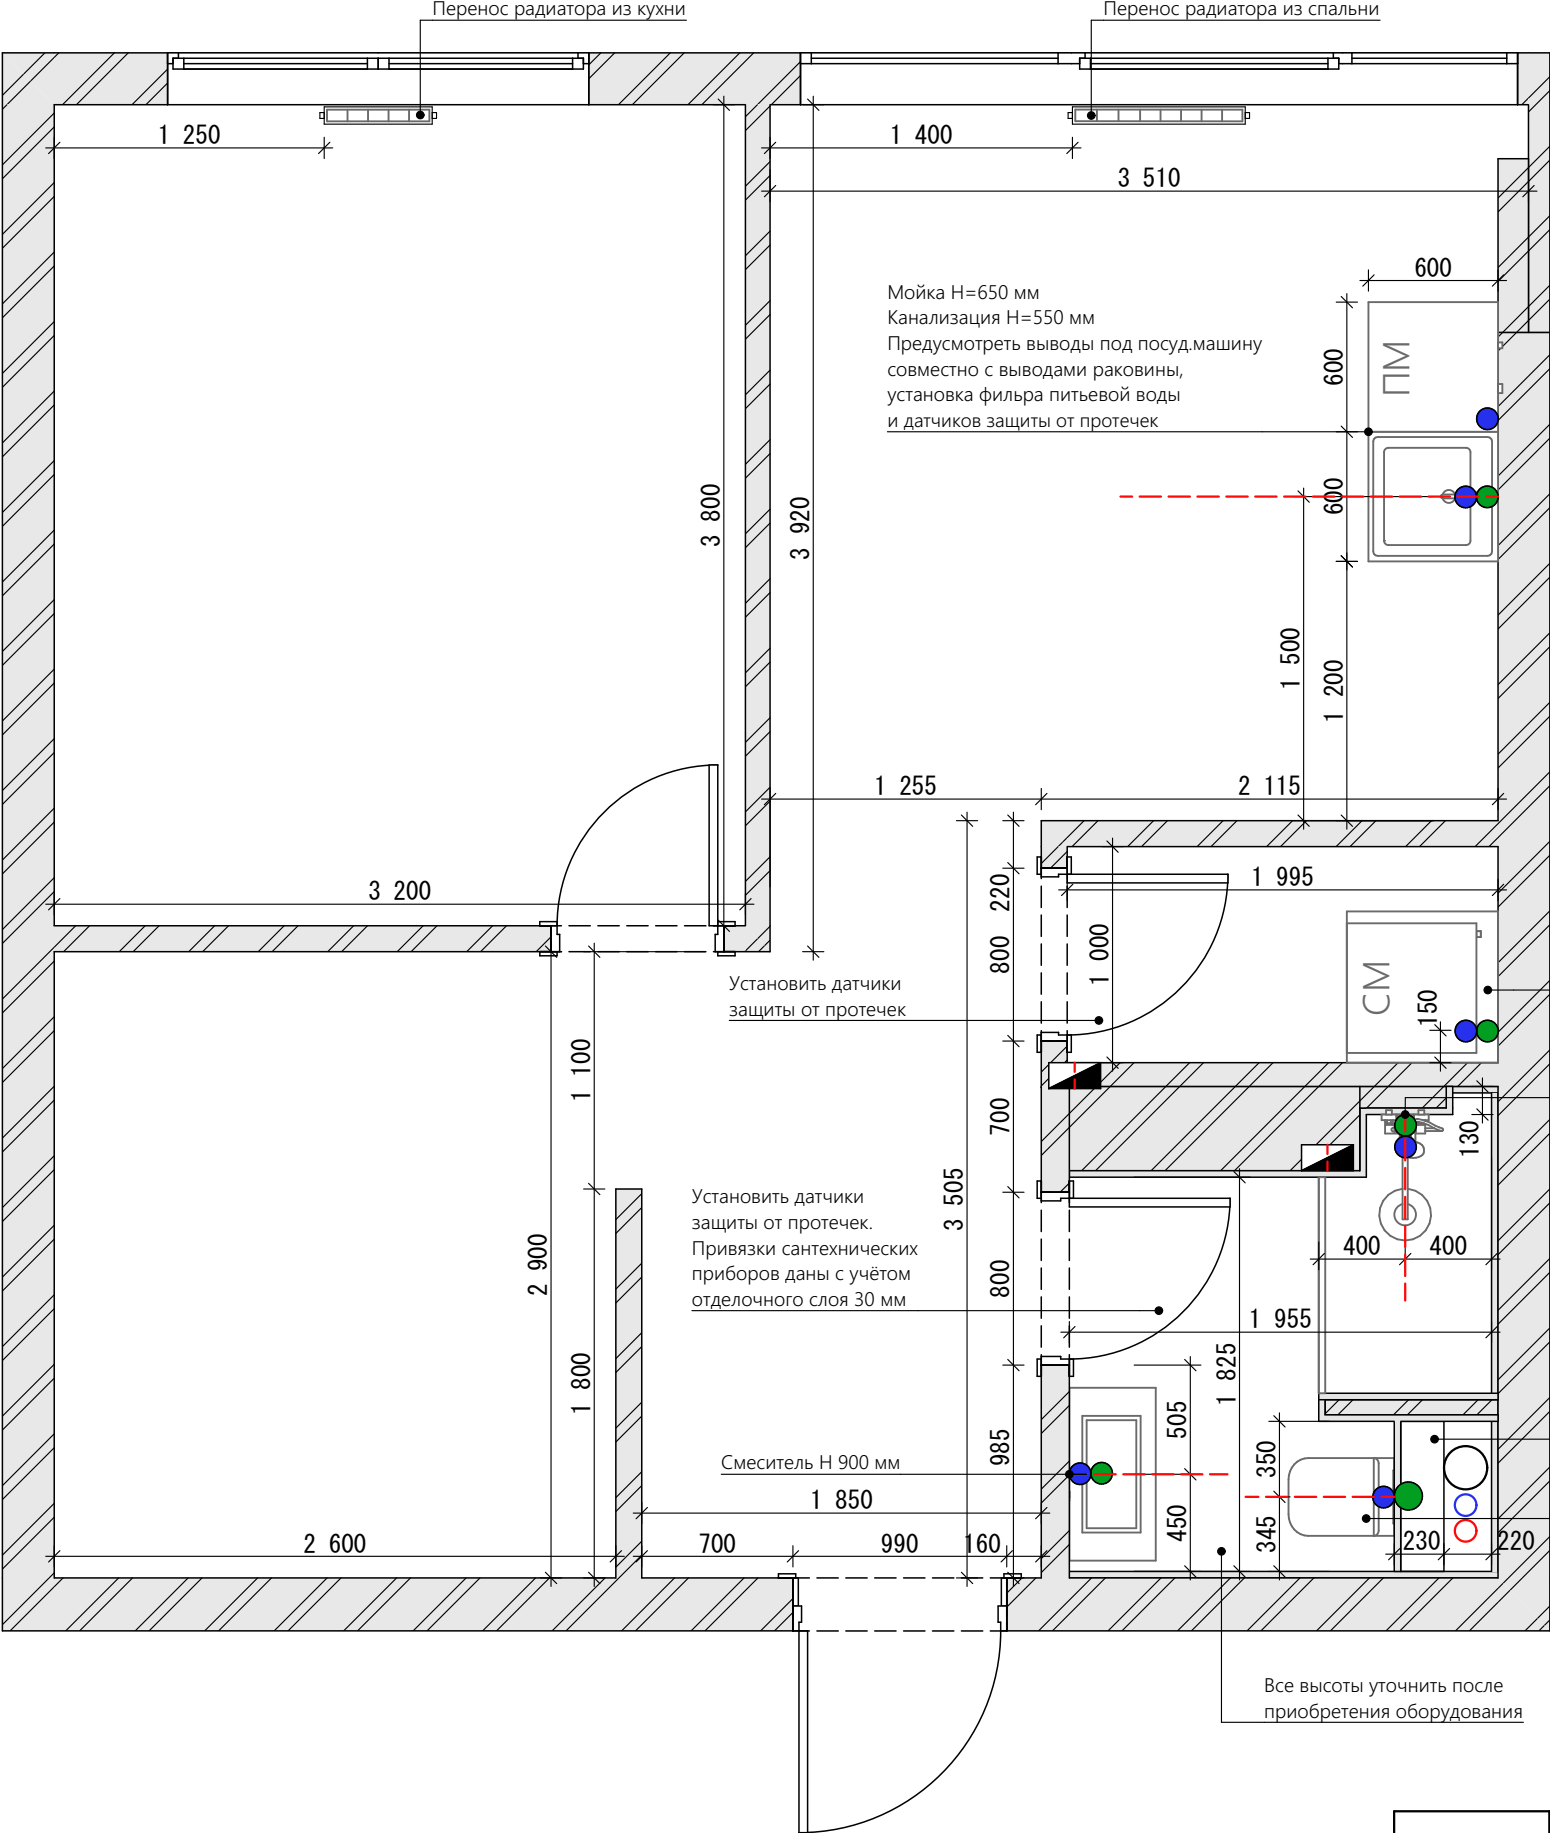










УСЛОВНЫЕ ОБОЗНАЧЕНИЯ:

	стены существующие
	канализационный вывод
	датчик защиты от протечек
	слой штукатурки, плитки клея - 30 мм


ПРИМЕЧАНИЯ:

1. Все размеры указаны в миллиметрах.
2. Размеры даны без учёта отделочных слоёв.
3. Лист смотреть совместно с развёртками стен.
4. Коммуникации штробим (уточнить по месту).
5. Привязка по оси сантехнического оборудования.
6. Установка сантехнического оборудования согласно тех. картам.
7. Все высоты выполнить согласно тех.картам купленного сантехнического оборудования.
8. Закупка сантехнического оборудования осуществляется только после возведения перегородок, оштукатуривания стен, укладки плитки и последующей проверки размеров.

		Подпись	Дата		Стадия	Лист	Масштаб
Руководитель					ДП	10	1:35
Дизайнер				Общий план расстановки сантехнических приборов			
Выполнил							
Заказчик							

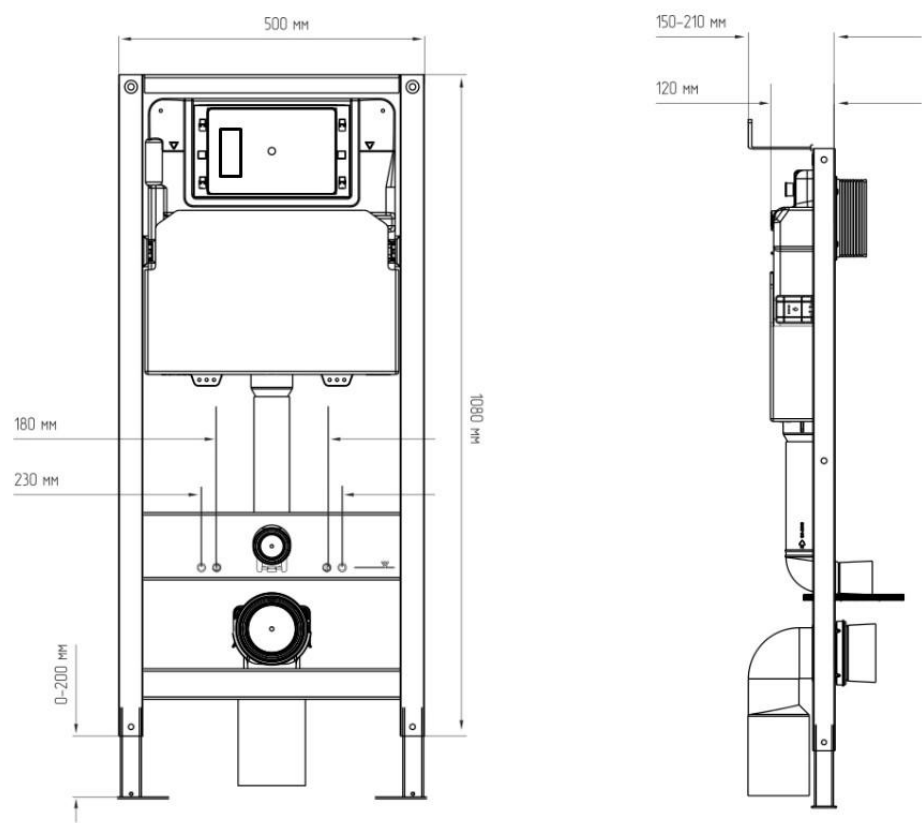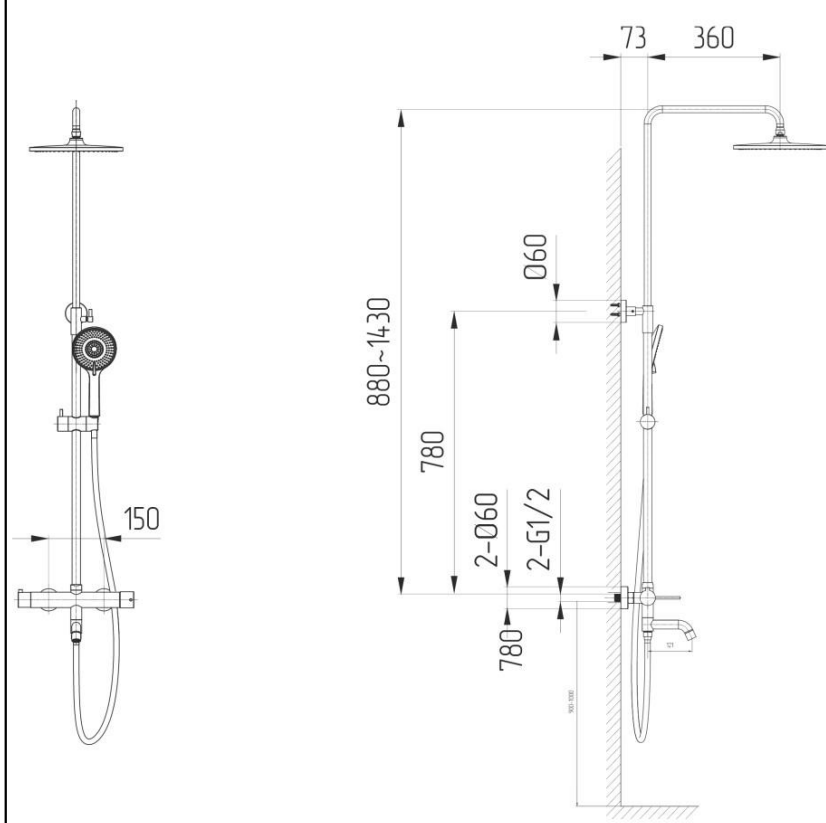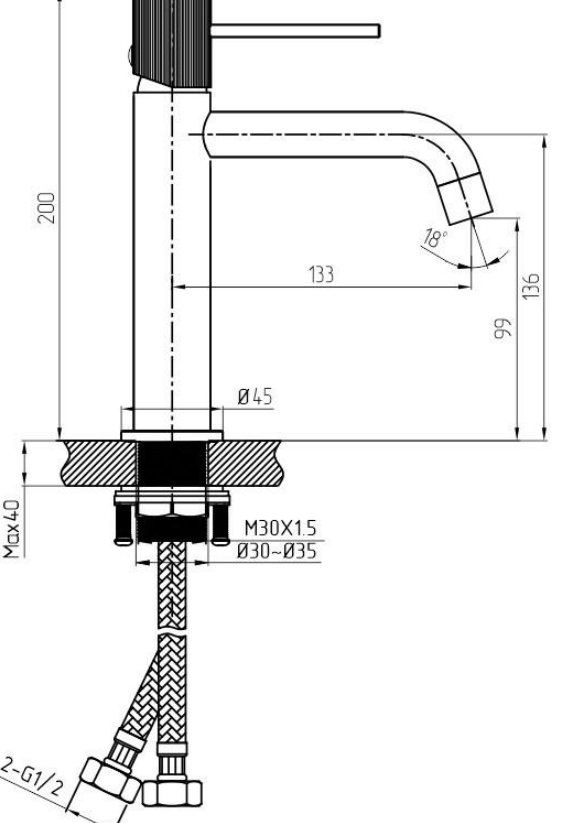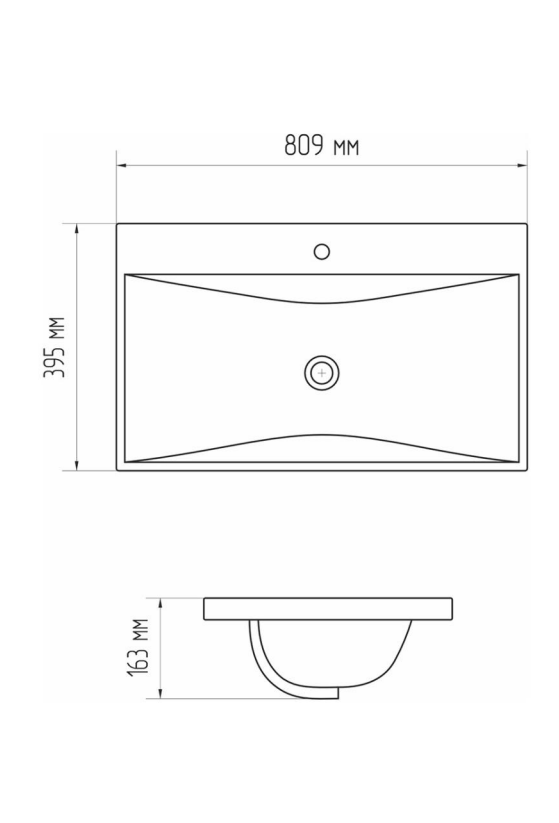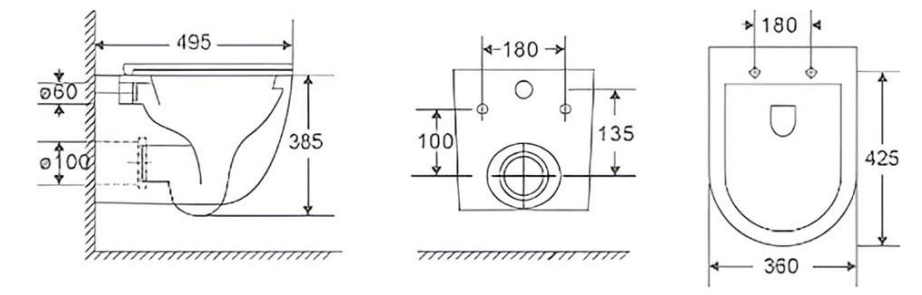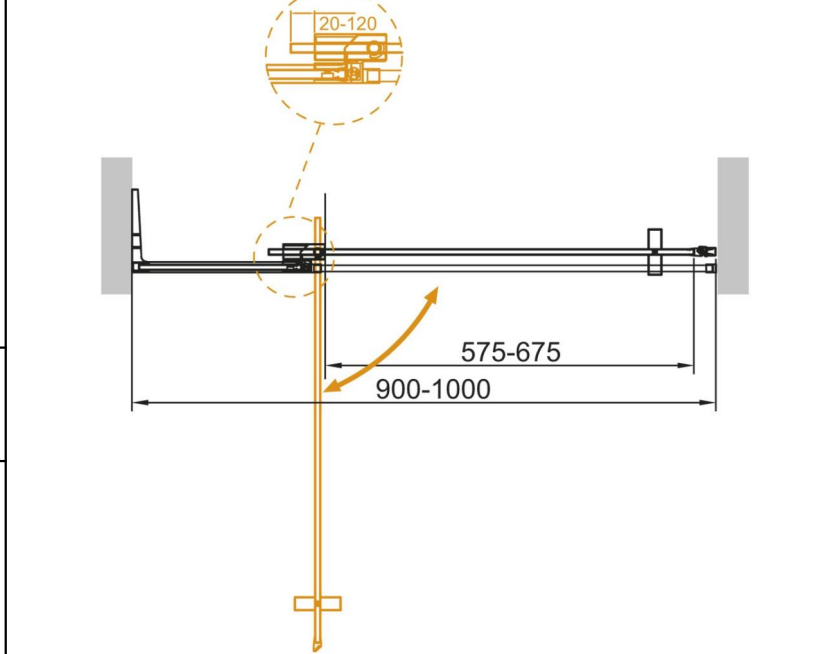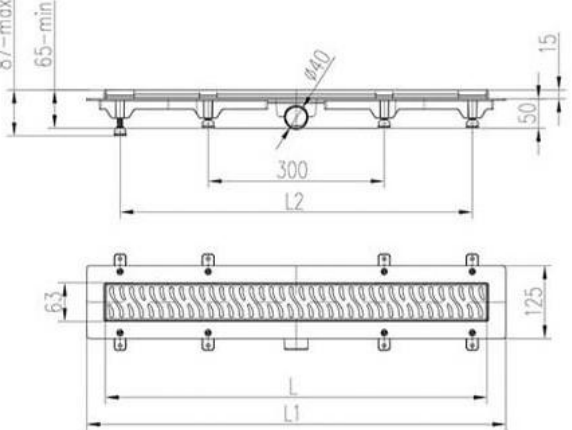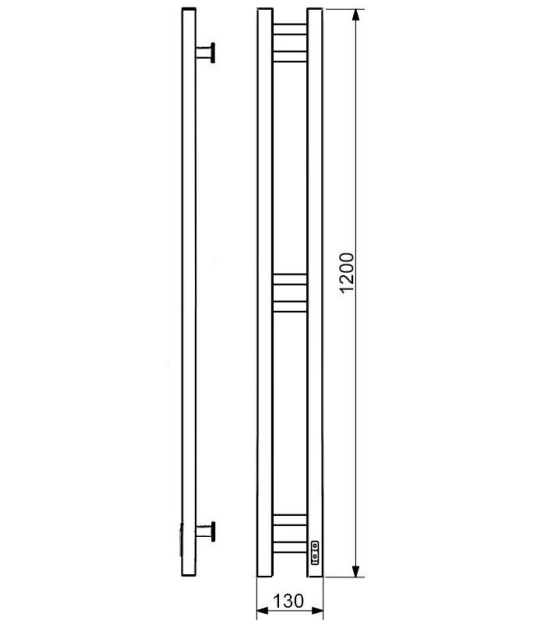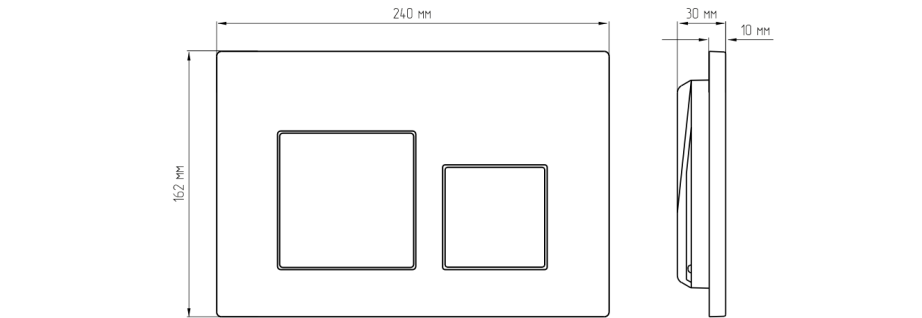Система инсталляции для унитазов AVS с отверстием для дезинфицирующих таблеток	Душевая стойка AVS Slimmer оружейная сталь	Смеситель для раковины AVS Pulse оружейная сталь	Раковина AVS эмаль белый ГАРМОНИЯ SL																																
																																			
Унитаз подвесной AVS Атлант безободковый, белый	Душевая дверь в нишу Cezares Slider 90-100 профиль черный, прозрачное стекло	Водоотводящий желоб 450 МСН с сеточками СН 450 МС сет	Полотенцесушитель электрический Nika Robe-2 120x10 черный матовый																																
		 <table><thead><tr><th>L [mm]</th><th>L1 [mm]</th><th>L2 [mm]</th><th>Вес [кг/м]</th></tr></thead><tbody><tr><td>350</td><td>415</td><td>295</td><td>1,04</td></tr><tr><td>450</td><td>515</td><td>295</td><td>1,19</td></tr><tr><td>550</td><td>615</td><td>495</td><td>1,32</td></tr><tr><td>650</td><td>715</td><td>595</td><td>1,71</td></tr><tr><td>750</td><td>815</td><td>695</td><td>1,85</td></tr><tr><td>850</td><td>915</td><td>795</td><td>2,02</td></tr><tr><td>950</td><td>1015</td><td>895</td><td>2,20</td></tr></tbody></table>	L [mm]	L1 [mm]	L2 [mm]	Вес [кг/м]	350	415	295	1,04	450	515	295	1,19	550	615	495	1,32	650	715	595	1,71	750	815	695	1,85	850	915	795	2,02	950	1015	895	2,20	
L [mm]	L1 [mm]	L2 [mm]	Вес [кг/м]																																
350	415	295	1,04																																
450	515	295	1,19																																
550	615	495	1,32																																
650	715	595	1,71																																
750	815	695	1,85																																
850	915	795	2,02																																
950	1015	895	2,20																																
Клавиша смыва AVS оружейная сталь квадратные кнопки	ПРИМЕЧАНИЯ: Закупка сантехнического оборудования осуществляется только после возведения перегородок, оштукатуривания стен, укладки плитки и последующей проверки размеров.																																		
	<table><tr><td></td><td></td><td>Подпись</td><td>Дата</td></tr><tr><td>Руководитель</td><td></td><td></td><td></td></tr><tr><td>Дизайнер</td><td></td><td></td><td></td></tr><tr><td>Выполнил</td><td></td><td></td><td></td></tr><tr><td>Заказчик</td><td></td><td></td><td></td></tr></table>				Подпись	Дата	Руководитель				Дизайнер				Выполнил				Заказчик				<table><tr><td></td><td>План технических карт сантехнических приборов</td><td>Стадия</td><td>Лист</td><td>Масштаб</td></tr><tr><td></td><td></td><td>ДП</td><td>11</td><td></td></tr></table>		План технических карт сантехнических приборов	Стадия	Лист	Масштаб			ДП	11			
		Подпись	Дата																																
Руководитель																																			
Дизайнер																																			
Выполнил																																			
Заказчик																																			
	План технических карт сантехнических приборов	Стадия	Лист	Масштаб																															
		ДП	11																																

Развёртки стен Санузел - привязка сантехники, раскладка плитки
S стен = 25,48 м²

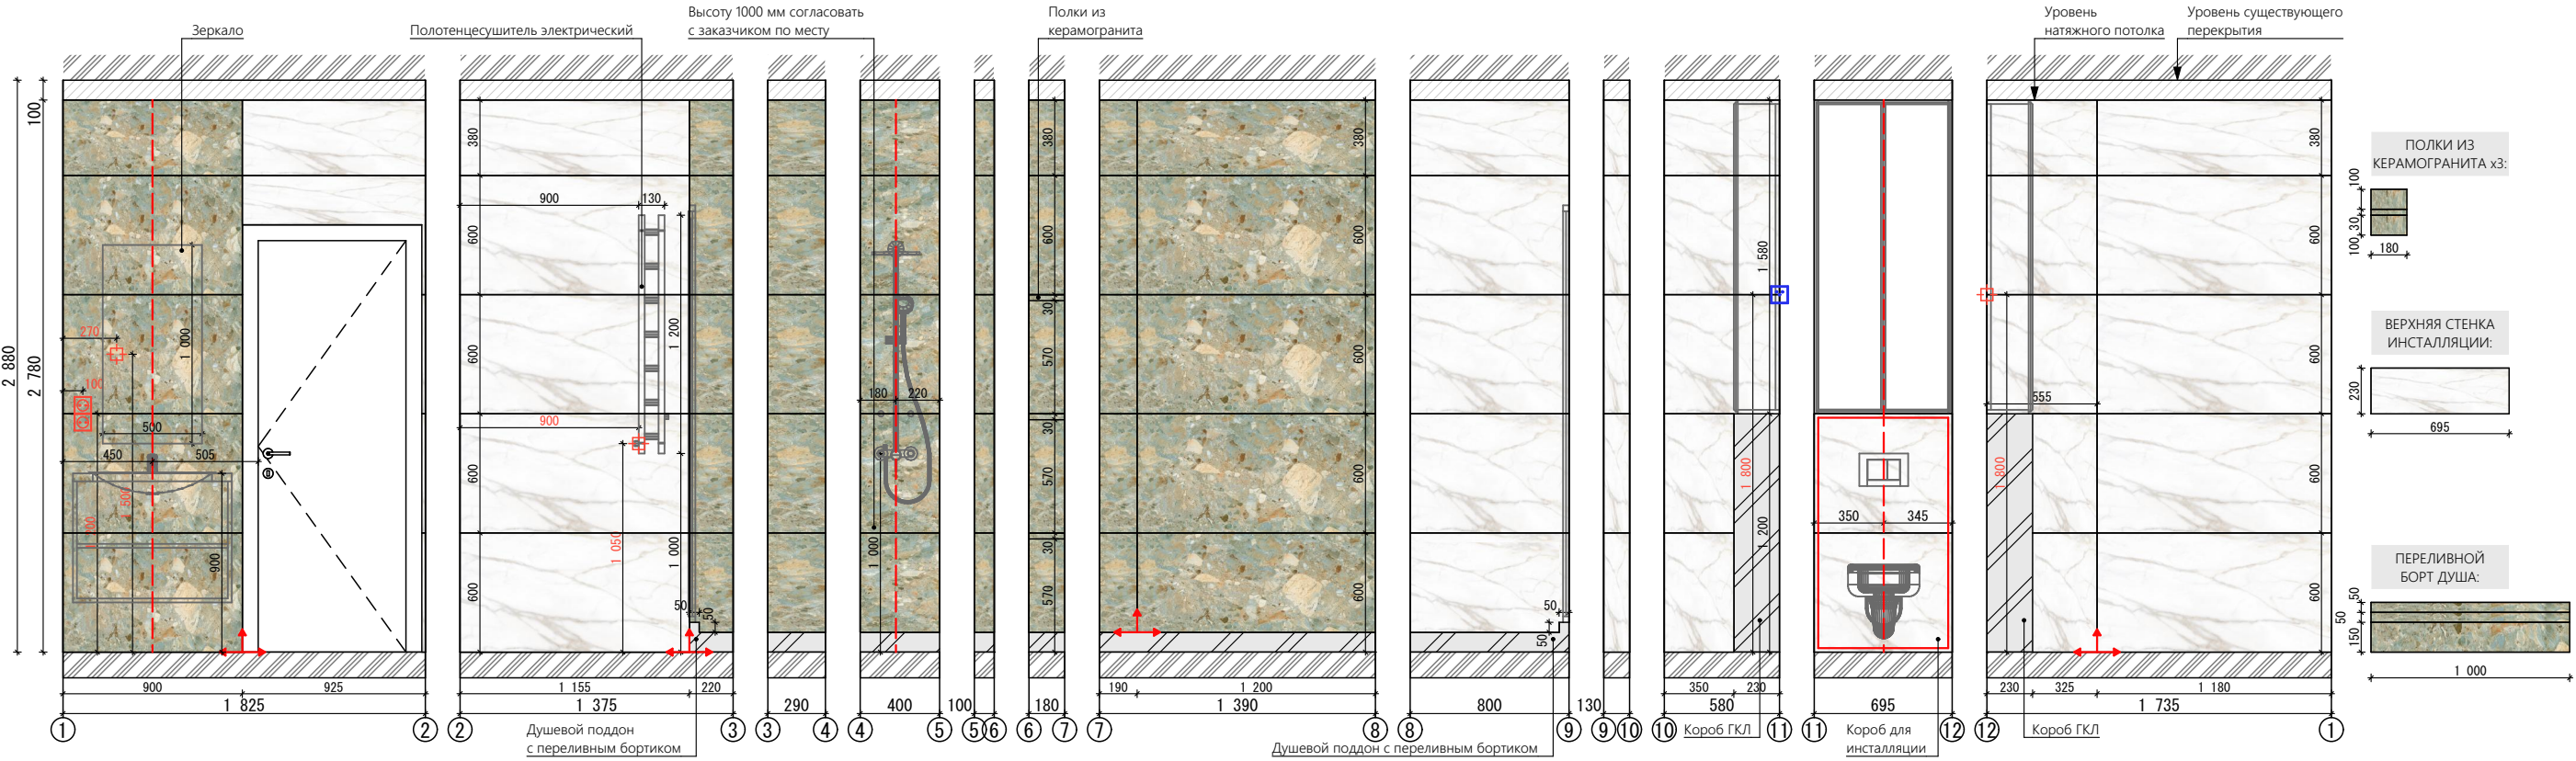



УСЛОВНЫЕ ОБОЗНАЧЕНИЯ:

	Керамогранит Ametis SM02 белый 1 матовый 600*1200*10 мм, реттифициров, затирка Мареi 103. Площадь без запаса: 13,21 м²
	Керамогранит AVS Lilas зелёный глянцевый 600*1200*9 мм, реттифициров, затирка Мареi 132. Площадь без запаса: 9,83 м²
	розетка/силовой вывод
	электрический вывод
	начало расклада

ПРИМЕЧАНИЯ:


- Все размеры указаны в миллиметрах.
- Размеры даны без учёта отделочных слоёв.
- Углы плитки зашлифовывать под 45 градусов.
- Шов минимальный (реттифицированный керамогранит).
- Каждый вид керамогранита затирается своим цветом затирки - уточнить у дизайнера.
- Привязка сантехнического оборудования - по центральной оси.
- Установка сантехнического оборудования согласно тех. картам, см. лист 11.
- Закупка сантехнического оборудования осуществляется только после возведения перегородок, оштукатуривания стен, укладки плитки и последующей проверки размеров.
- Привязка электрики возле двери дана от дверного проёма, а не от полотна!
- Лист смотреть совместно с 3D-визуализациями.

! Раскладку керамогранита по стенам
смотреть по факту монтажа. В случае,
если размеры керамогранита Ametis и
AVS будут сильно отличаться, выполнить
раскладку со смещением по вертикали
на 1/2.

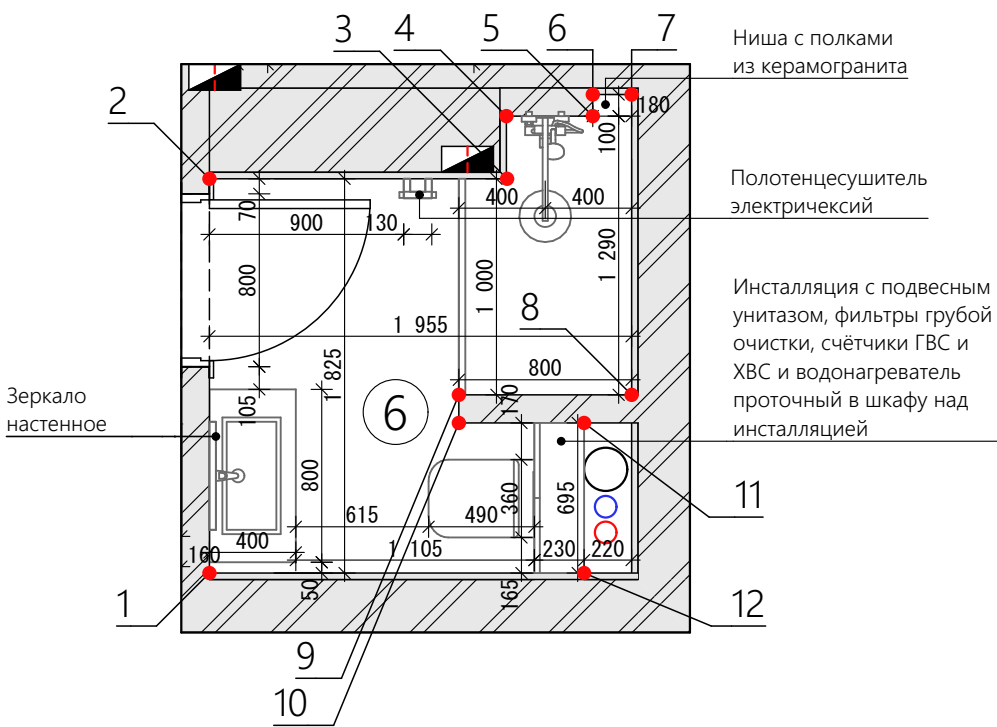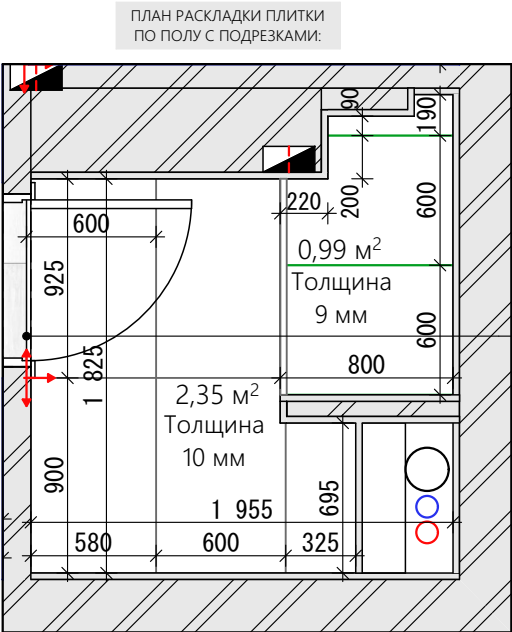

		Подпись	Дата		Стадия	Лист	Масштаб
Руководитель					ДП	12	1:35
Дизайнер							
Выполнил							
Заказчик							
				Развёртки стен Санузел			

 


	стены существующие
	потолок натяжной, цвет белый матовый - 40,83 м ²
	ГКЛ потолок, покраска, цвет белый матовый
	вставка резиновая чёрная для натяжн. потолка - 66,49 м. пог.
	потолочный карниз для штор 2-рядный - 6,71 м. пог.
	электровентилятор потолочного монтажа, R=65

ПРИМЕЧАНИЯ:

1. Все размеры указаны в миллиметрах.
2. Размеры даны без учёта отделочных слоёв.
3. Лист смотреть совместно с развёртками стен и 3д визуализациями.
4. Все площади посчитаны без запаса.
5. Коммуникации штробим.
6. Перед монтажом потолков уточнить монтажную глубину выбранных светильников.

		Подпись	Дата		Стадия	Лист	Масштаб
Руководитель					ДП	13	1:35
Дизайнер				План потолка			
Выполнил							
Заказчик							

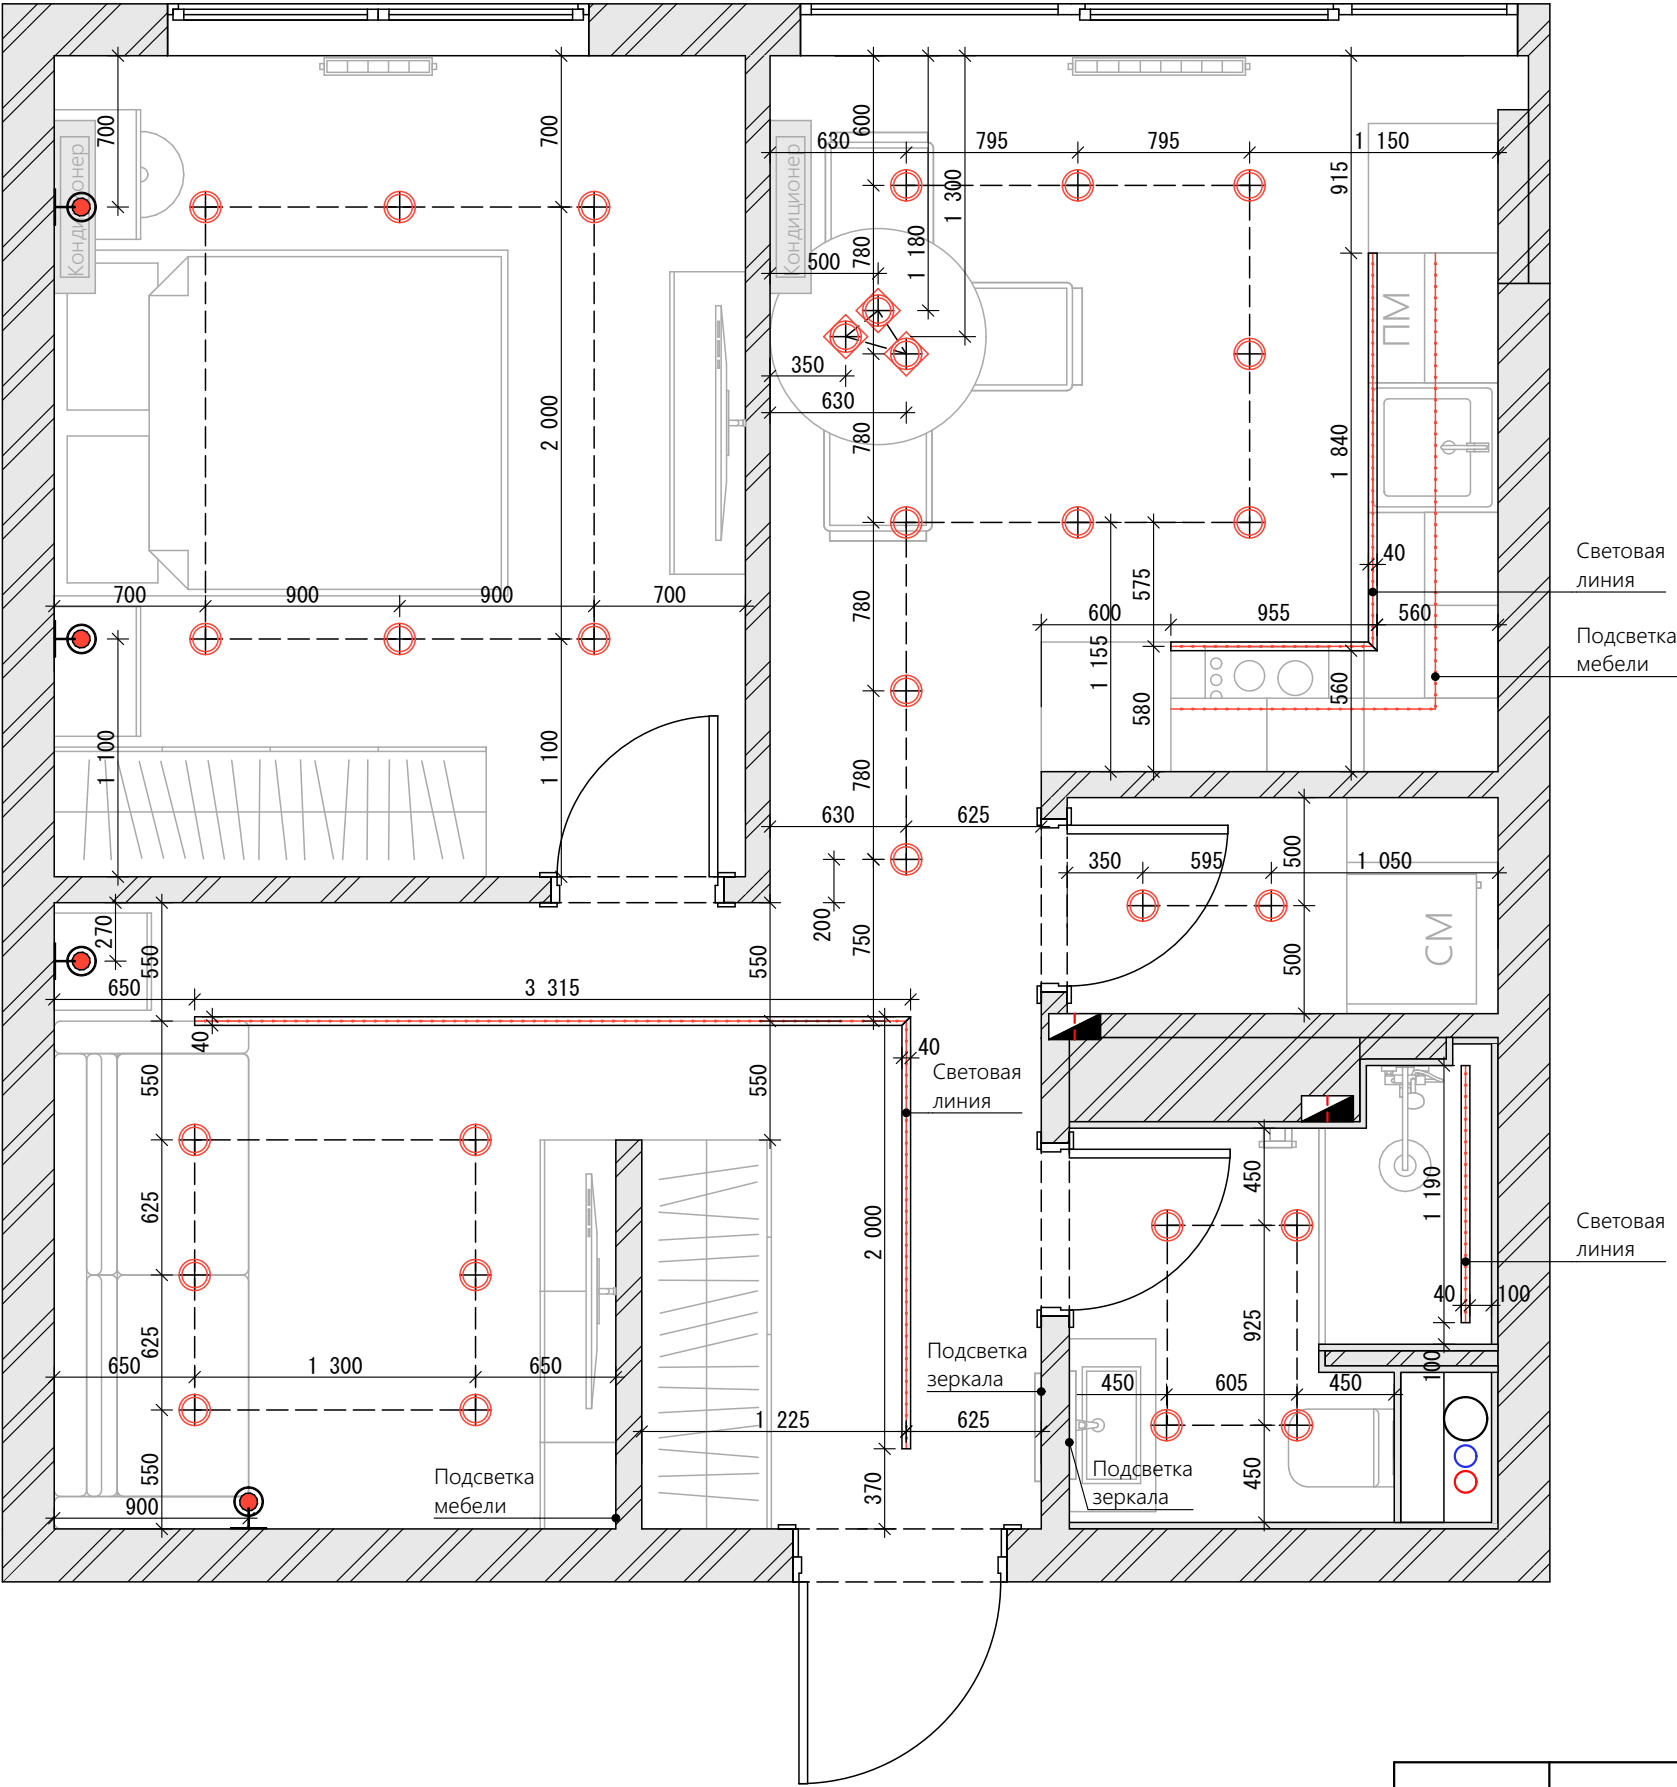


УСЛОВНЫЕ ОБОЗНАЧЕНИЯ:

	светильник встраиваемый - 27 шт.
	светильник подвесной - 3 шт.
	бра - 4 шт.
	световая линия - 9,31 м. пог.
	светодиодная лента
	электроцит

ПРИМЕЧАНИЯ:

1. Все размеры указаны в миллиметрах.
2. Размеры даны без учёта отделочных слоёв.
3. Лист смотреть совместно с развёртками стен.
4. Расположение осветительного оборудования указано относительно центра светильника.
5. Для электровыводов дать запас.
6. Светодиодная лента посчитана без учёта подсветки мебели.

		Подпись	Дата		Стадия	Лист	Масштаб
Руководитель					ДП	14	1:35
Дизайнер				План расстановки осветительного оборудования			
Выполнил							
Заказчик							

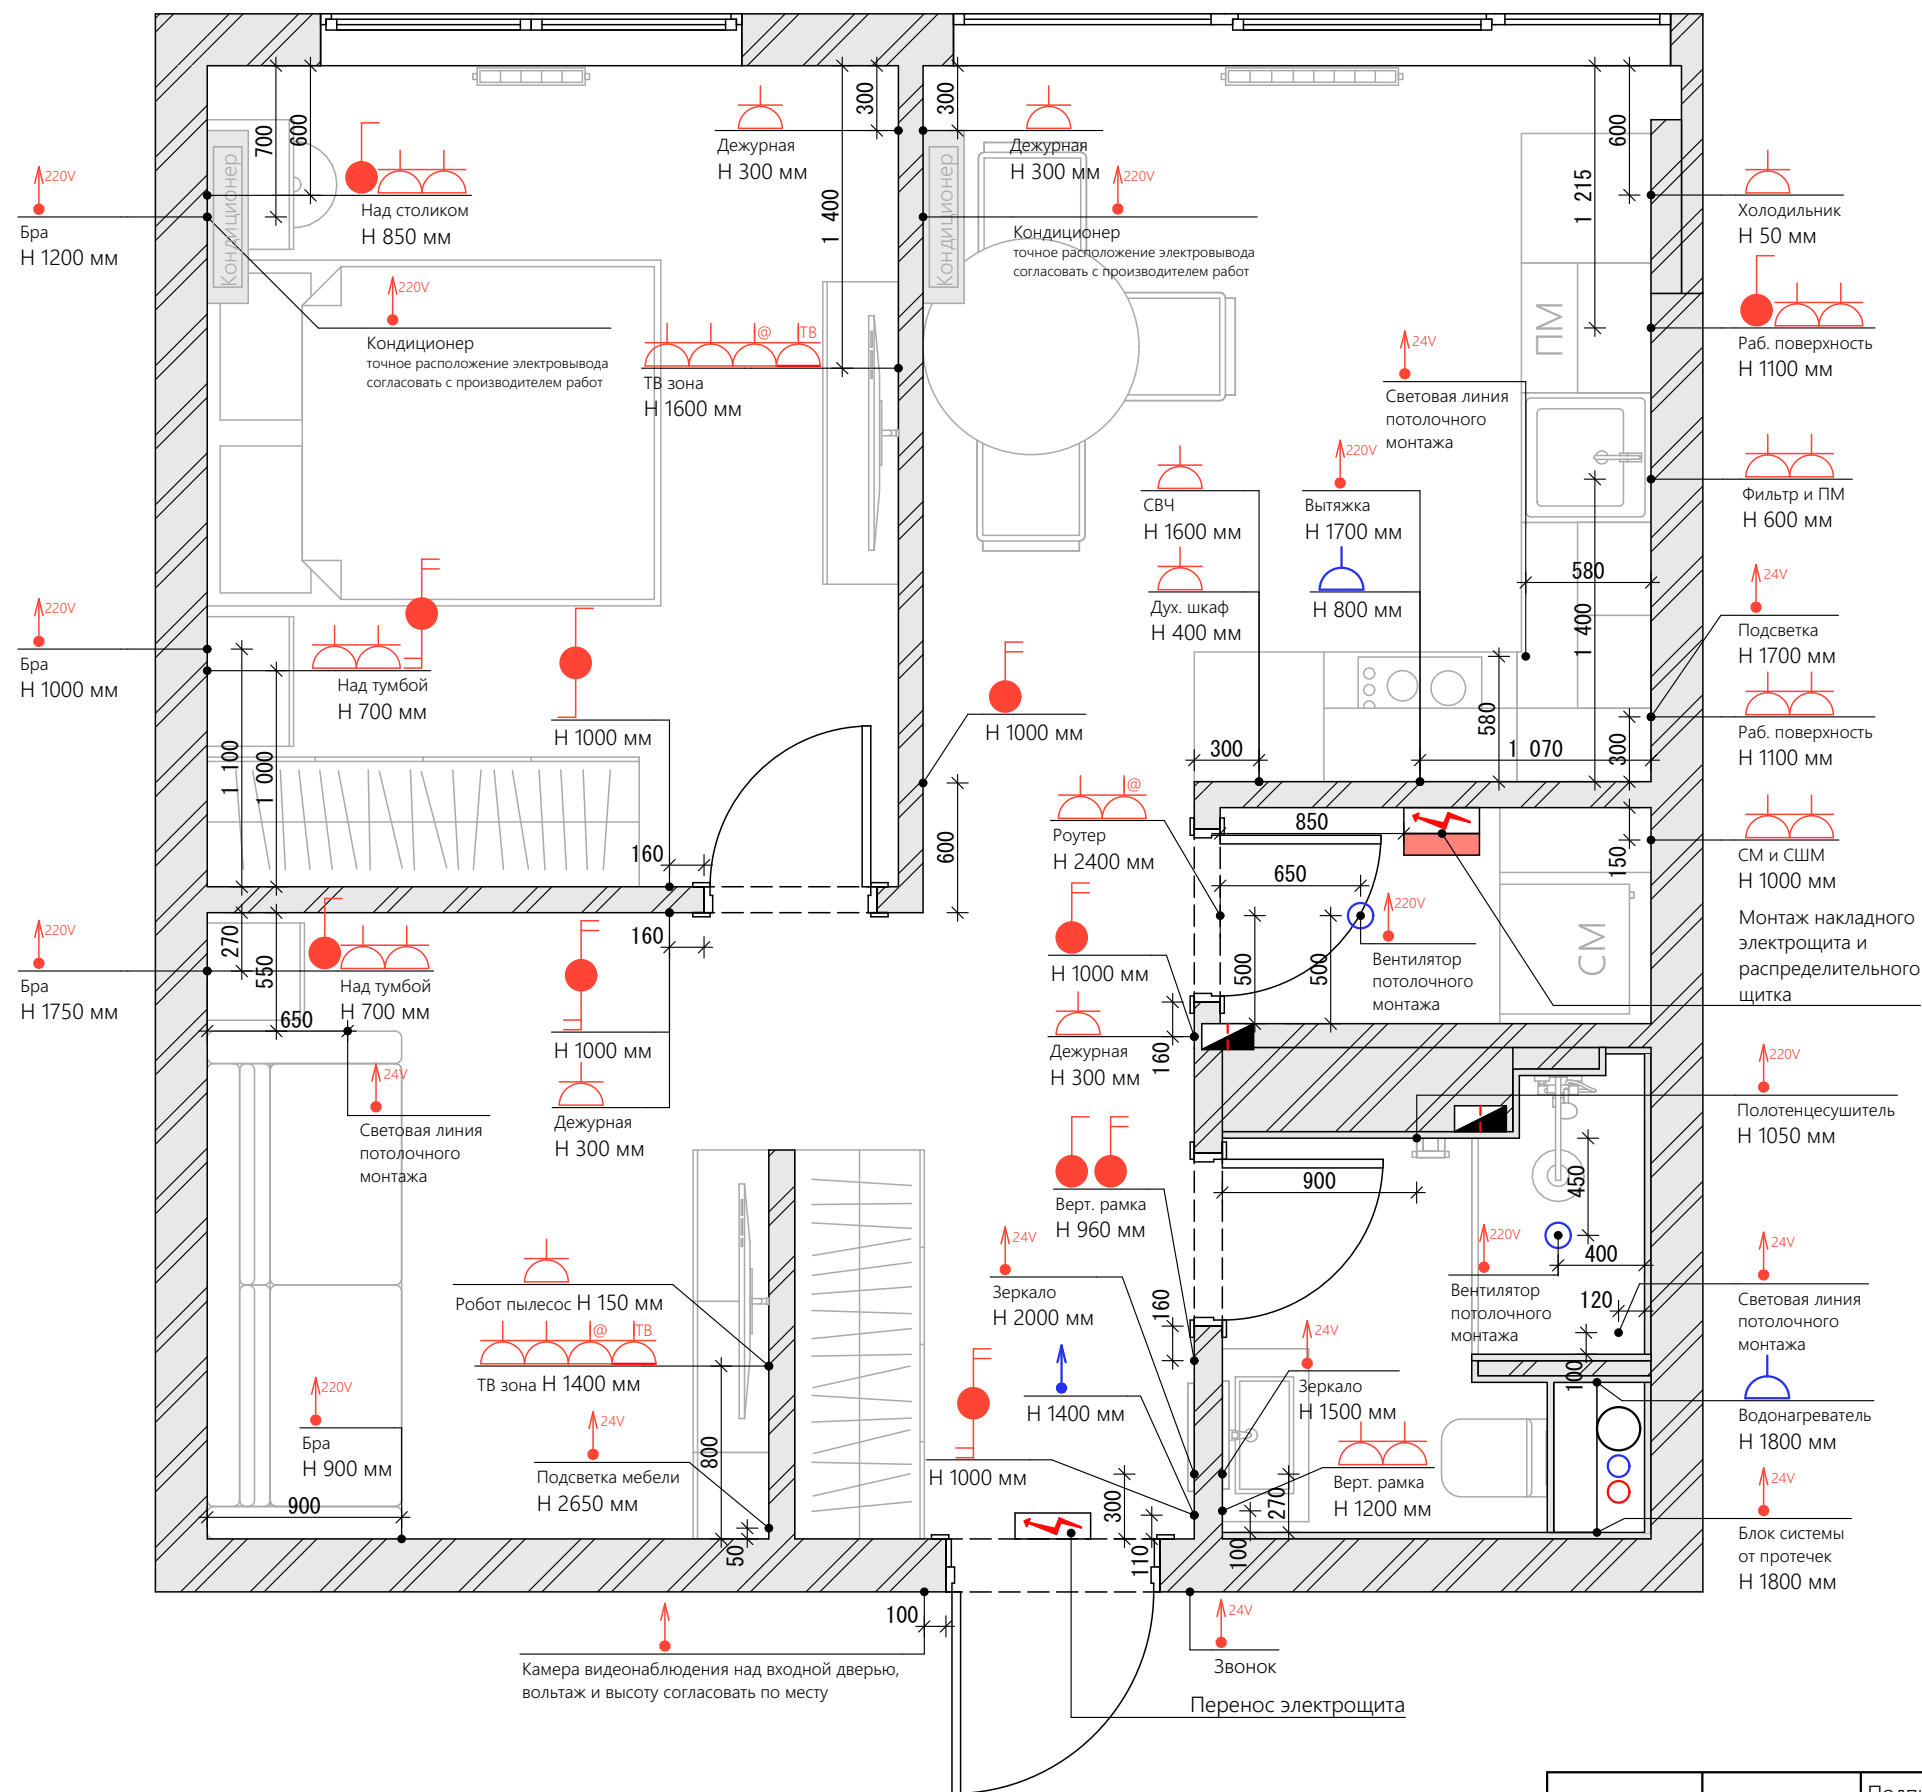


УСЛОВНЫЕ ОБОЗНАЧЕНИЯ:

	1 кл. выключатель - 4 шт.
	2 кл. выключатель - 3 шт.
	1 кл. прох. выключатель - 1 шт.
	2 кл. прох. выключатель - 3 шт.
	выпуск 220V - 10 шт.
	выпуск 24V - 9 шт.
	выпуск для домофона - 1 шт.
	розетка - 29 шт.
	силовой вывод - 2 шт.
	розетка интернет - 3 шт.
	розетка тв - 2 шт.
	электрощит
	распределительный щиток для светодиодных лент

ПРИМЕЧАНИЯ:

1. Все размеры указаны в миллиметрах.
2. Лист смотреть совместно с развертками стен.
3. Размеры даны без учёта отделочных слоёв.
4. Расположение розеток и выводов указано относительно центра розетки или группы розеток.
5. Все розетки, необозначенные отметкой высоты, устанавливаются на высоту 300 мм от уровня пола, выключатели 1000 мм.
6. Точное расположение розеток и выводов для кухонной техники уточнить при заказе кухни.
7. Выводы под сплит-систему даны к нижней точке корпуса со стороны стены, согласно купленной модели.
8. Выводы в зонах TV требуют согласования с учетом выбранного оборудования.
9. Дать запас электровыводам не менее 500мм.

		Подпись	Дата	План расположения розеток и выключателей	Стадия	Лист	Масштаб
Руководитель					ДП	15	1:35
Дизайнер							
Выполнил							
Заказчик							

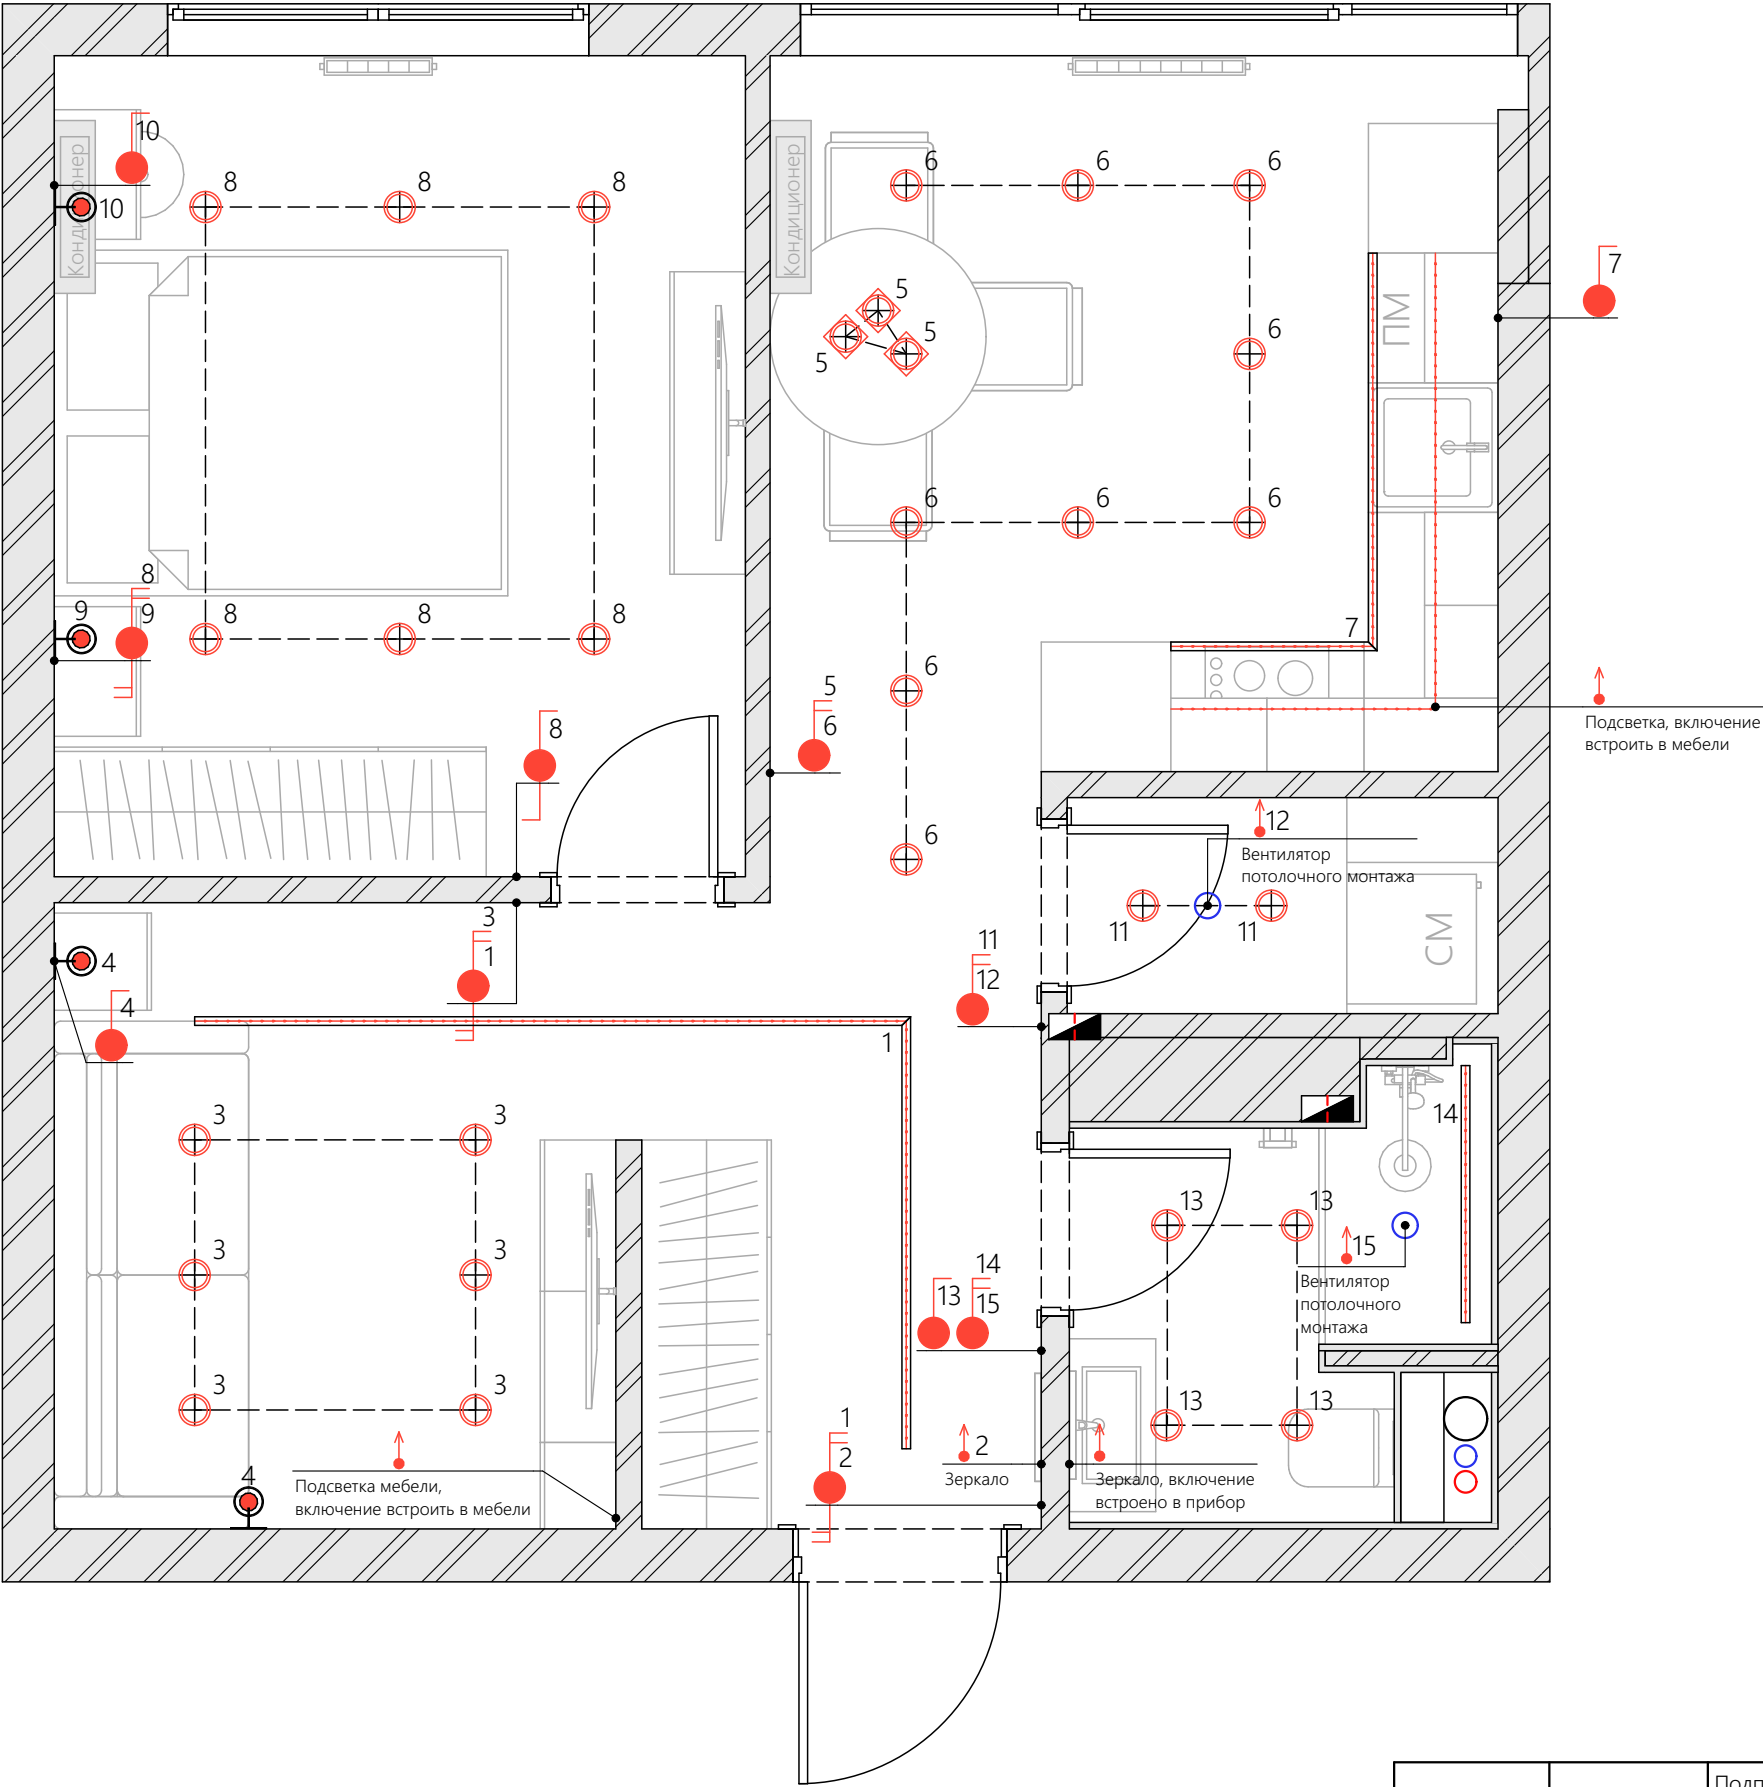


УСЛОВНЫЕ ОБОЗНАЧЕНИЯ:

	светильник встраиваемый - 27 шт.
	светильник подвесной - 3 шт.
	бра - 4 шт.
	световая линия - 9,31 м. пог.
	светодиодная лента
	электрощит
	1 кл. выключатель - 4 шт.
	2 кл. выключатель - 3 шт.
	1 кл. прох. выключатель - 1 шт.
	2 кл. прох. выключатель - 3 шт.

ПРИМЕЧАНИЯ:

- 1. Все размеры указаны в миллиметрах.
- 2. Размеры даны без учёта отделочных слоёв.
- 3. Лист смотреть совместно с развёртками стен.
- 4. Расположение осветительного оборудования указано относительно центра светильника.
- 5. Для электровыводов дать запас.
- 6. Светодиодная лента посчитана без учёта подсветки мебели.

		Подпись	Дата		Стадия	Лист	Масштаб
Руководитель					ДП	16	1:35
Дизайнер				План управления осветительным оборудованием			
Выполнил							
Заказчик							

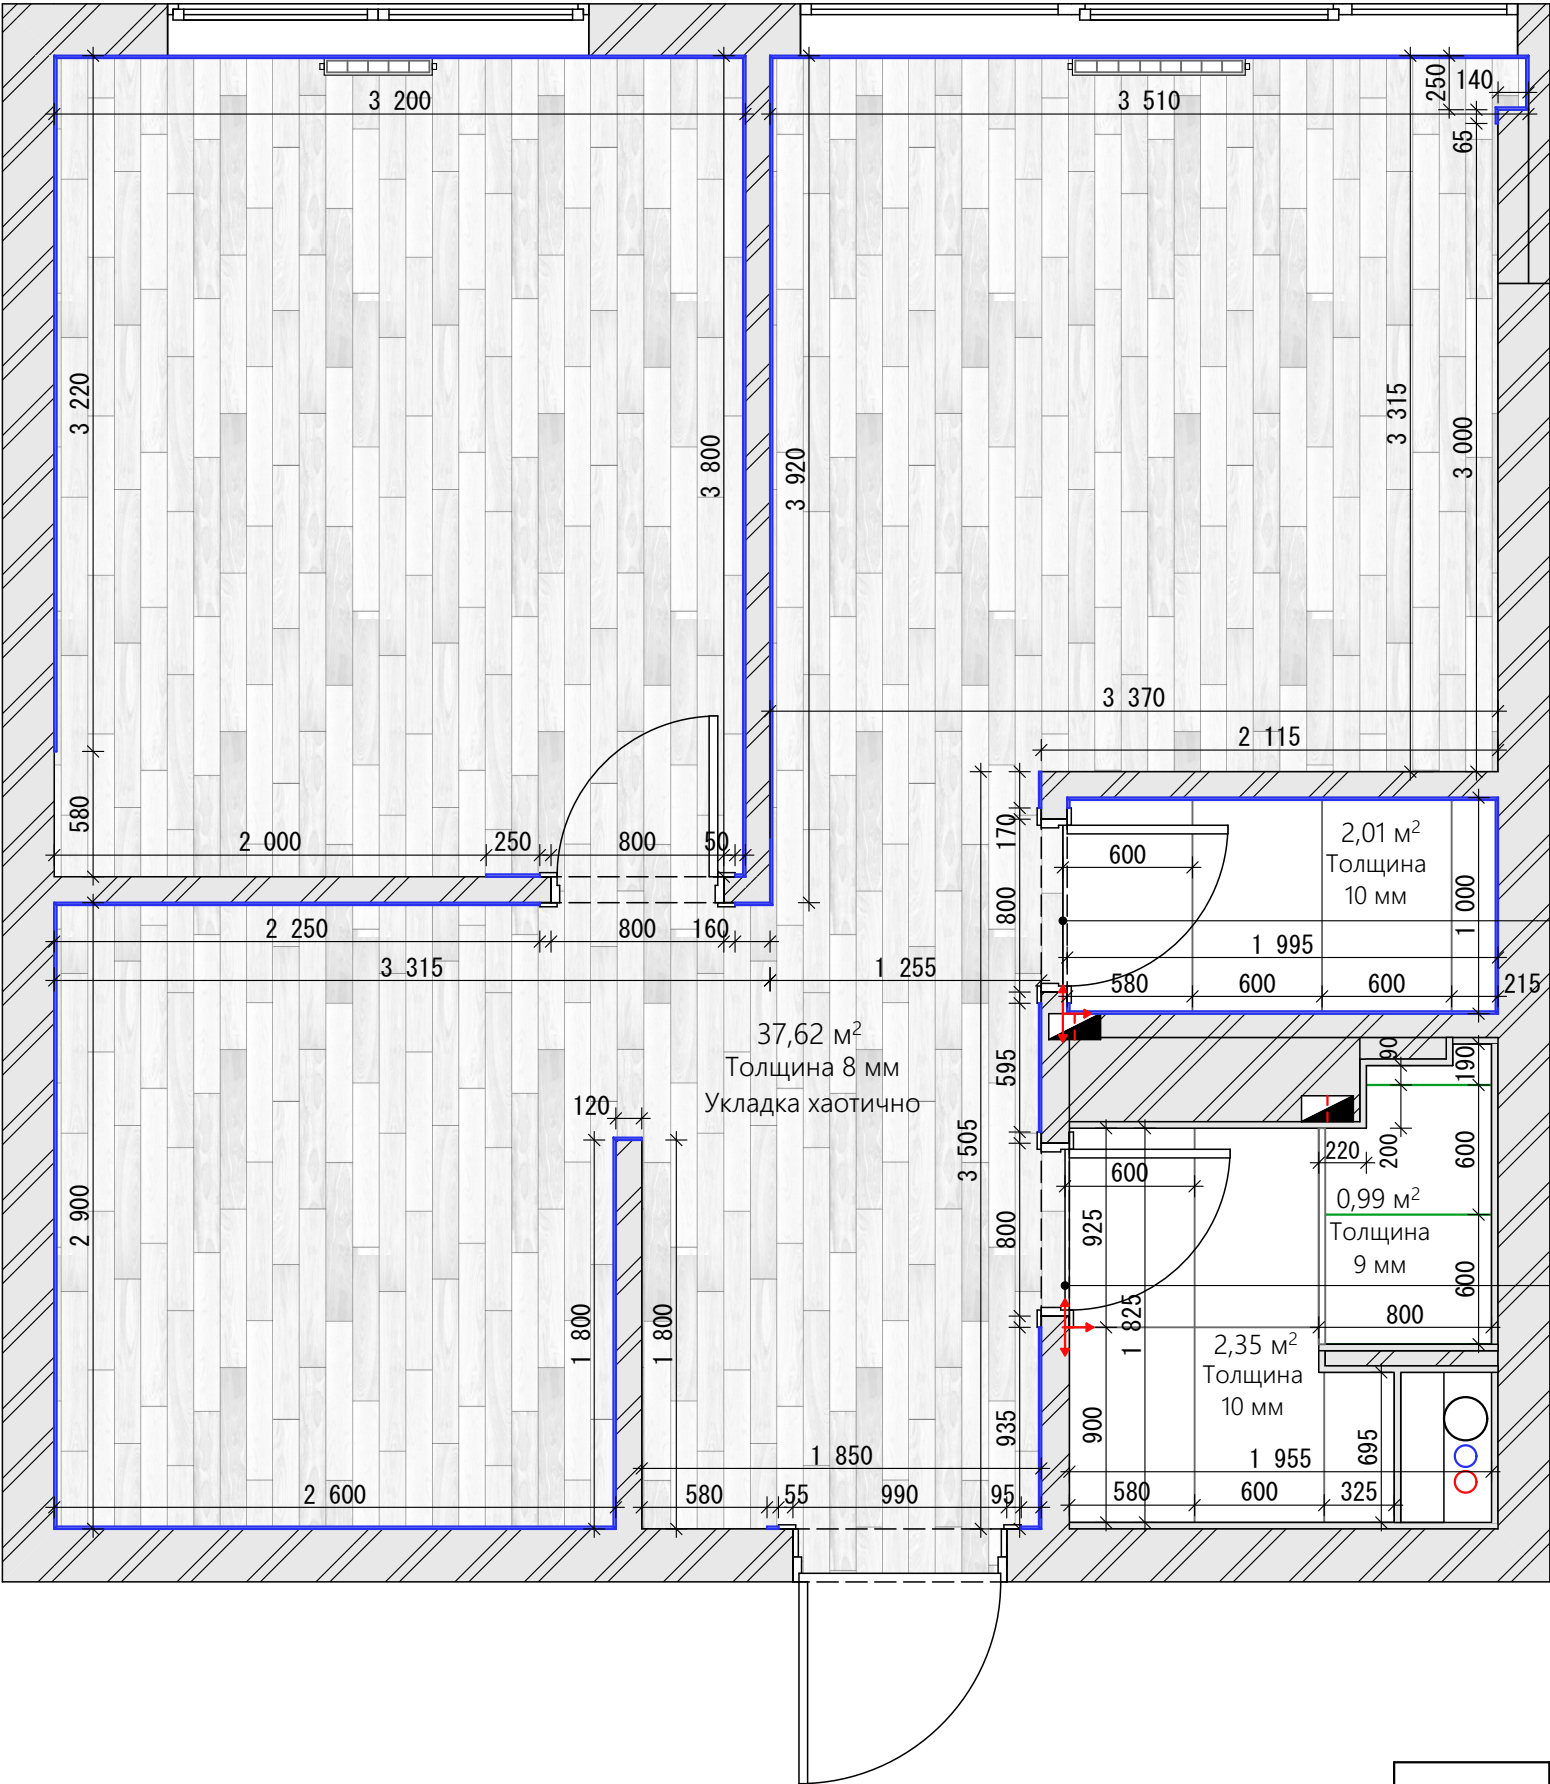

УСЛОВНЫЕ ОБОЗНАЧЕНИЯ:

вид на плане	текстура материала	наименование, количество
		Ламинат Quick-Step Венге Eligna U1300 1380*156*8 мм - S = 37,62 м²
		Керамогранит Ametis SM02 белый 1 матовый рект., 600*1200*10 мм - S = 4,36 м²
		Керамогранит AVS Lilas зелёный глянцевый рект., 600*1200*9 мм - S = 0,99 м²
		плинтус напольный мокко мдф к двери Терем Country, 2070*75*10 мм = 35,1 м. пог.
		начало расклада

Материал для стыка напольных покрытий согласовать с дизайнером, стык выполнить под дверным полотном

Материал для стыка напольных покрытий согласовать с дизайнером, стык выполнить под дверным полотном


ПРИМЕЧАНИЯ:

1. Все размеры указаны в миллиметрах.
2. Размеры даны без учёта отделочных слоёв.
3. Лист смотреть совместно с развёртками стен.
4. Все площади посчитаны без запаса.
5. Направление укладки пола и все размеры уточняются после окончания общестроительных работ.
6. Границы технологического разрыва уточнить, монтаж производить после согласования с заказчиком и дизайнером.
7. Уровень пола санузла довести до уровня чистового пола во всех помещениях.

		Подпись	Дата		Стадия	Лист	Масштаб
Руководитель					ДП	17	1:35
Дизайнер							
Выполнил							
Заказчик							
				План раскладки напольных покрытий			

Развёртки стен Прихожая

S стен = 15,73 м²

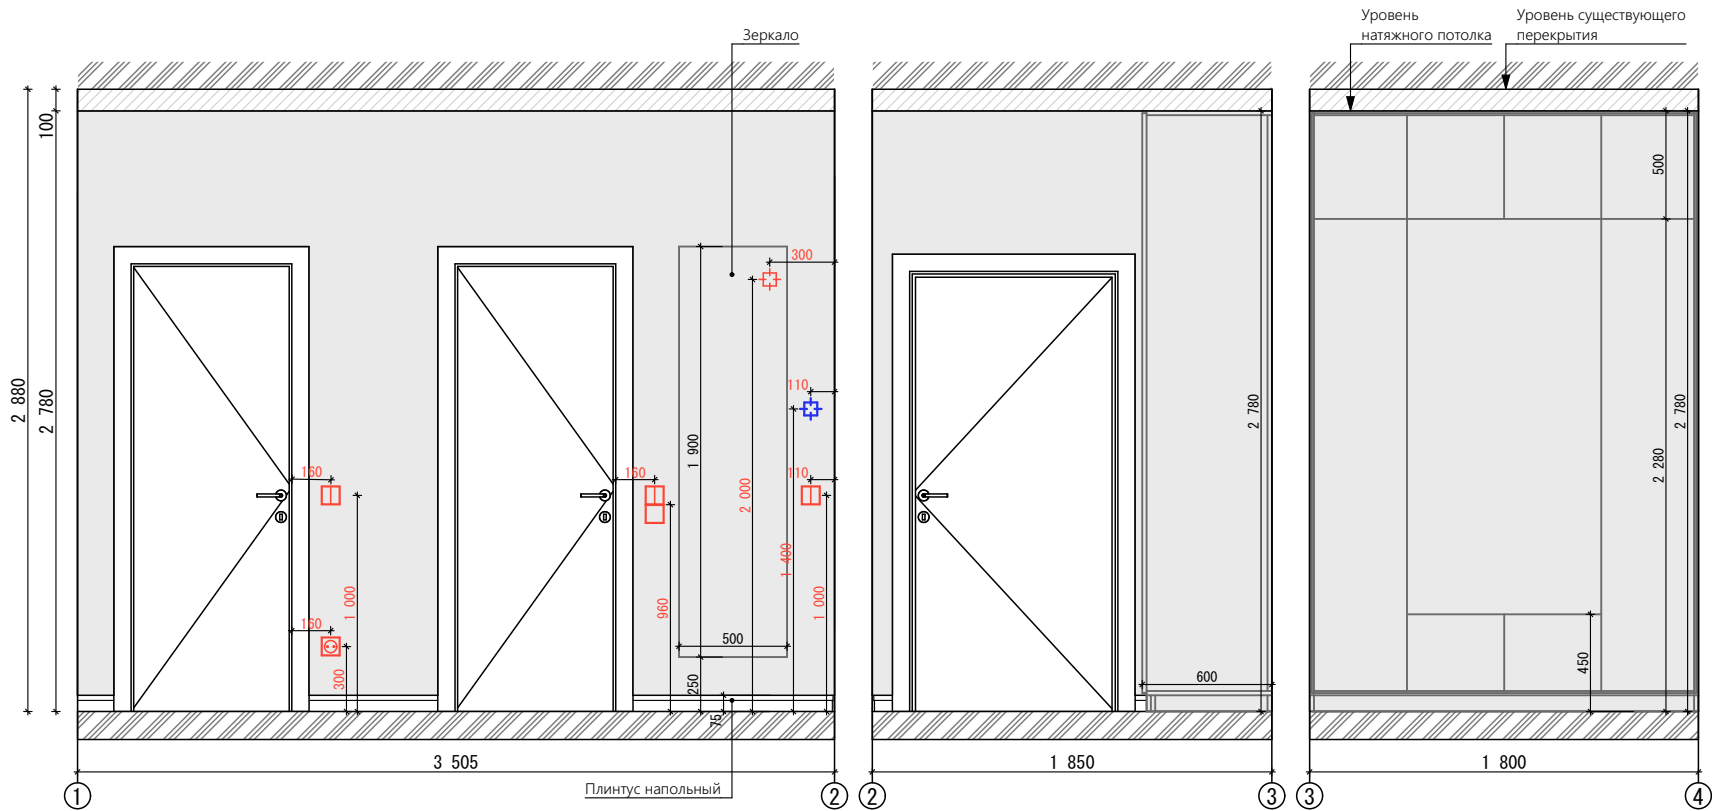


УСЛОВНЫЕ ОБОЗНАЧЕНИЯ:

	Обои однотонные флизелиновые Victoria Stenova IDEAL 287392 светлый серый, 10,05*1 м. Площадь без запаса: 13,47 м²
	Плинтус напольный мокко мдф к двери Терем Country
	выключатель двухклавишный/ выключатель одноклавишный/ розетка
	вывод для домофона/ электрический вывод


ПРИМЕЧАНИЯ:

1. Все размеры указаны в миллиметрах.
2. Размеры даны без учёта отделочных слоёв.
3. Все площади даны без запаса.
4. Размеры плинтуса смотреть на плане раскладки напольных покрытий лист №17.
5. Привязка электрики возле двери дана от дверного проёма, а не от полотна!
6. Лист смотреть совместно с 3D-визуализациями.

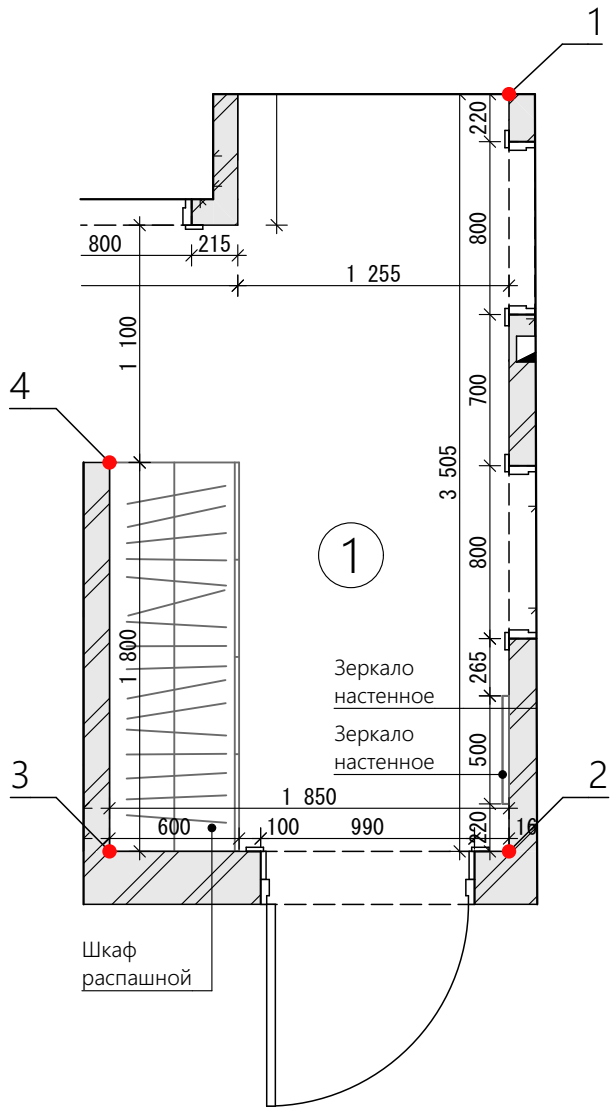

		Подпись	Дата		Стадия	Лист	Масштаб
Руководитель					ДП	18	1:35
Дизайнер							
Выполнил							
Заказчик							


Развёртки стен Прихожая
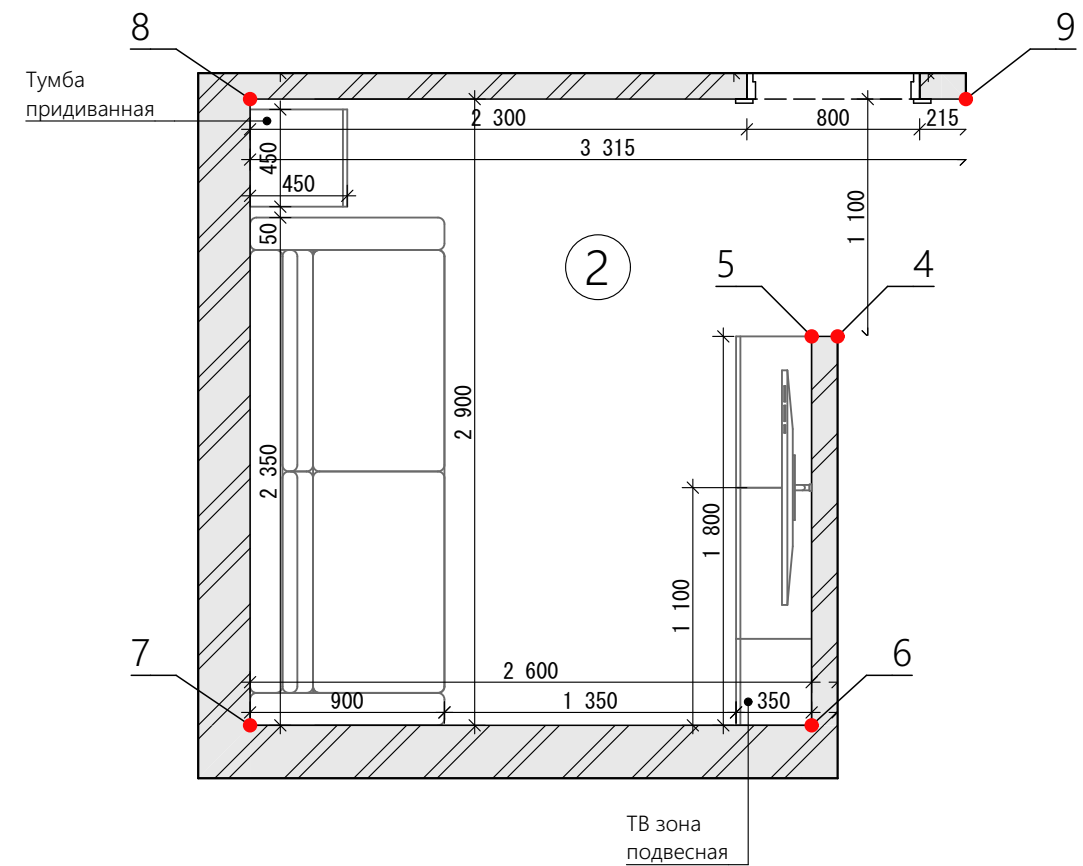
$$S_{\text{стен}} = 29,37 \text{ м}^2$$


ПРИМЕЧАНИЯ:


1. Все размеры указаны в миллиметрах.
2. Размеры даны без учёта отделочных слоёв.
3. Все площади даны без запаса.
4. Размеры плинтуса смотреть на плане раскладки напольных покрытий лист №17.
5. Привязка электрики возле двери дана от дверного проёма, а не от полотна!
6. Лист смотреть совместно с 3D-визуализациями.

		Подпись	Дата		Стадия	Лист	Масштаб
Руководитель					ДП	19	1:35
Дизайнер				Развёртки стен Гостиная			
Выполнил							
Заказчик							

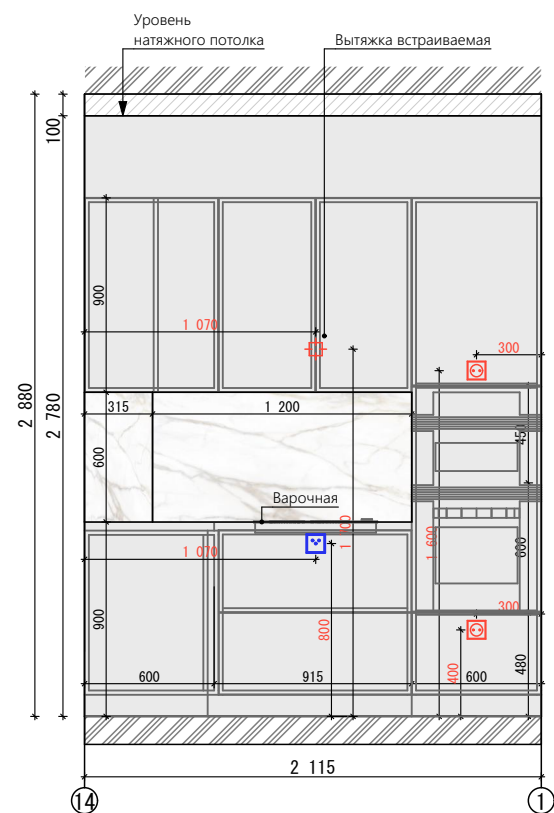
$$S_{\text{стен}} = 31,31 \text{ м}^2$$


	Обои однотонные флизелиновые Victoria Stenova IDEAL 287392 светлый серый, 10,05*1 м. Площадь без запаса: 22,59 м ²
	Обои Wall Street Pifagorica 9 frost, 2705*1800 мм, цвет согласовать по цветопробе. Площадь без запаса: 4,87 м ²
	Laconistiq. Теневая рейка CLASSIC 8,8*10,7*3000 мм, чёрная матовая. Алюминий. Количество без запаса: 5,41 м. пог.
	Керамогранит Ametis SM02 белый 1 матовый 600*1200*10 мм, реттифициров, затирка Мареи 103. Площадь без запаса: 2,35 м ²
	Плинтус напольный мокко мдф к двери Терем Country
	выключатель двухклавишный/ выключатель одноклавишный/ розетка/силовой вывод
	электрический вывод

1. Все размеры указаны в миллиметрах.
2. Размеры даны без учёта отделочных слоёв.
3. Все площади даны без запаса.
4. Размеры плинтуса смотреть на плане раскладки напольных покрытий лист №17.
5. Привязка электрики возле двери дана от дверного проёма, а не от полотна!
6. Лист смотреть совместно с 3D-визуализациями.

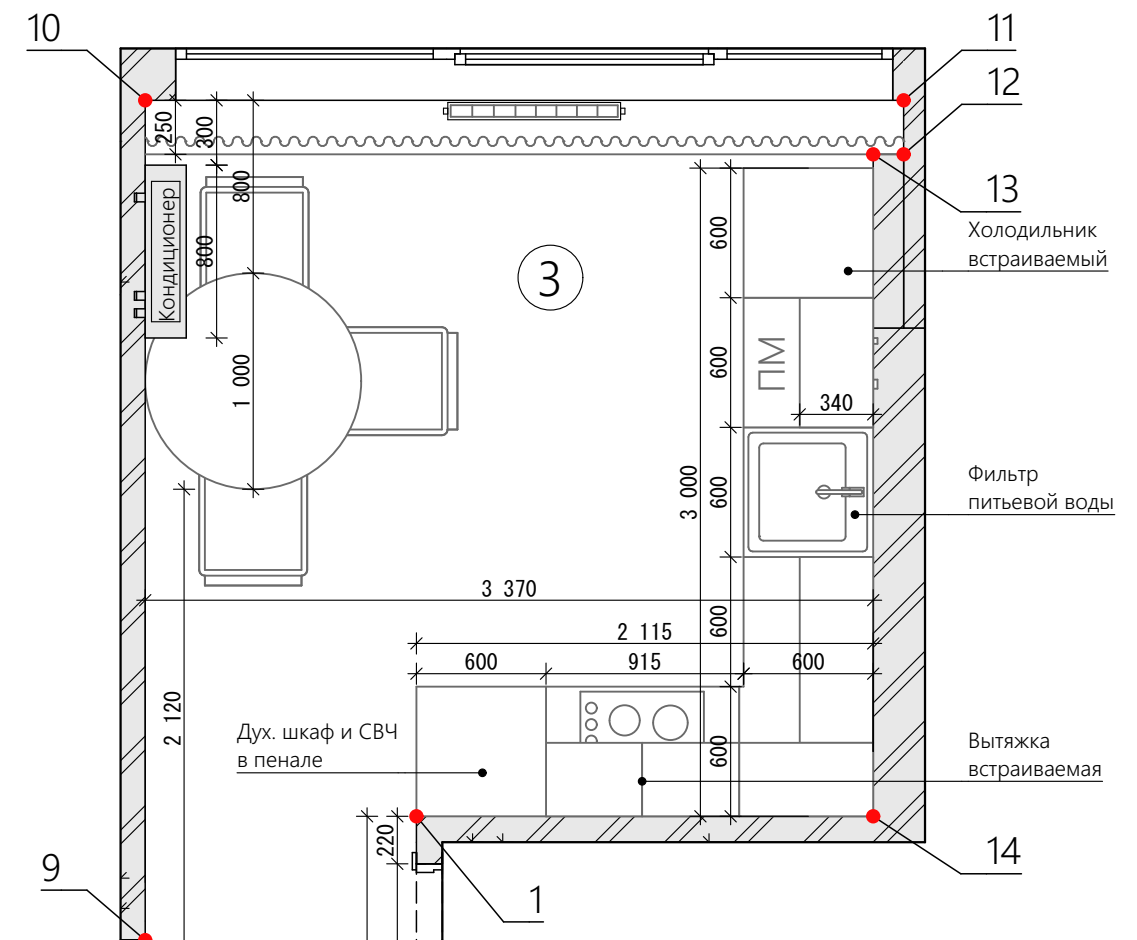


		Подпись	Дата		Стадия	Лист	Масштаб
Руководитель					ДП	20	1:35
Дизайнер				Развёртки стен Кухня			
Выполнил							
Заказчик							
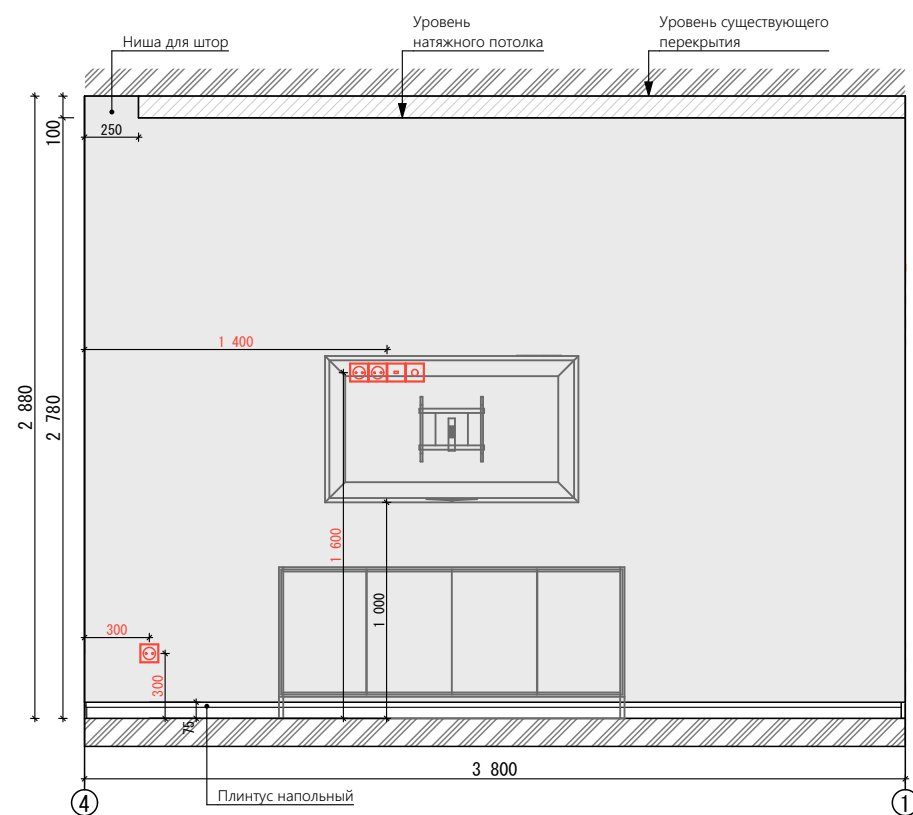
$$S_{\text{стен}} = 35,01 \text{ м}^2$$


	Обои однотонные флизелиновые Victoria Stenova IDEAL 287392 светлый серый, 10,05*1 м. Площадь без запаса: 23,14 м²
	Обои Wall Street Altay 1 frost, 2705*3550 мм, цвет согласовать по цветопробе. Площадь без запаса: 9,65 м²
	Плнтус напольный мокко мдф к двери Терем Country
	выключатель двухклавишный/ выключатель одноклавишный/ розетка/розетка тв/ розетка интернет
	электрический вывод


1. Все размеры указаны в миллиметрах.
2. Размеры даны без учёта отделочных слоёв.
3. Все площади даны без запаса.
4. Размеры плинтуса смотреть на плане раскладки напольных покрытий лист №17.
5. Привязка электрики возле двери дана от дверного проёма, а не от полотна!
6. Лист смотреть совместно с 3D-визуализациями.

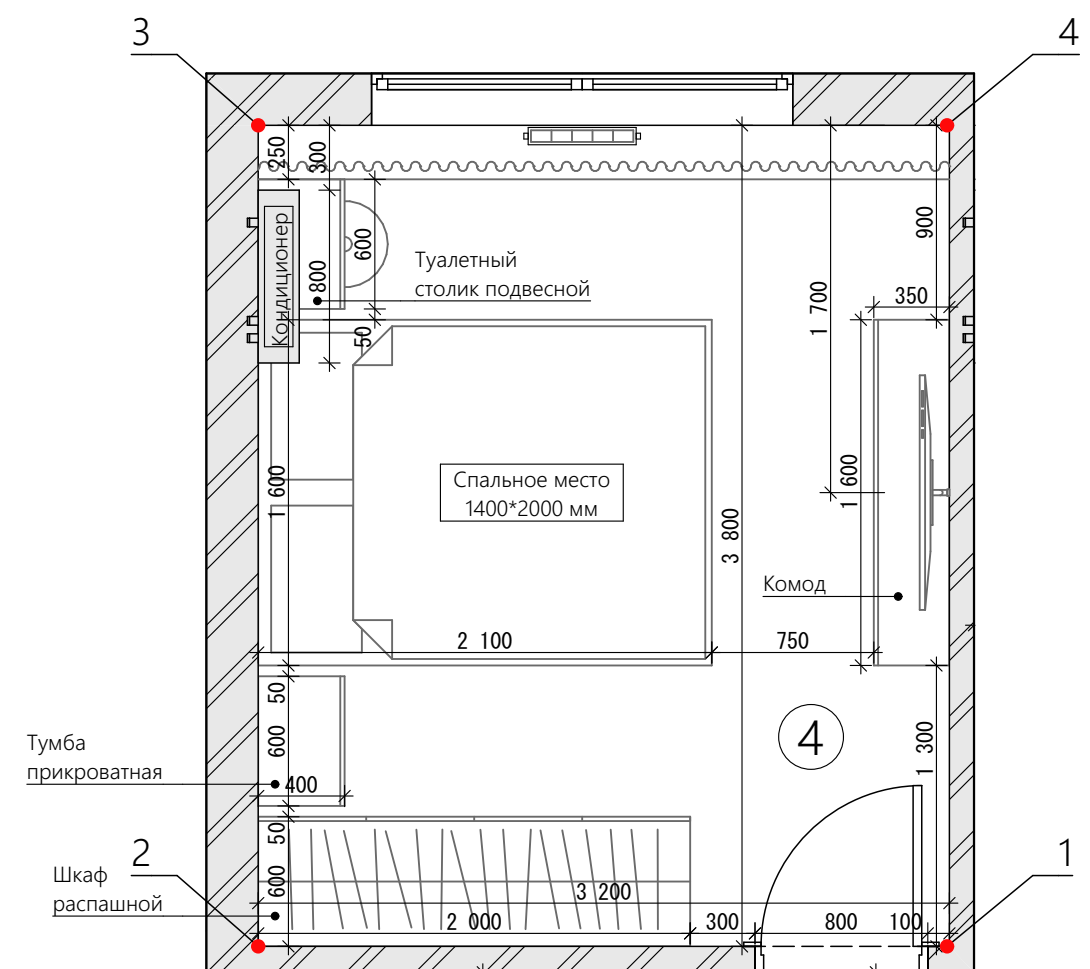

		Подпись	Дата	Развёртки стен Спальня	Стадия	Лист	Масштаб
Руководитель					ДП	21	1:35
Дизайнер							
Выполнил							
Заказчик							


Развёртки стен Постирочная

S стен = 15,71 м²

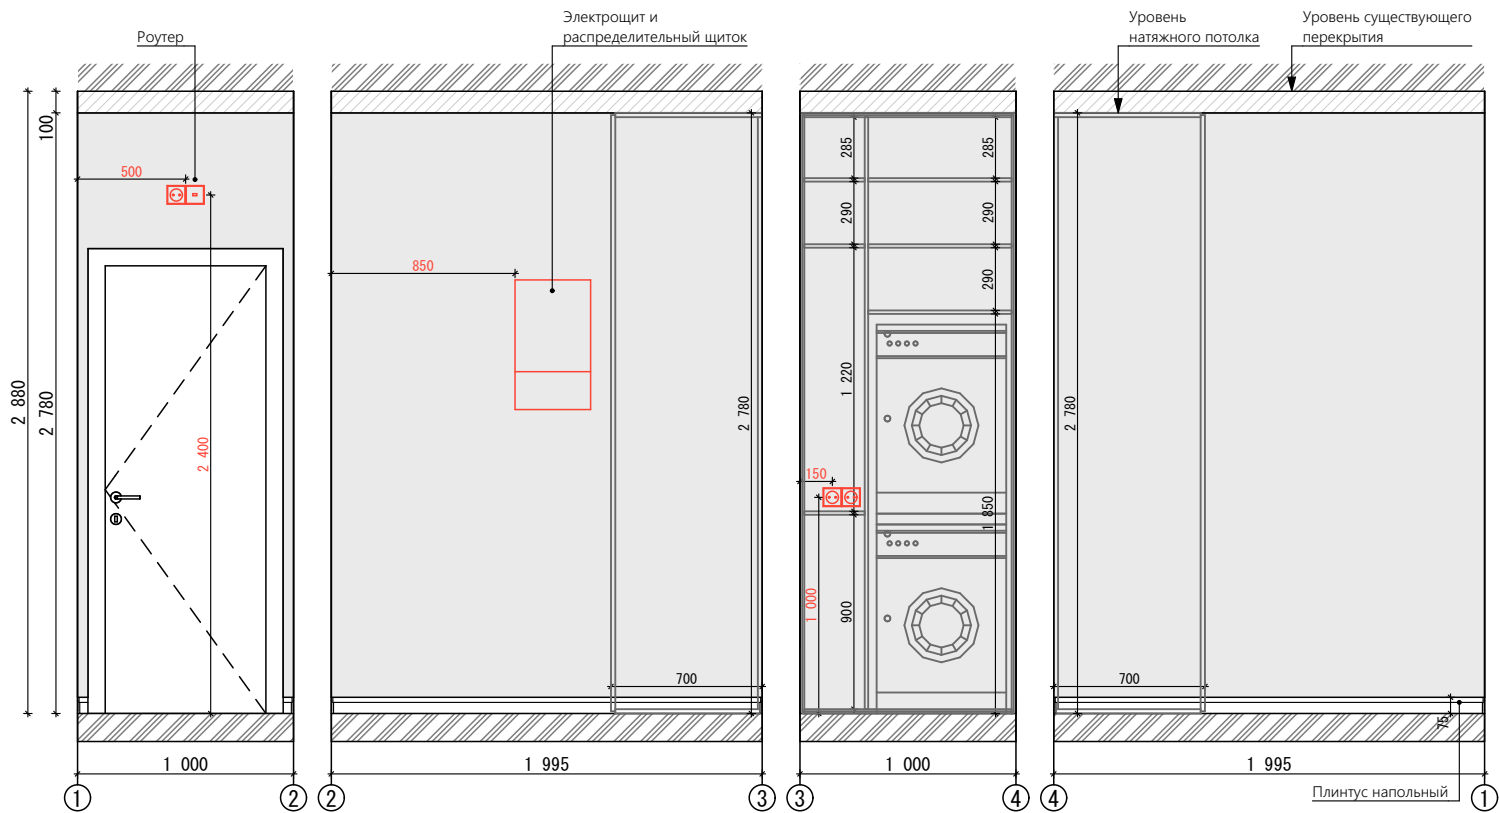

УСЛОВНЫЕ ОБОЗНАЧЕНИЯ:

	Обои однотонные флизелиновые Victoria Stenova IDEAL 287392 светлый серый, 10,05*1 м. Площадь без запаса: 14,41 м²
	Плинтус напольный мокко мдф к двери Терем Country
	розетка/розетка интернет

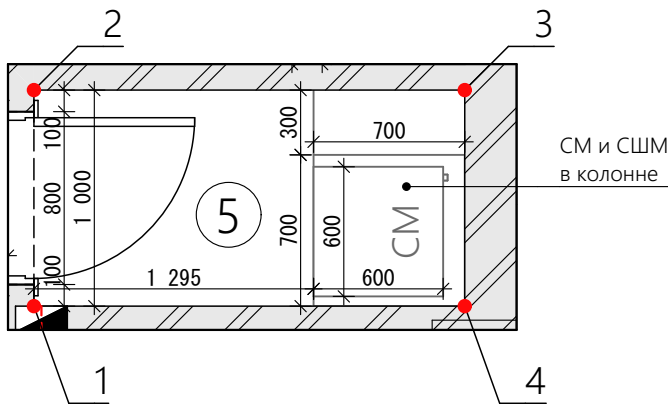

ПРИМЕЧАНИЯ:

1. Все размеры указаны в миллиметрах.
2. Размеры даны без учёта отделочных слоёв.
3. Все площади даны без запаса.
4. Размеры плинтуса смотреть на плане раскладки напольных покрытий лист №17.
5. Привязка электрики возле двери дана от дверного проёма, а не от полотна!
6. Лист смотреть совместно с 3D-визуализациями.

		Подпись	Дата		Стадия	Лист	Масштаб
Руководитель					ДП	22	1:35
Дизайнер							
Выполнил							
Заказчик							

Развёртки стен Постирочная

